
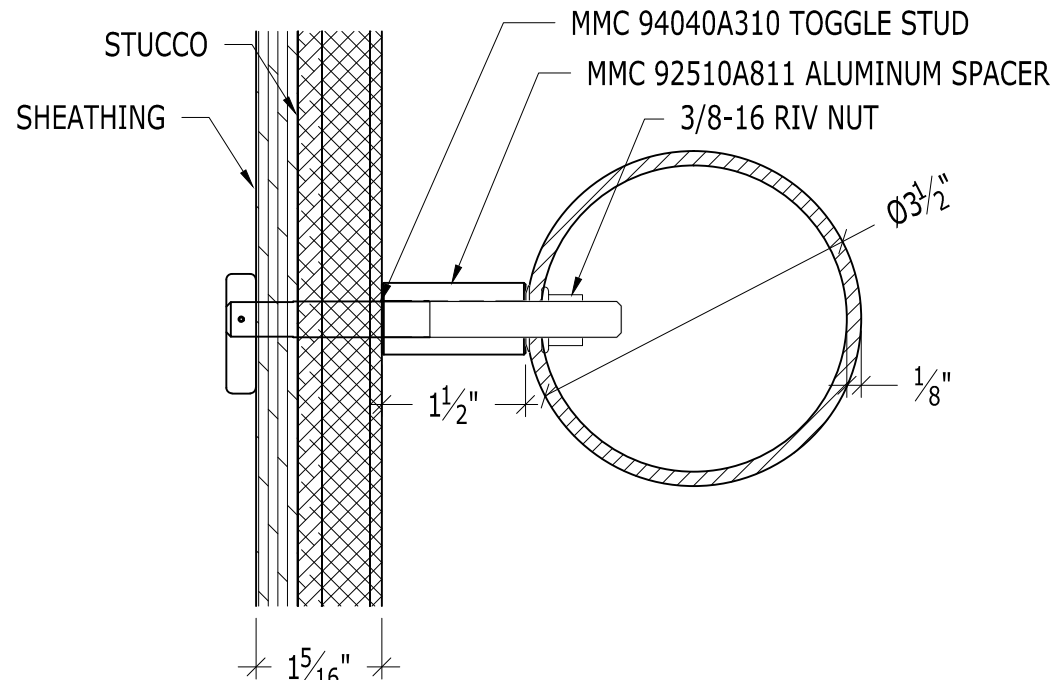
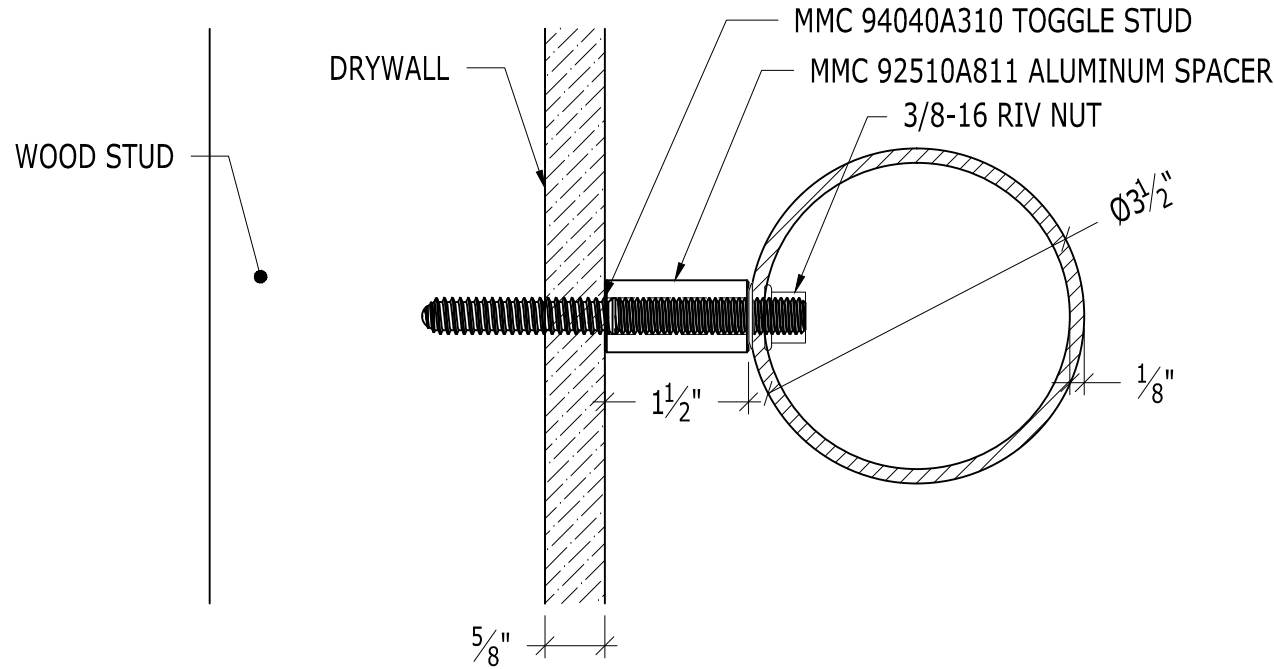
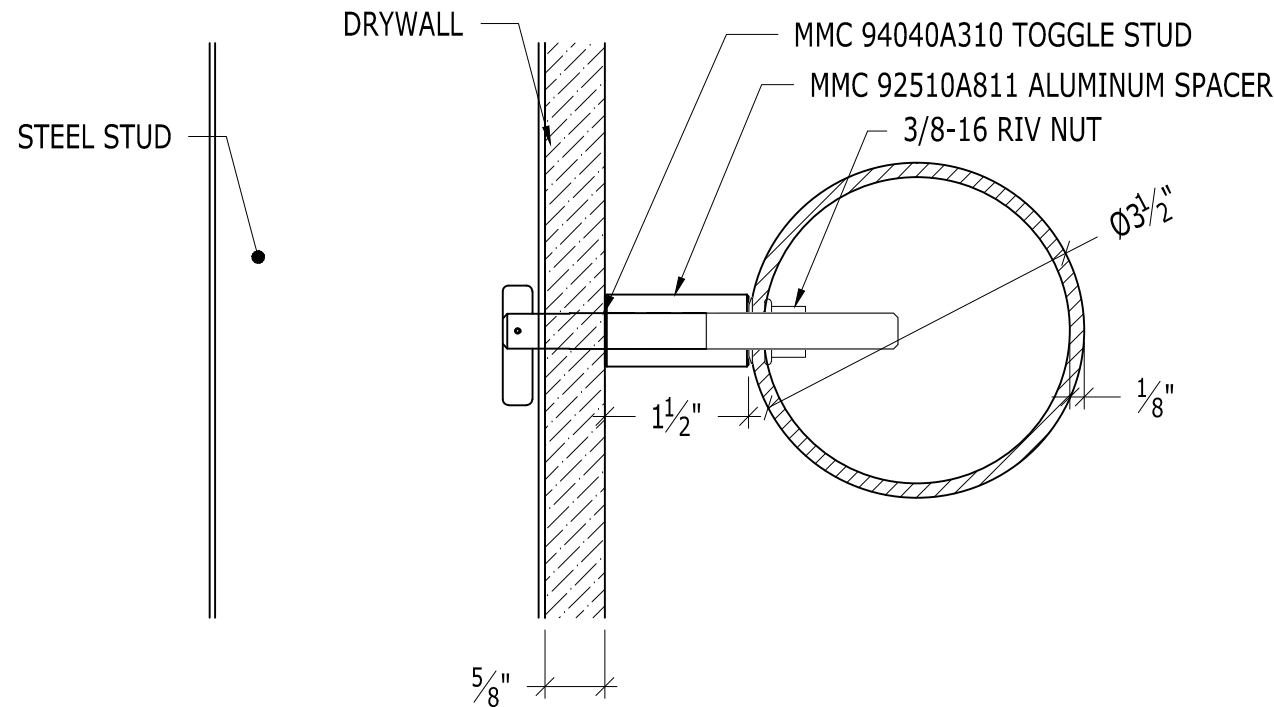


JACK ANDERSON
FABRICATION DESIGN
3326 CAZADOR STREET
LOS ANGELES CA 90065
623-419-4802
jack4congrss@protonmail.com


LOS ANGELES SOLAR SYSTEM PROJECT
WALL MOUNT MERCURY

2800 E. Observatory Rd
Los Angeles, CA 90027


DRAWN BY	JACK
DRAWING DATE	2-5-2026
REVISION DATE	--/--/----
TITLE	ELEVATION, SECTIONS
SCALE	AS NOTED
SHEET	ME100

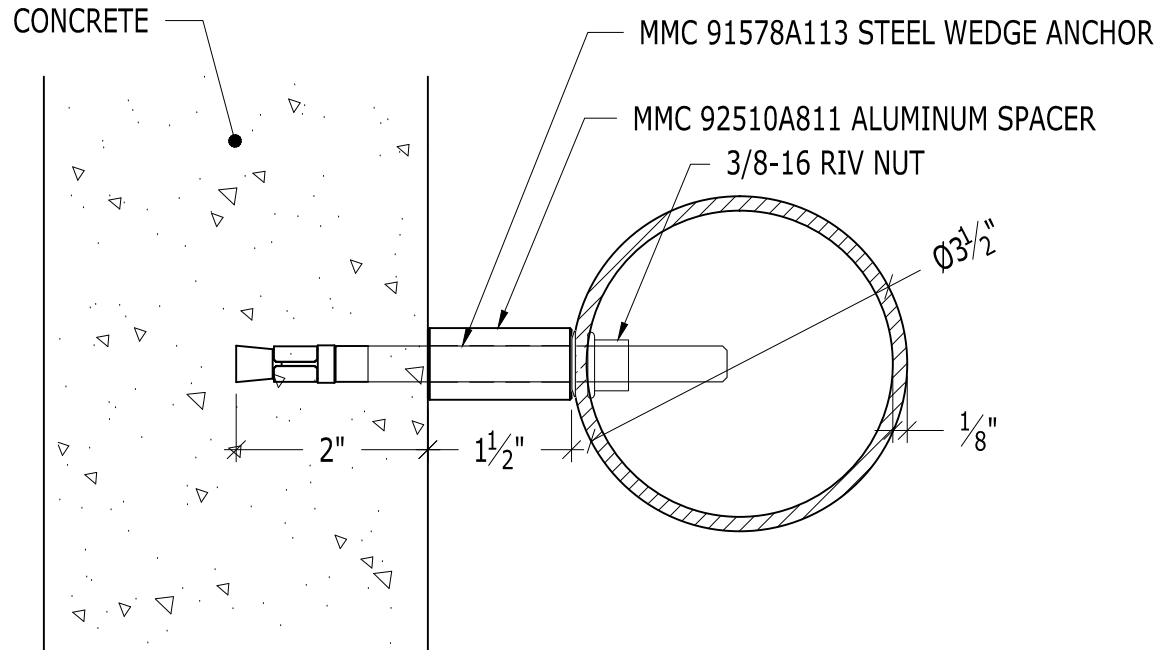


1 SECTION - INSTALLATION
SCALE: HALF SCALE

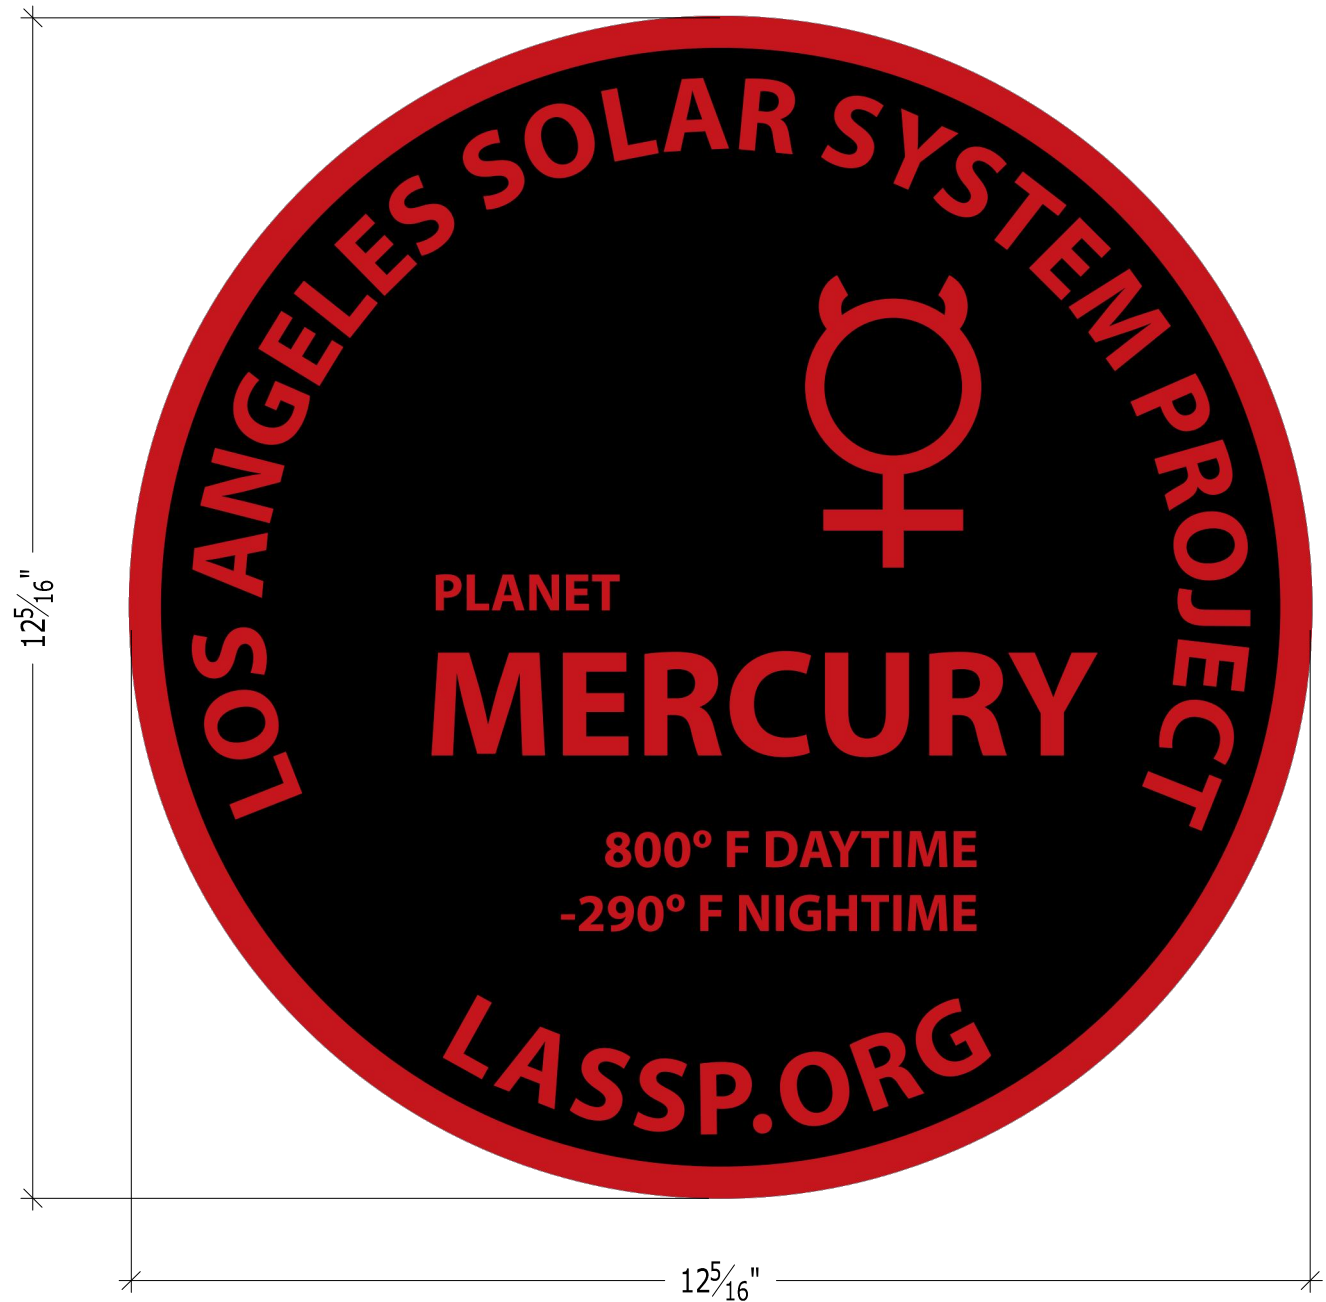


B ELEVATION - COMPANION GRAPHIC
SCALE: HALF SCALE

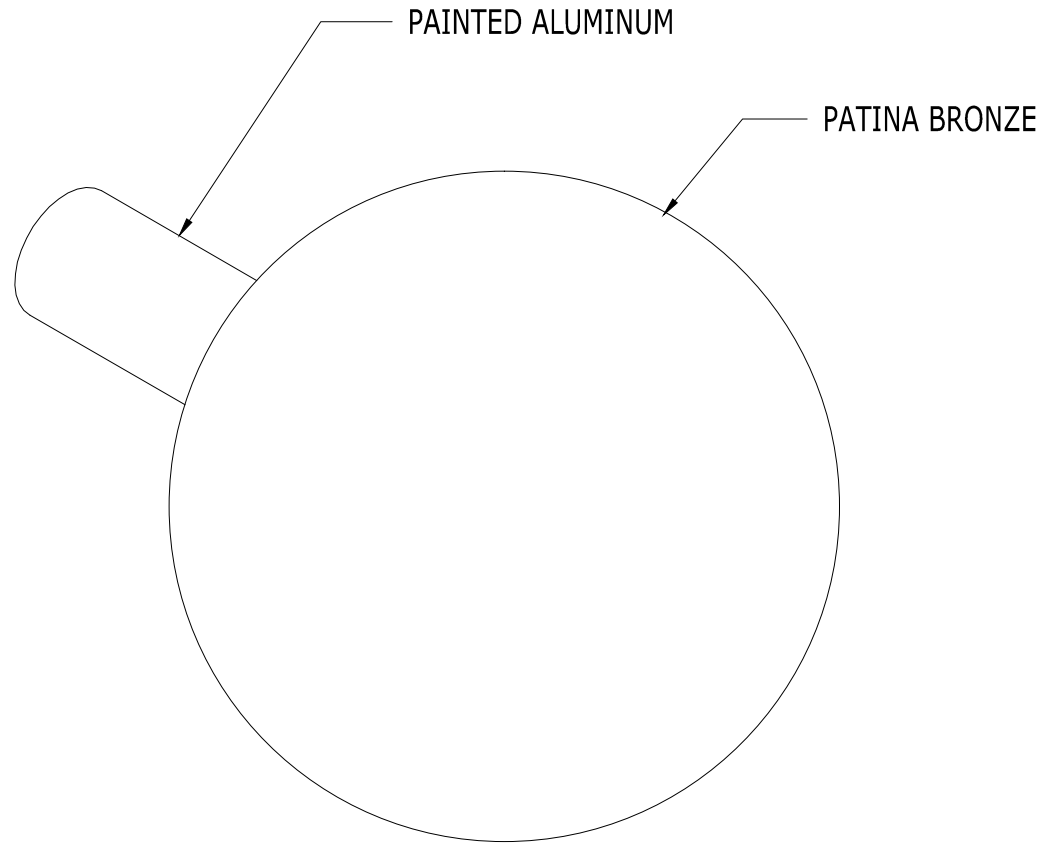

ISO VIEW
NTS


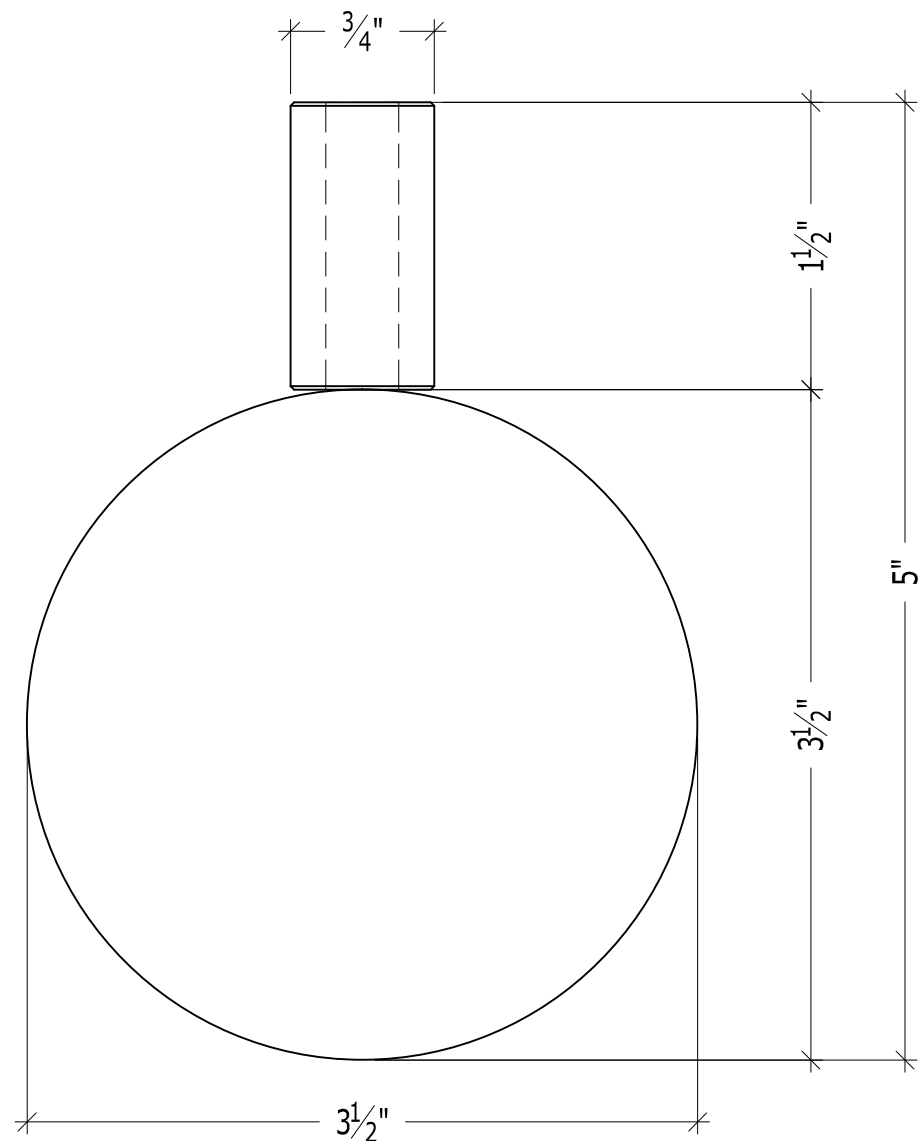


PLAN -
SCALE: FULL SCALE

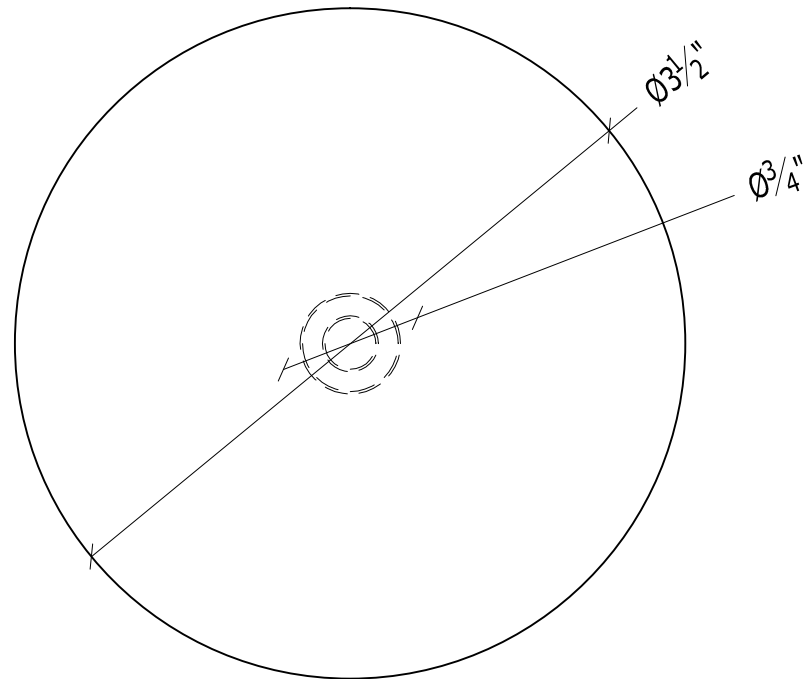


A ELEVATION -
SCALE: FULL SCALE



FOR REVIEW

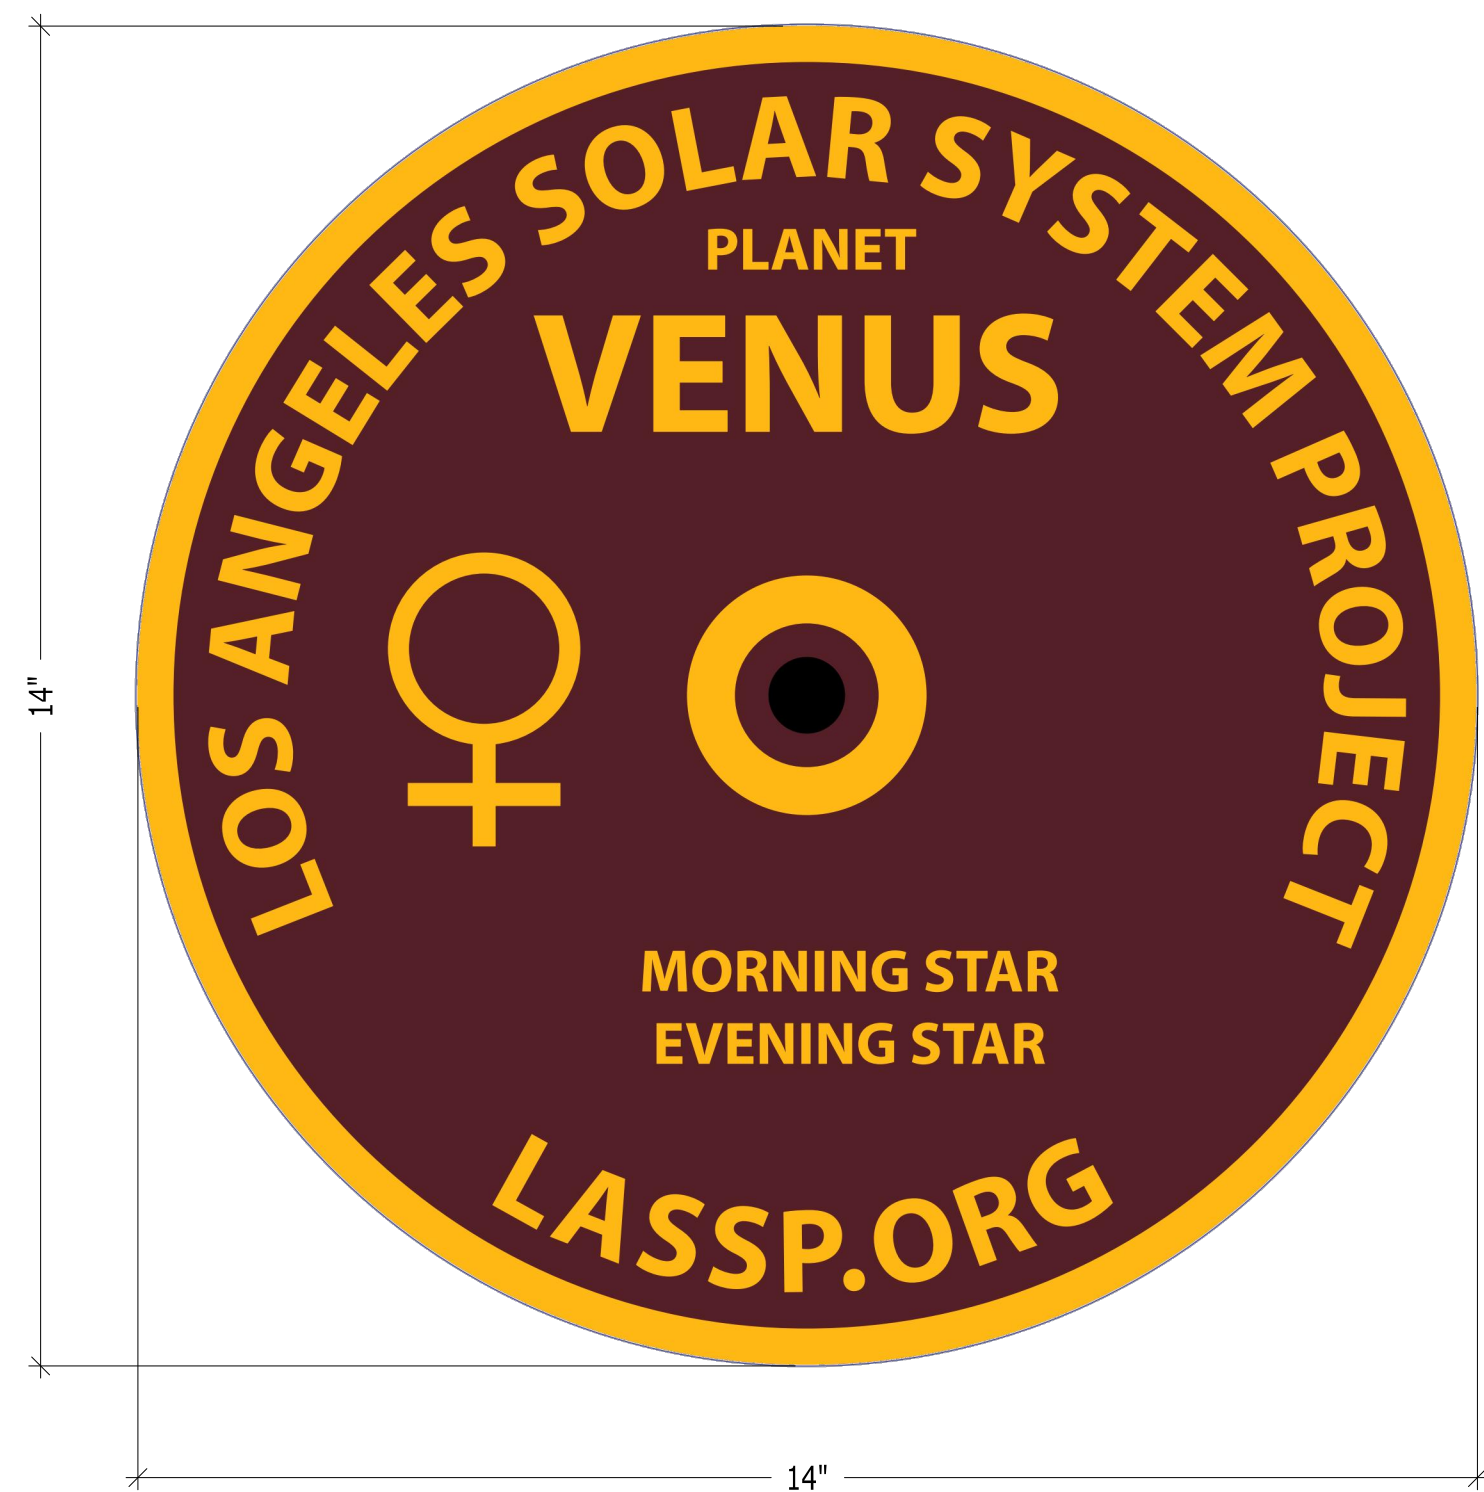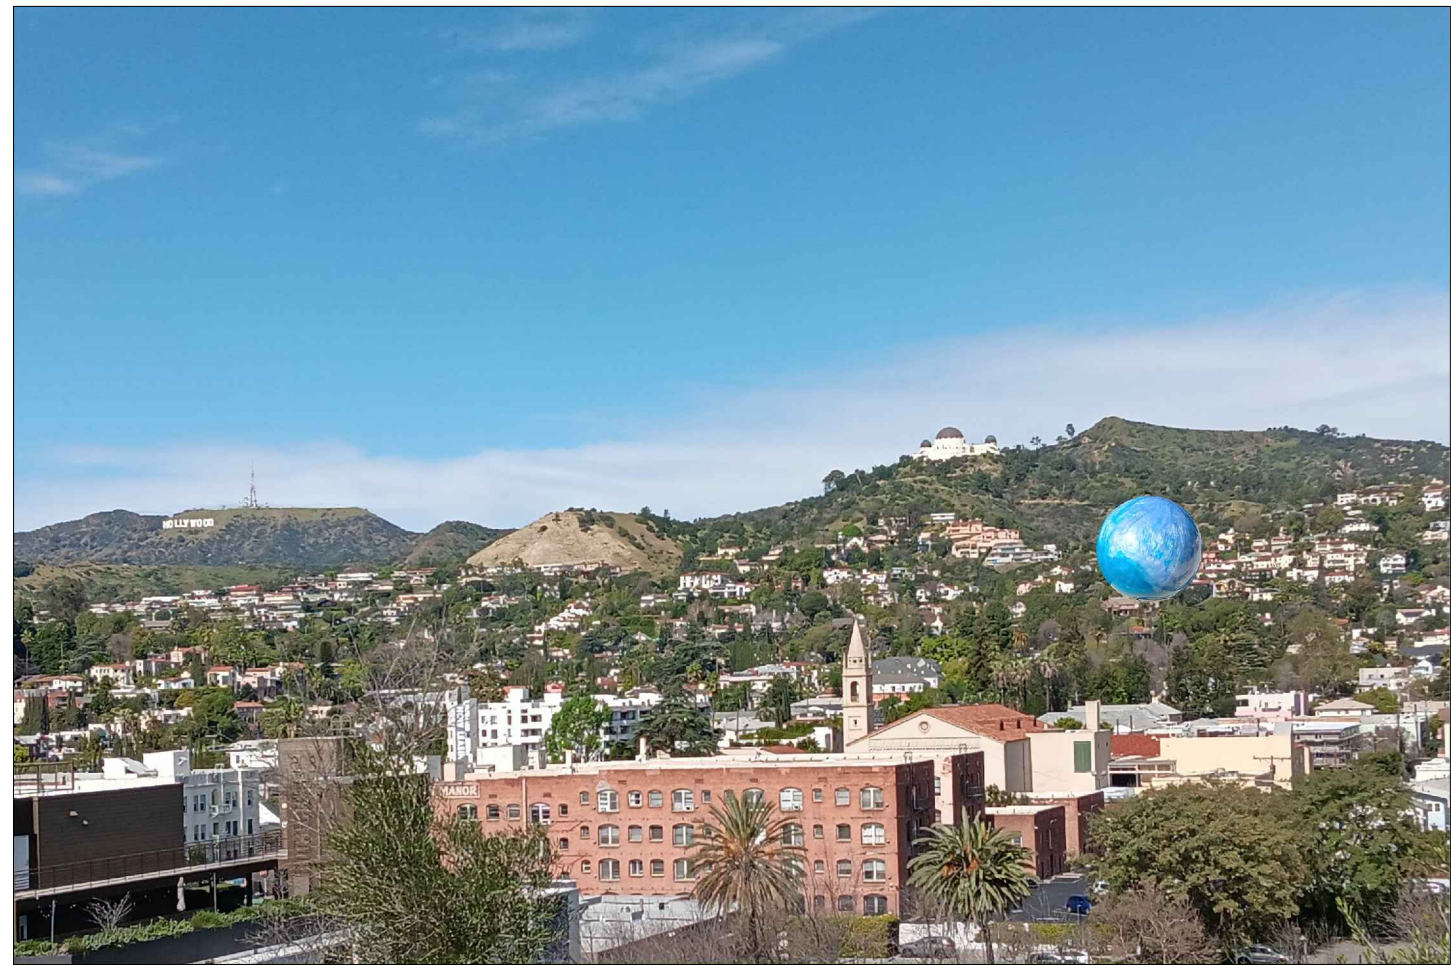


A PLAN DETAIL - BRONZE
SCALE: HALF SCALE

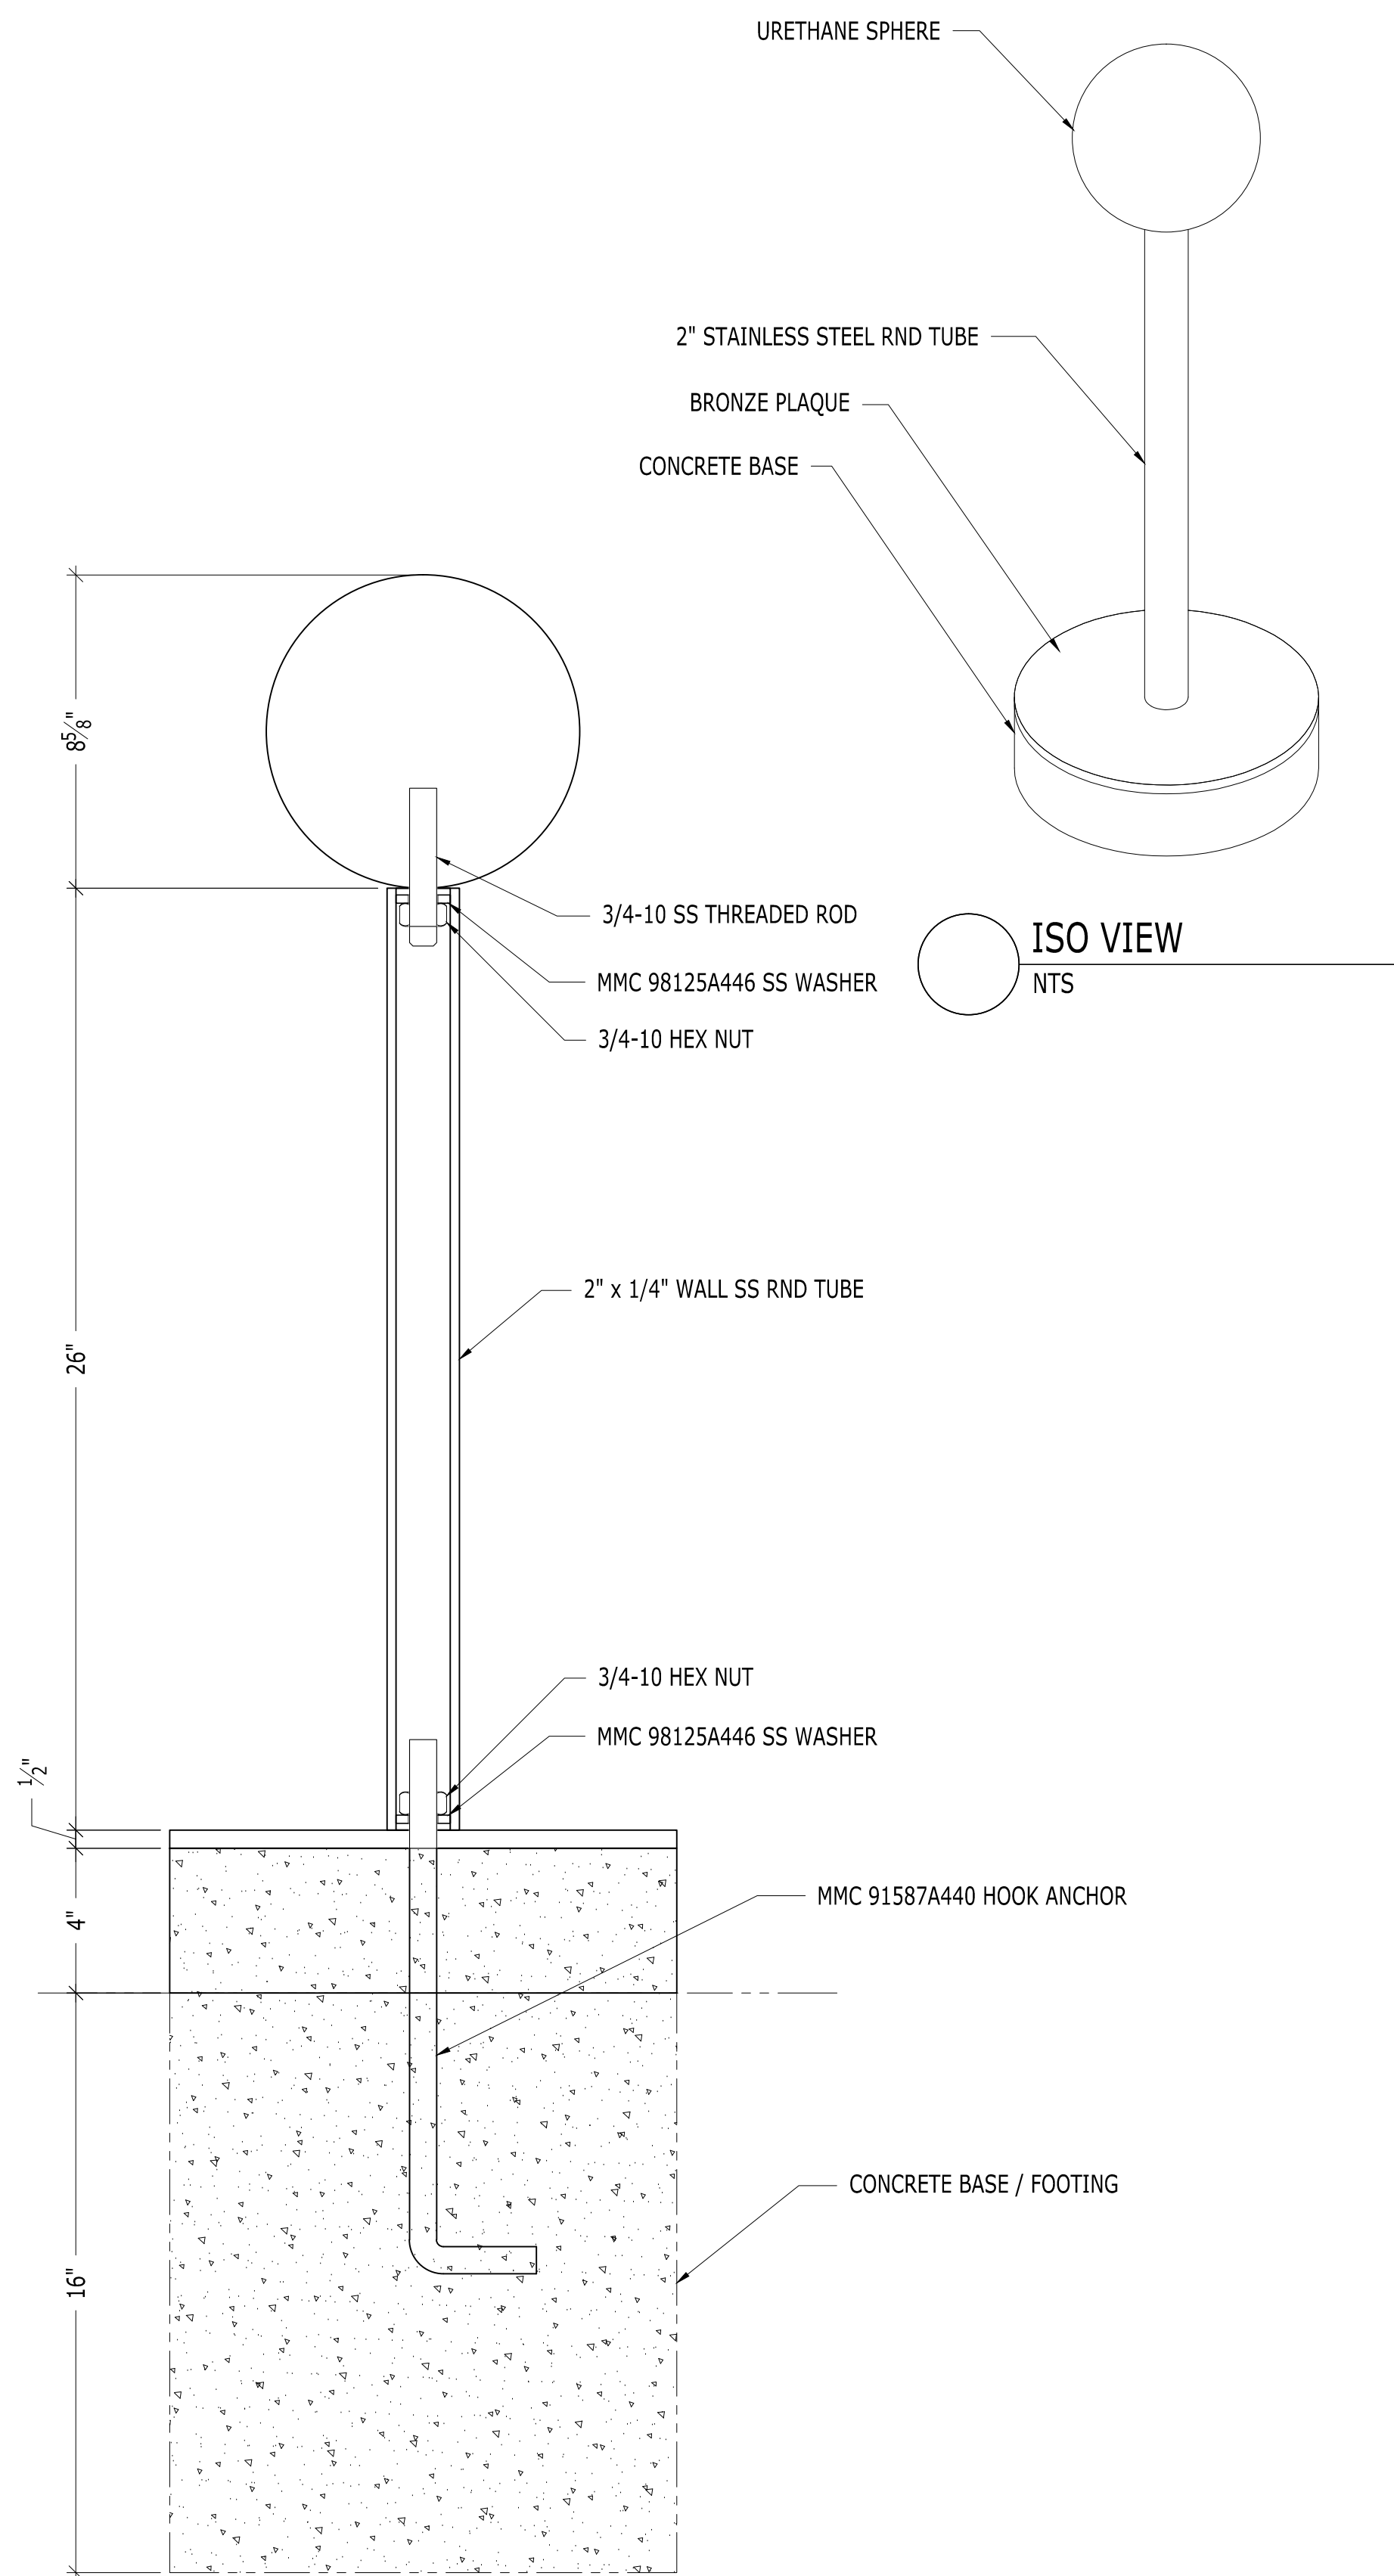

1 SECTION -
SCALE: 3" = 1'-0"

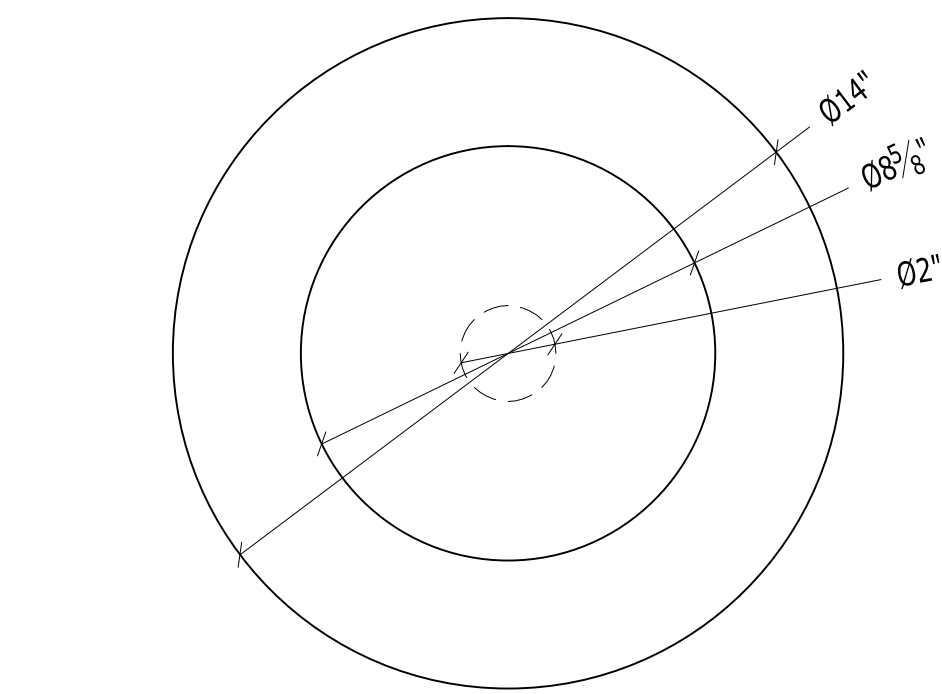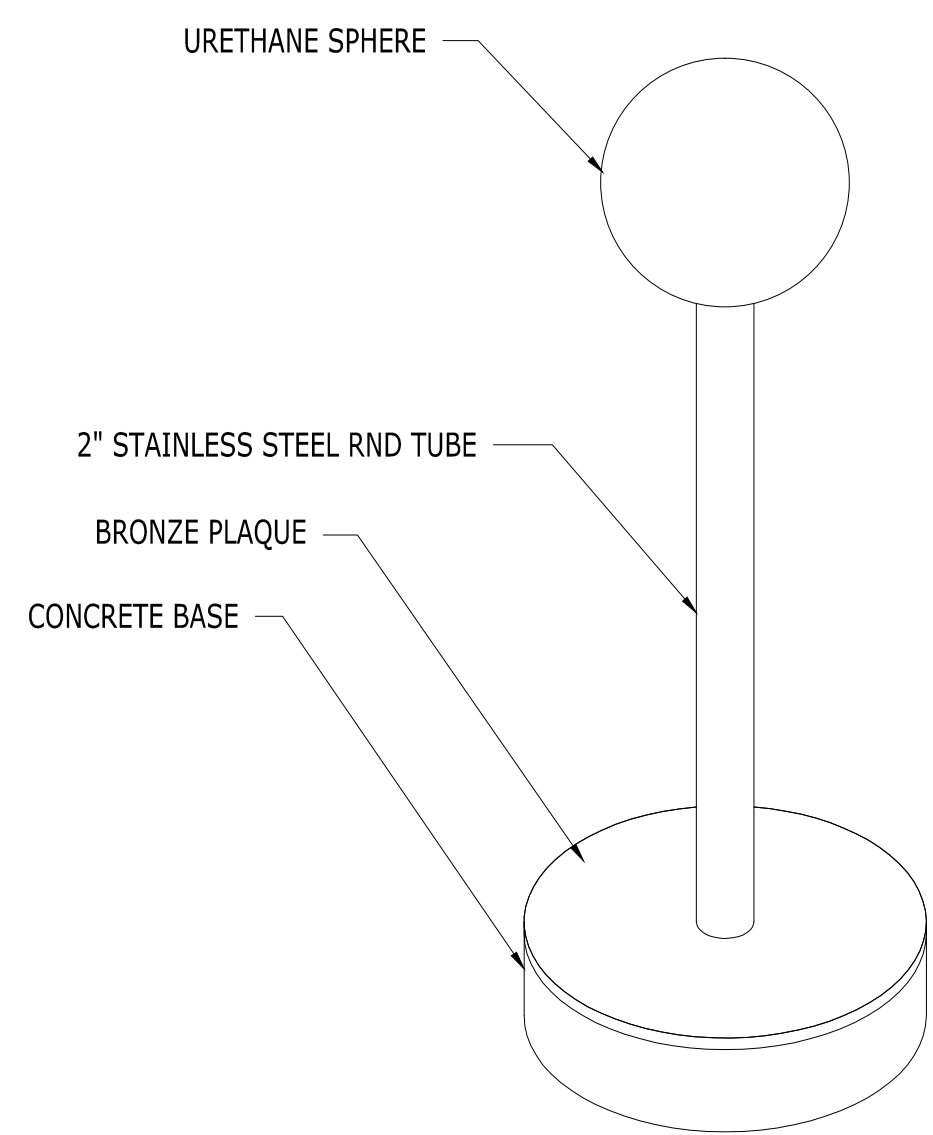

PLAN -
SCALE: 3" = 1'-0"

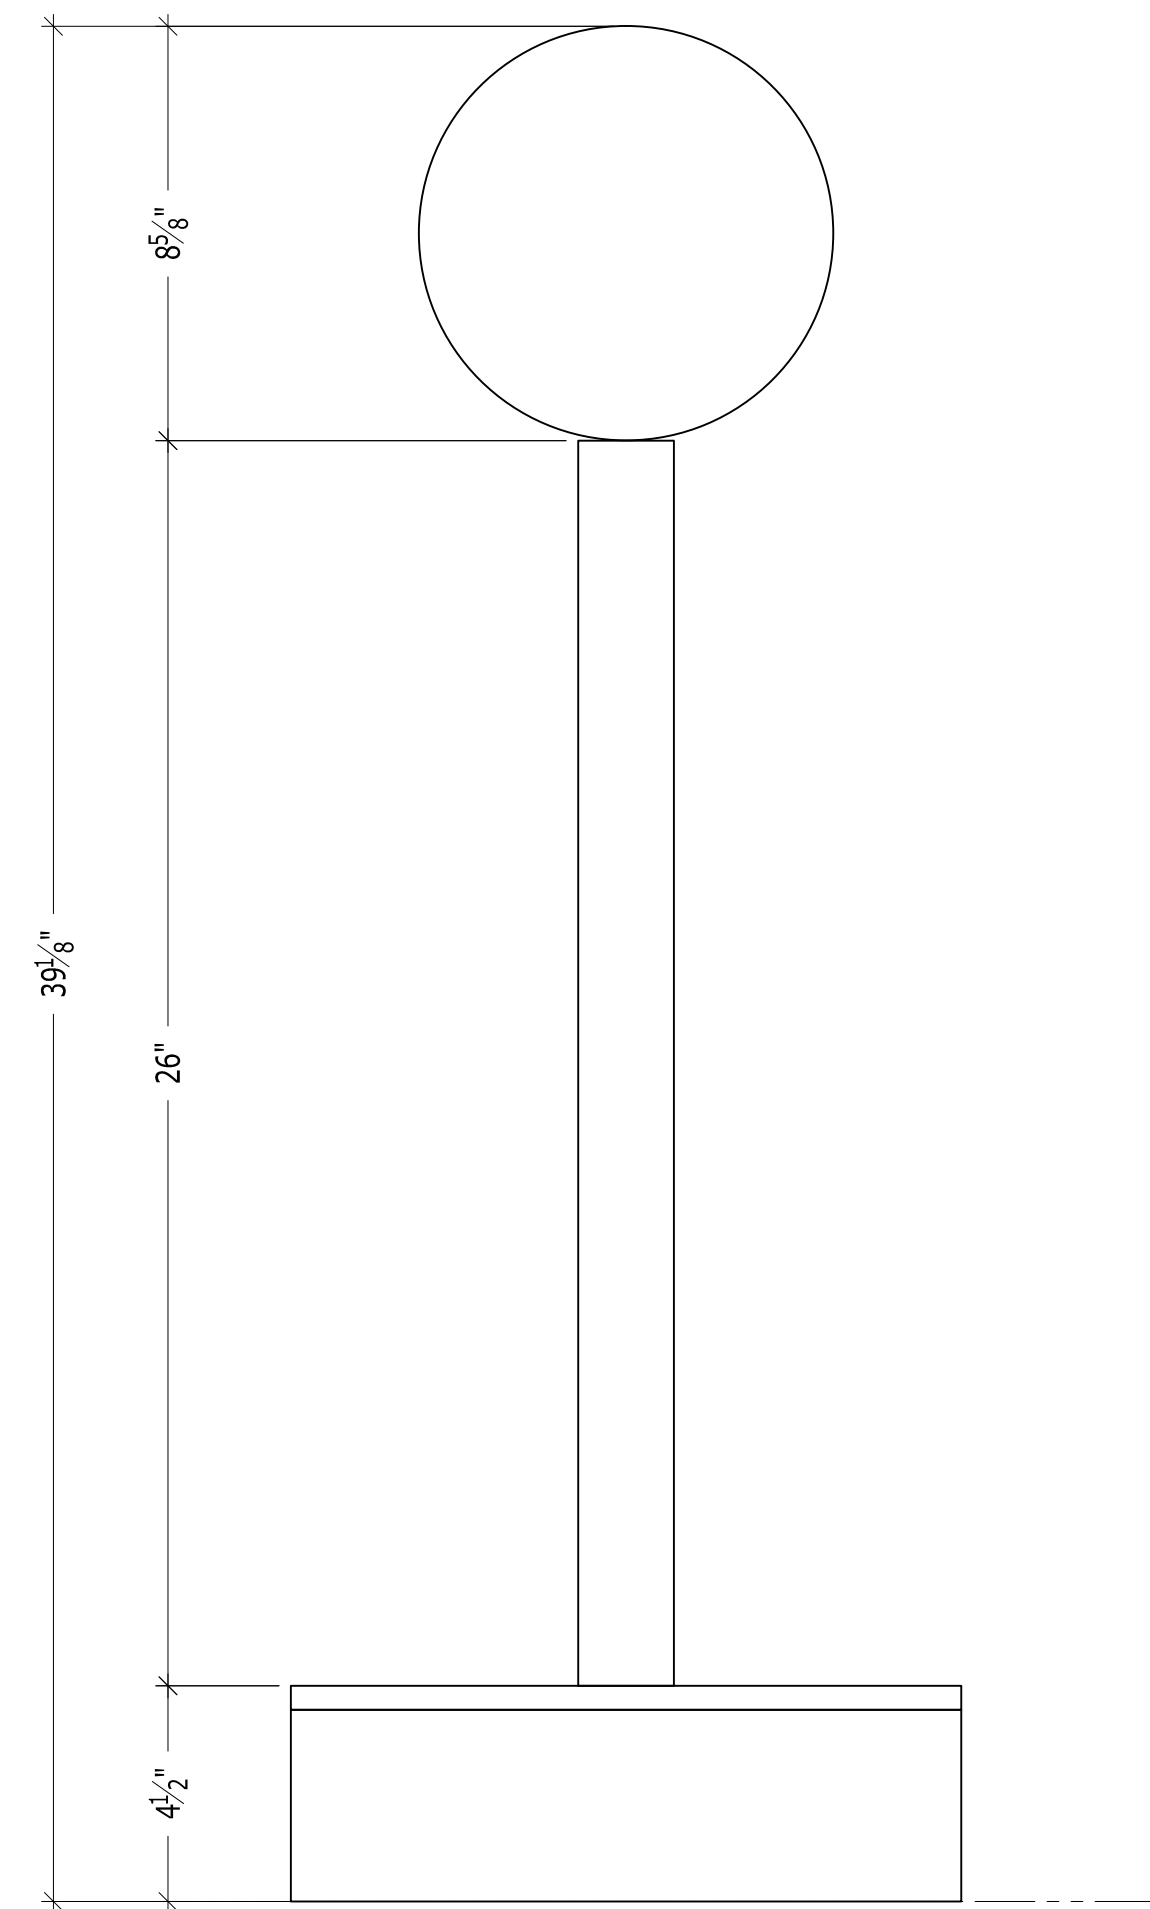

A ELEVATION -
SCALE: 3" = 1'-0"







FOR REVIEW

JACK ANDERSON
FABRICATION DESIGN
3326 CAZADOR STREET
LOS ANGELES CA 90065
623-419-4802
jack4congrss@protonmail.com

LOS ANGELES SOLAR SYSTEM PROJECT
FREE STANDING VENUS
2800 E. Observatory Rd
Los Angeles, CA 90027

DRAWN BY	JACK
DRAWING DATE	2-5-2026
REVISION DATE	--/------
TITLE	ELEVATION, SECTIONS
SCALE	AS NOTED
SHEET	VE200

JACK ANDERSON
FABRICATION DESIGN
3326 CAZADOR STREET
LOS ANGELES CA 90065
623-419-4802
jack4congrss@protonmail.com

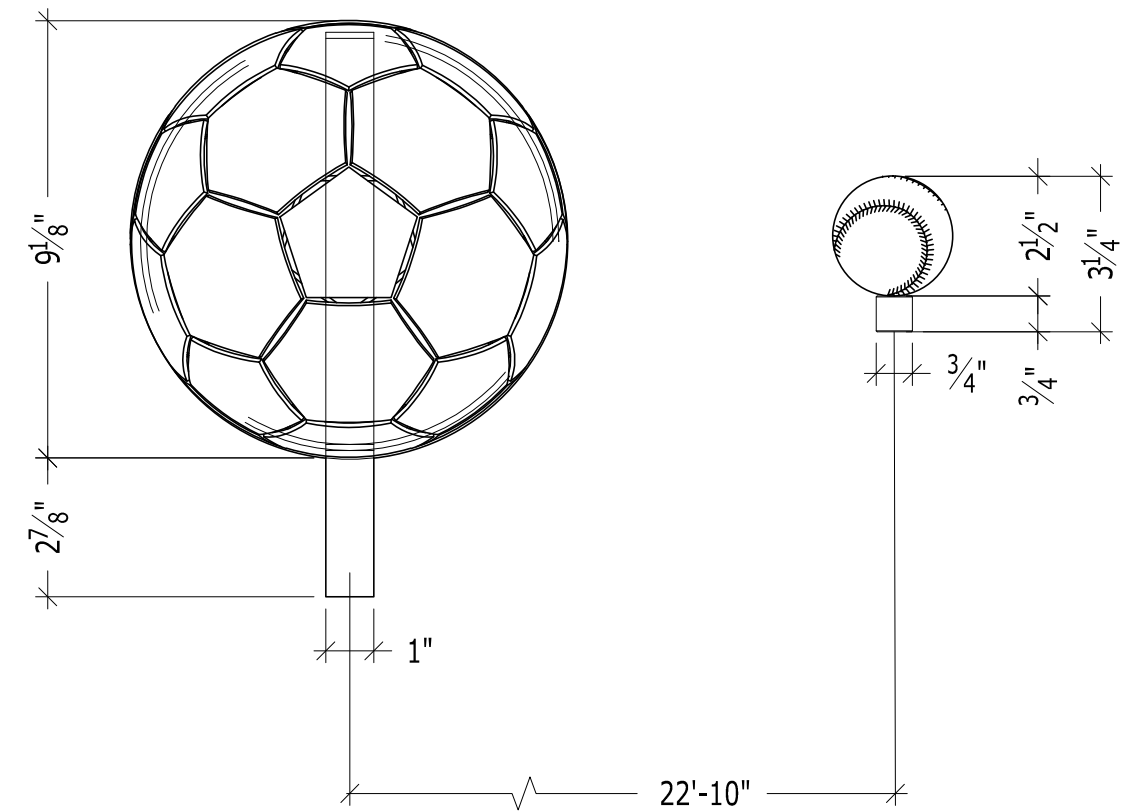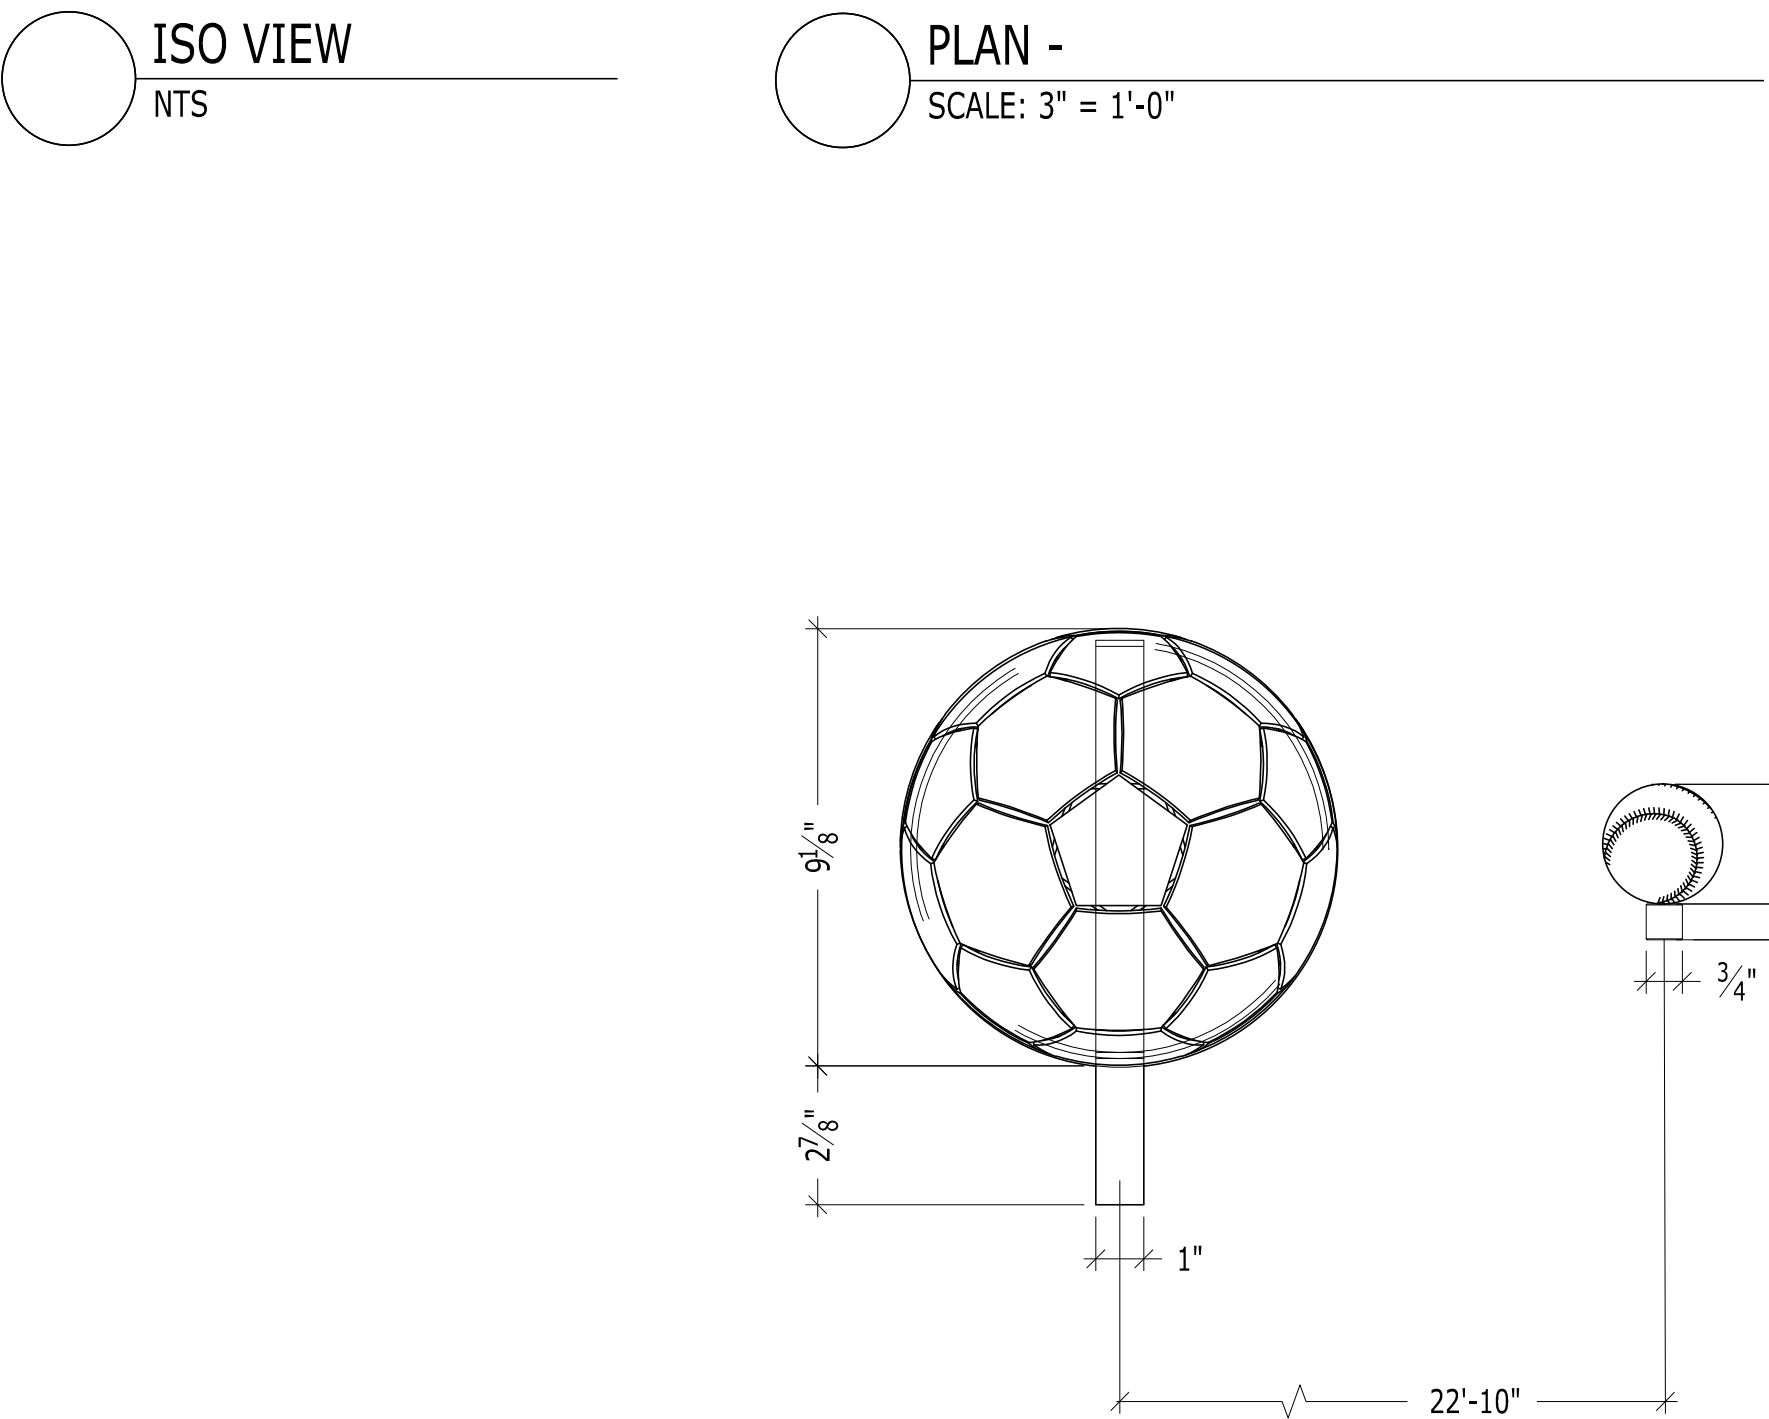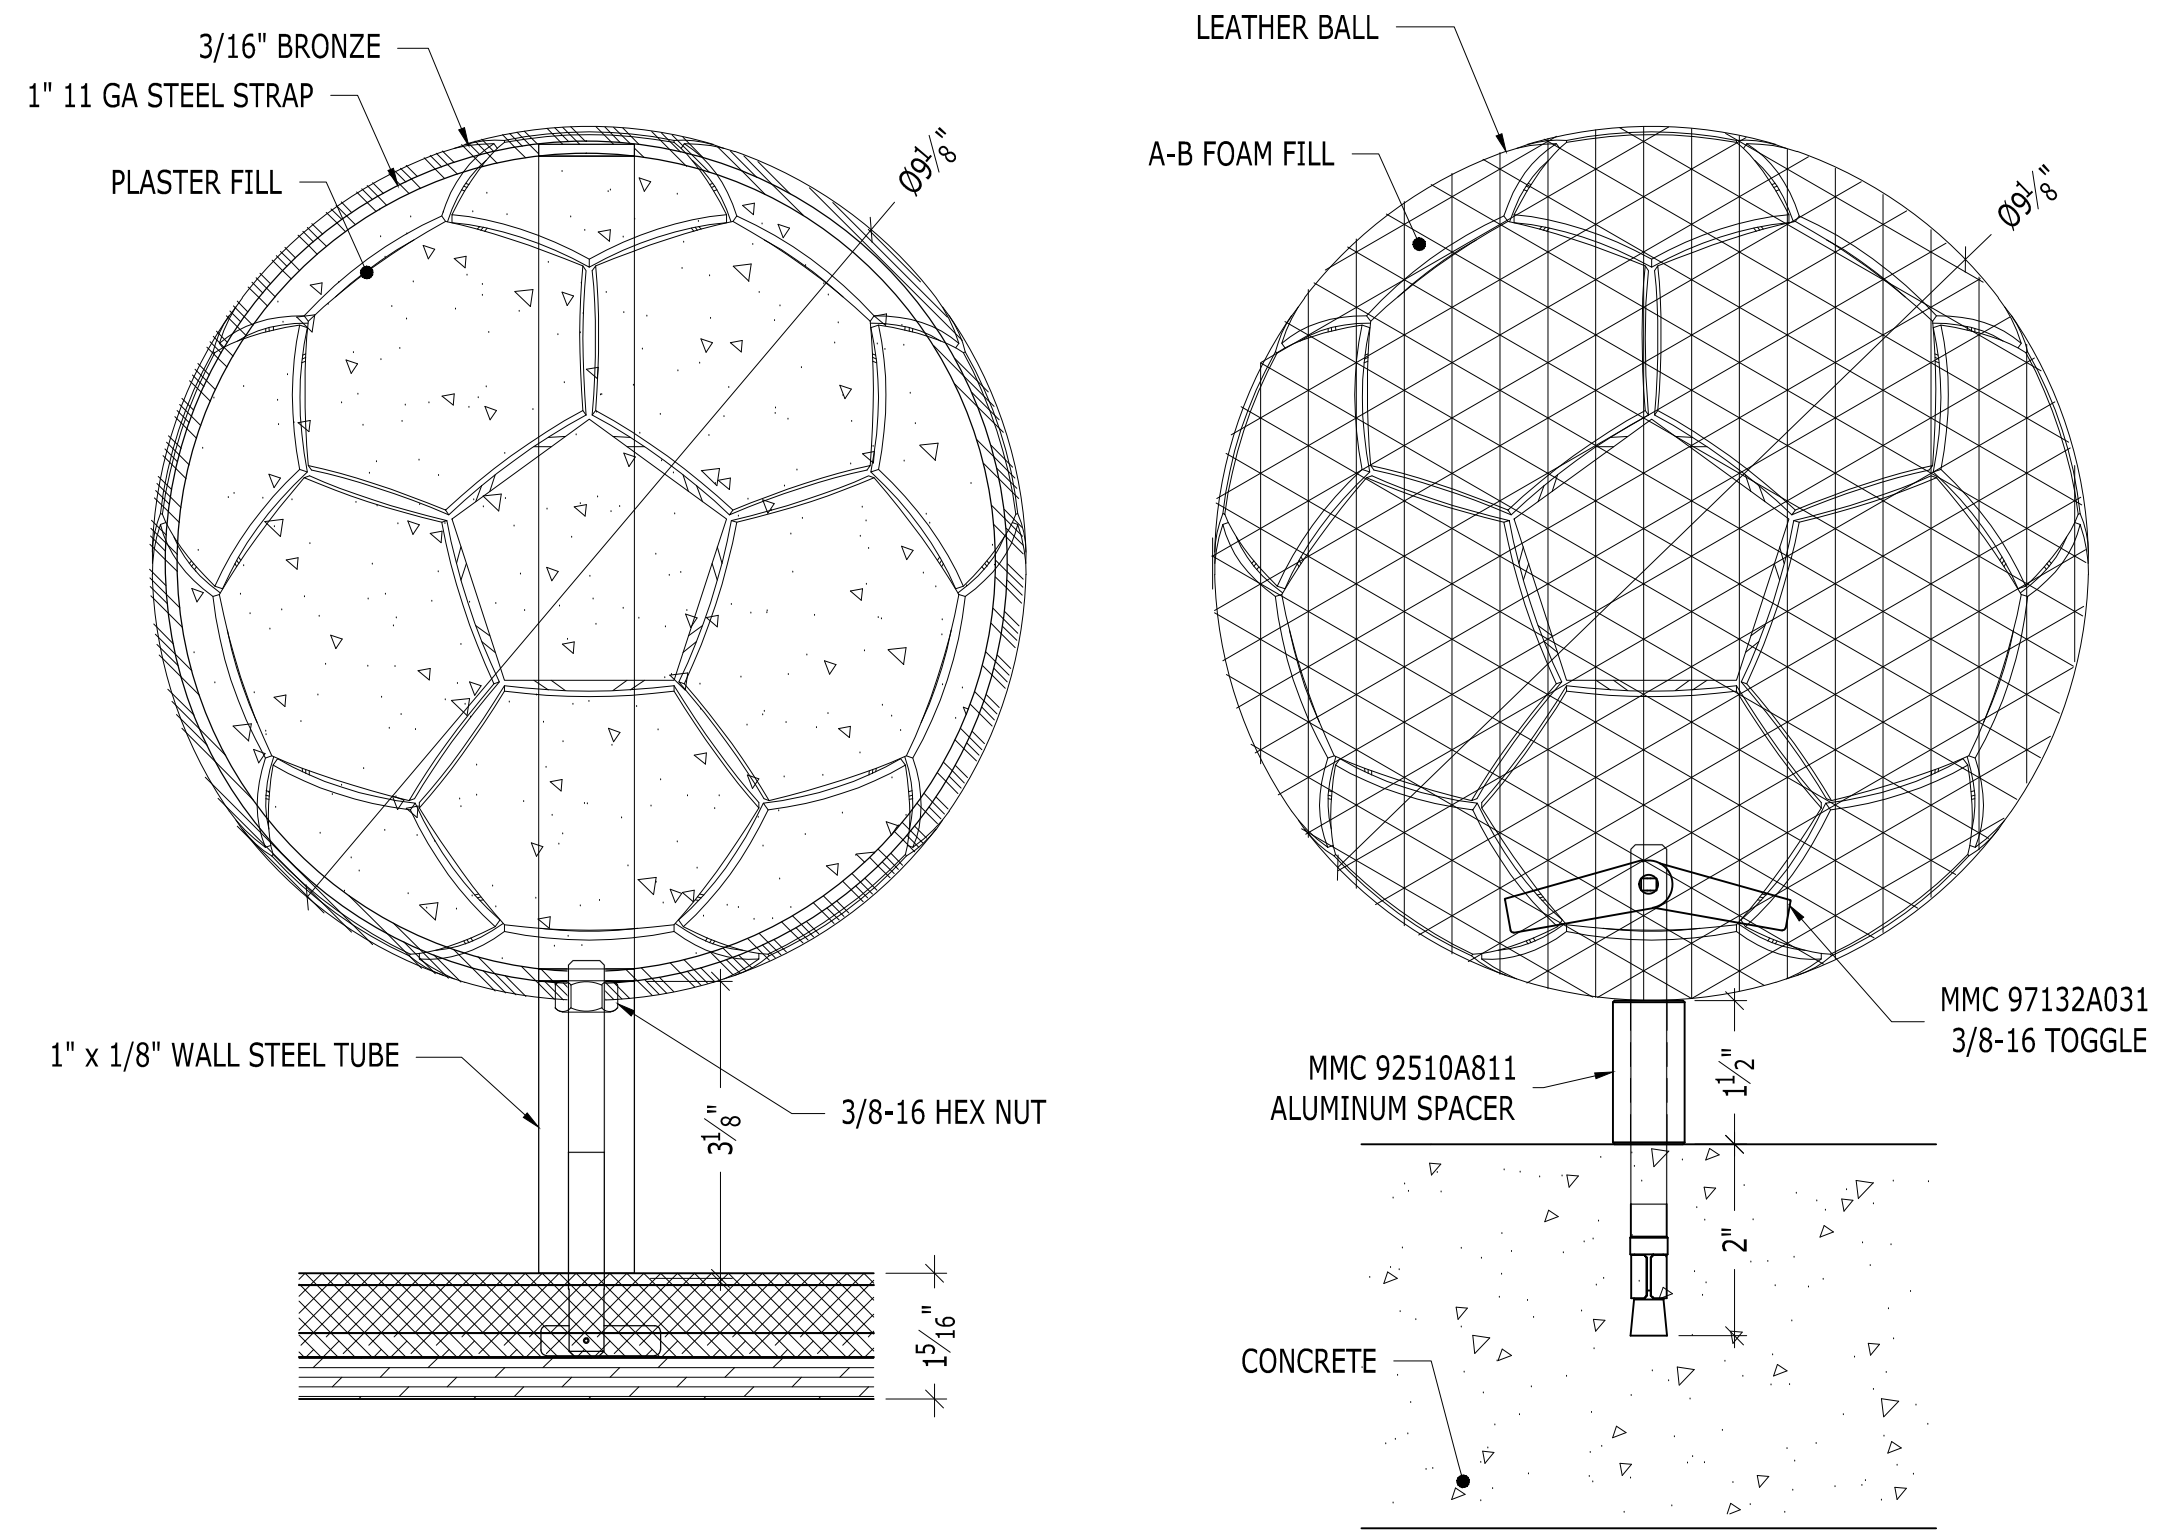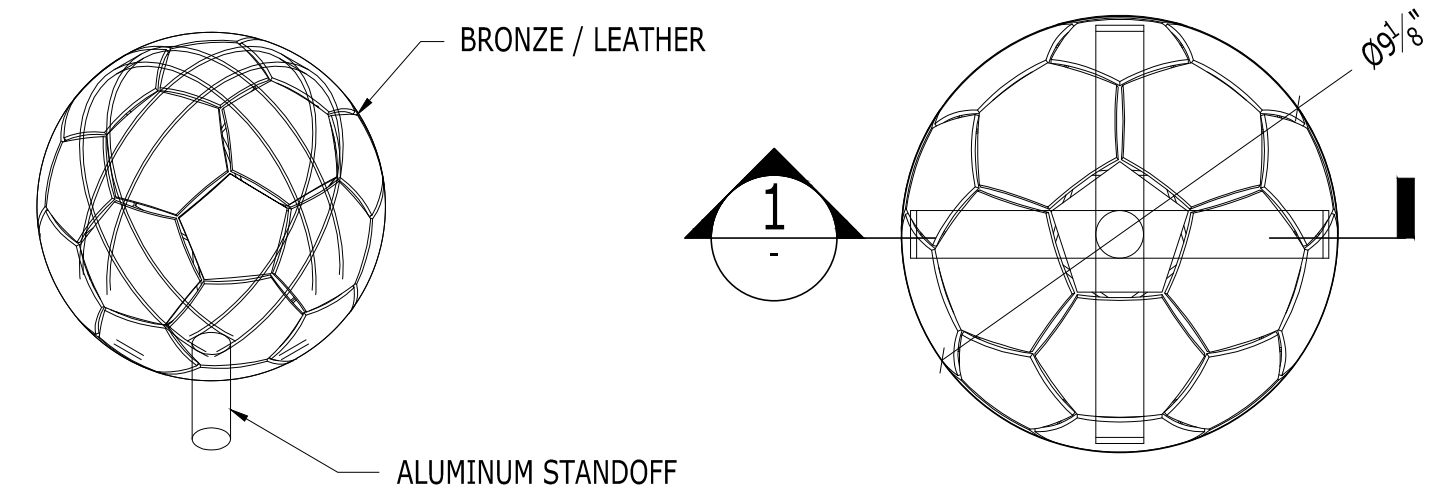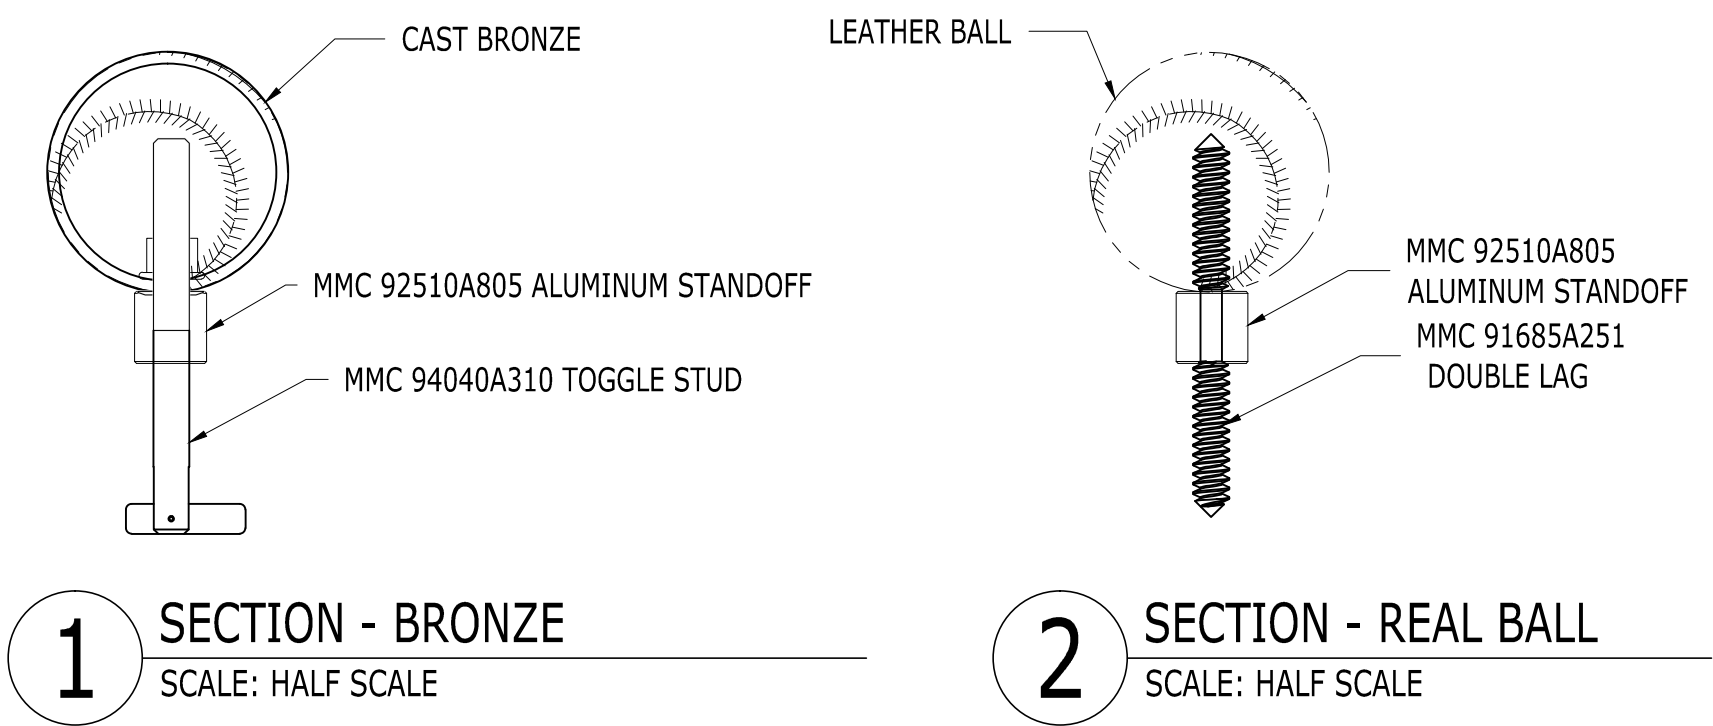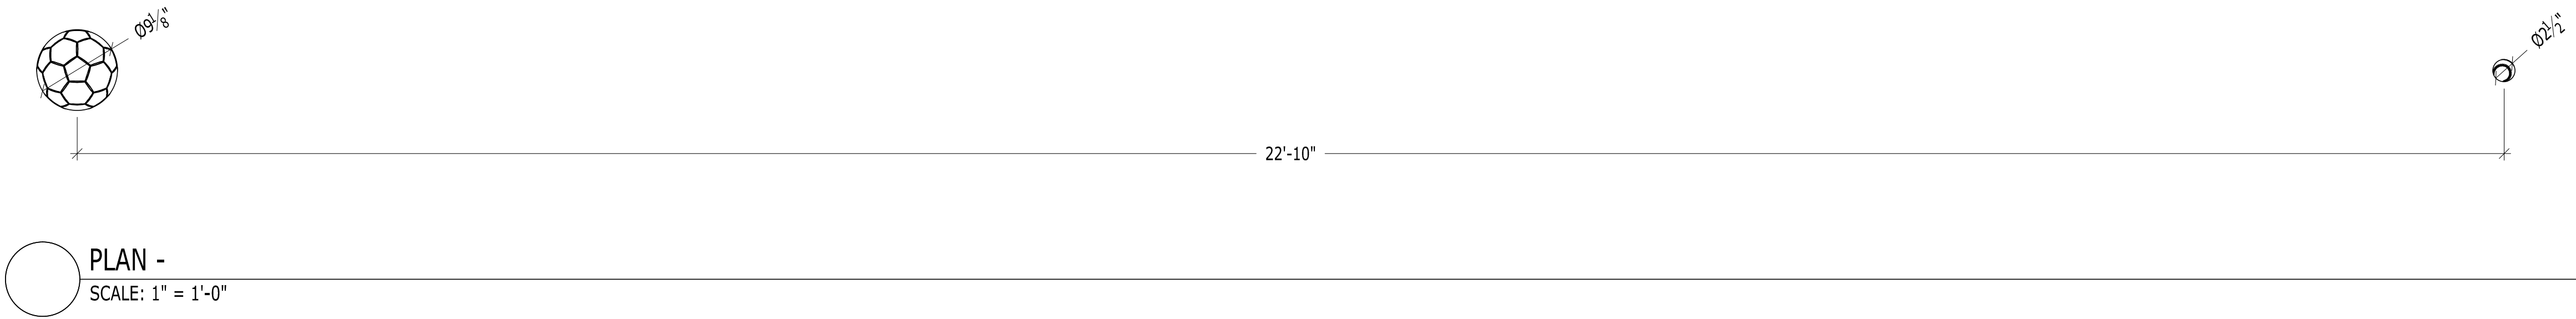

FOR REVIEW






LOS ANGELES SOLAR SYSTEM PROJECT

2800 E. Observatory Rd
Los Angeles, CA 90027


EARTH AND MOON

DRAWN BY	JACK
DRAWING DATE	2-5-2026
REVISION DATE	--/------
TITLE	ELEVATION, SECTIONS
SCALE	AS NOTED
SHEET	EA300


JACK ANDERSON
FABRICATION DESIGN
3326 CAZADOR STREET
LOS ANGELES CA 90065
623-419-4802
jack4congrss@protonmail.com

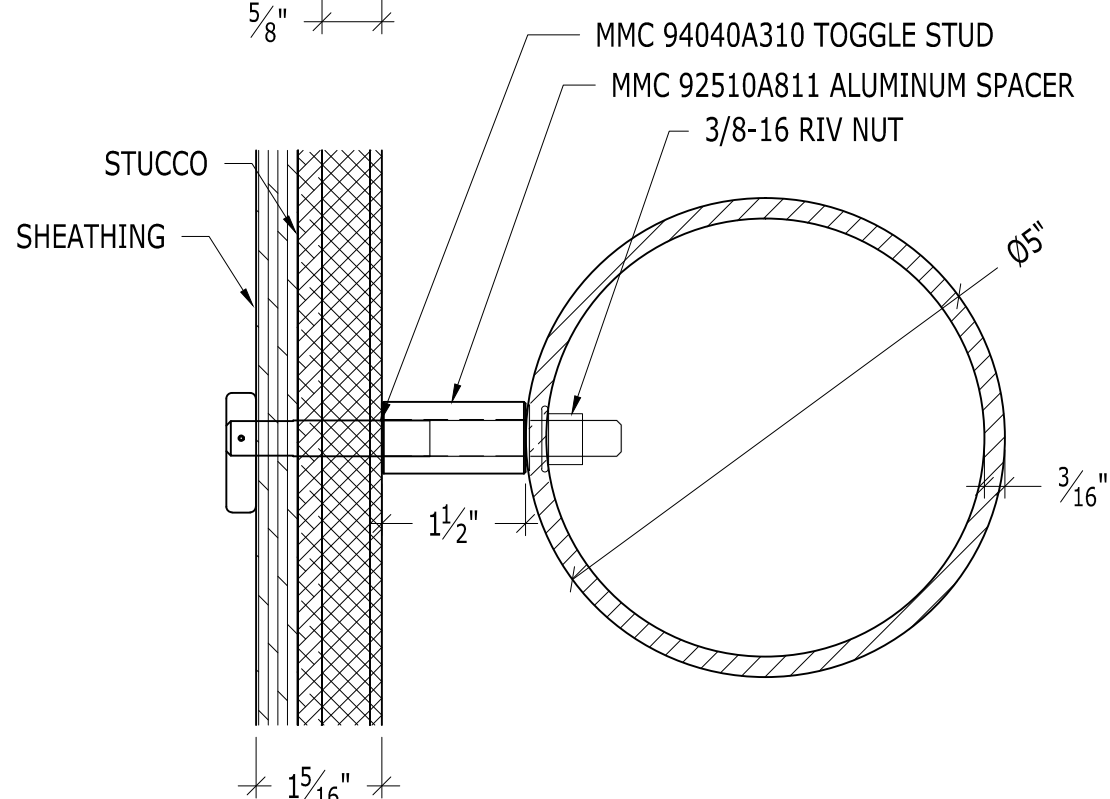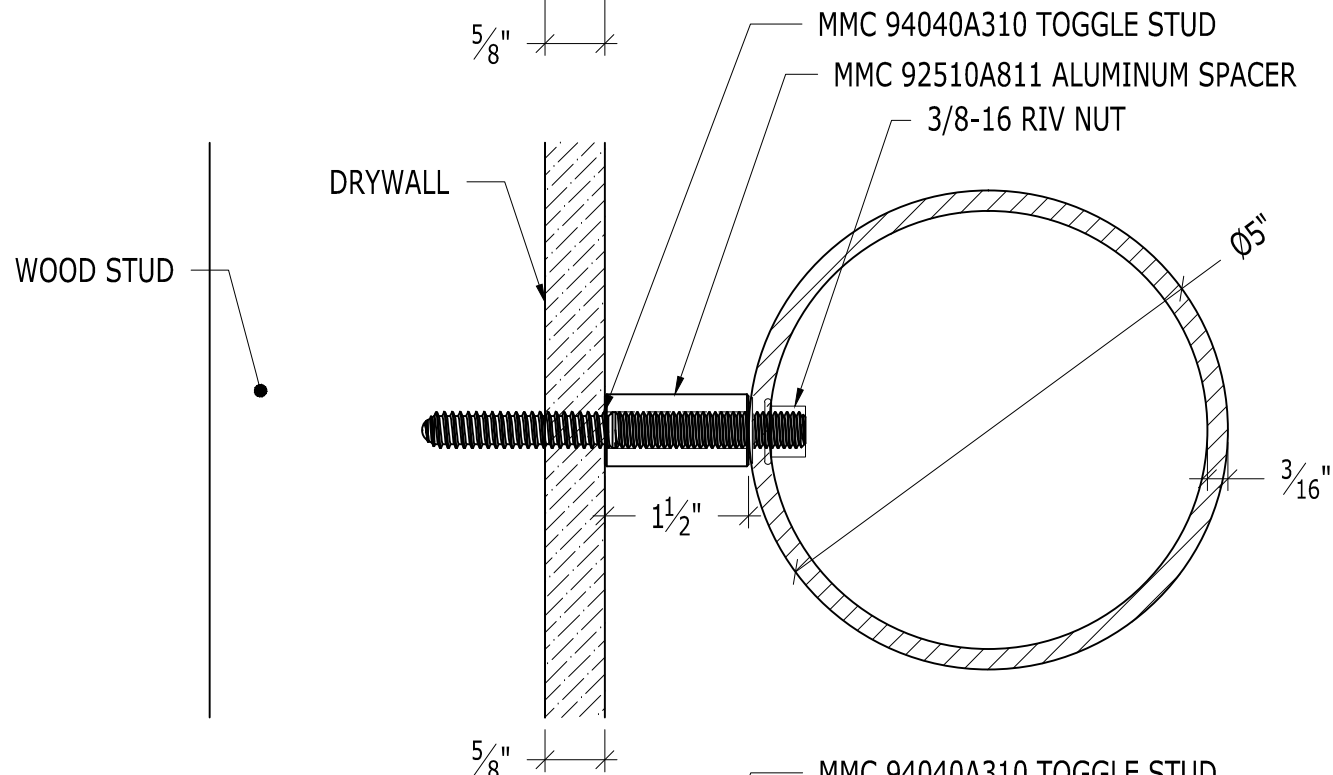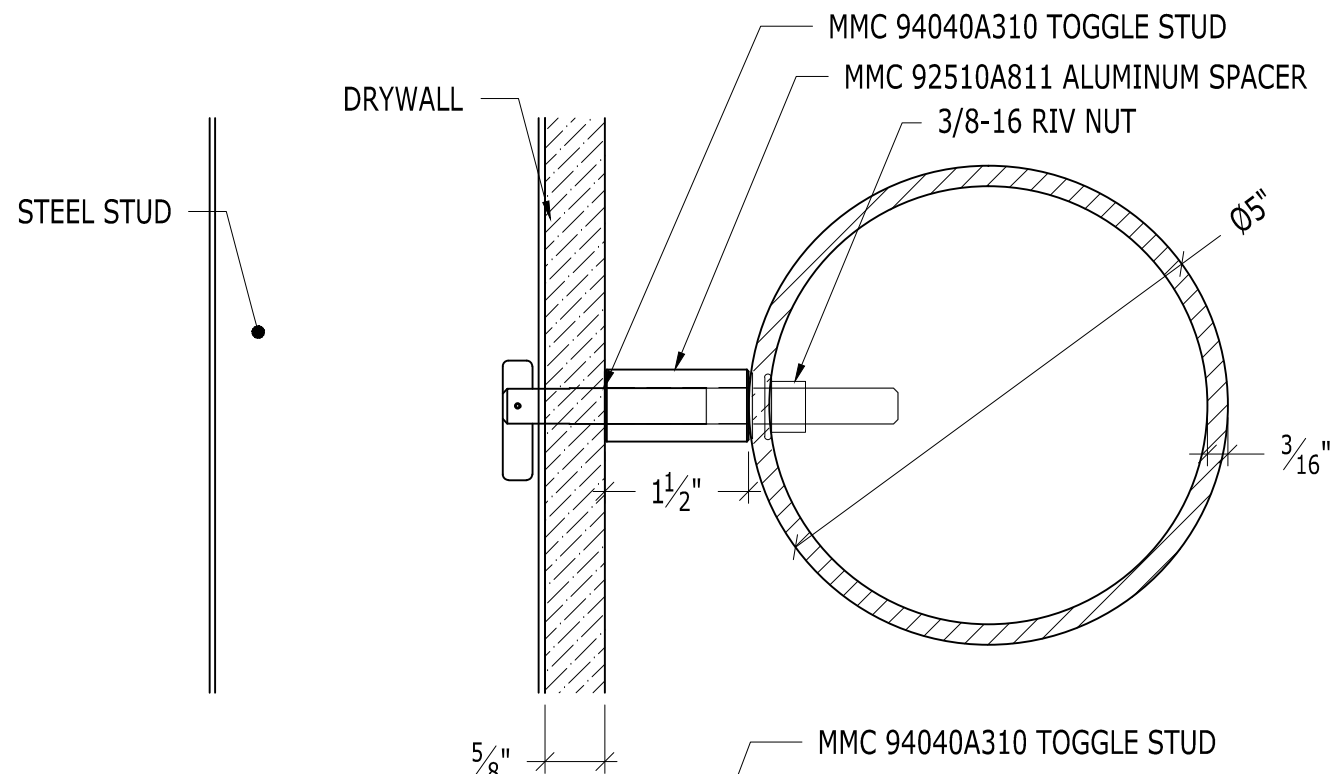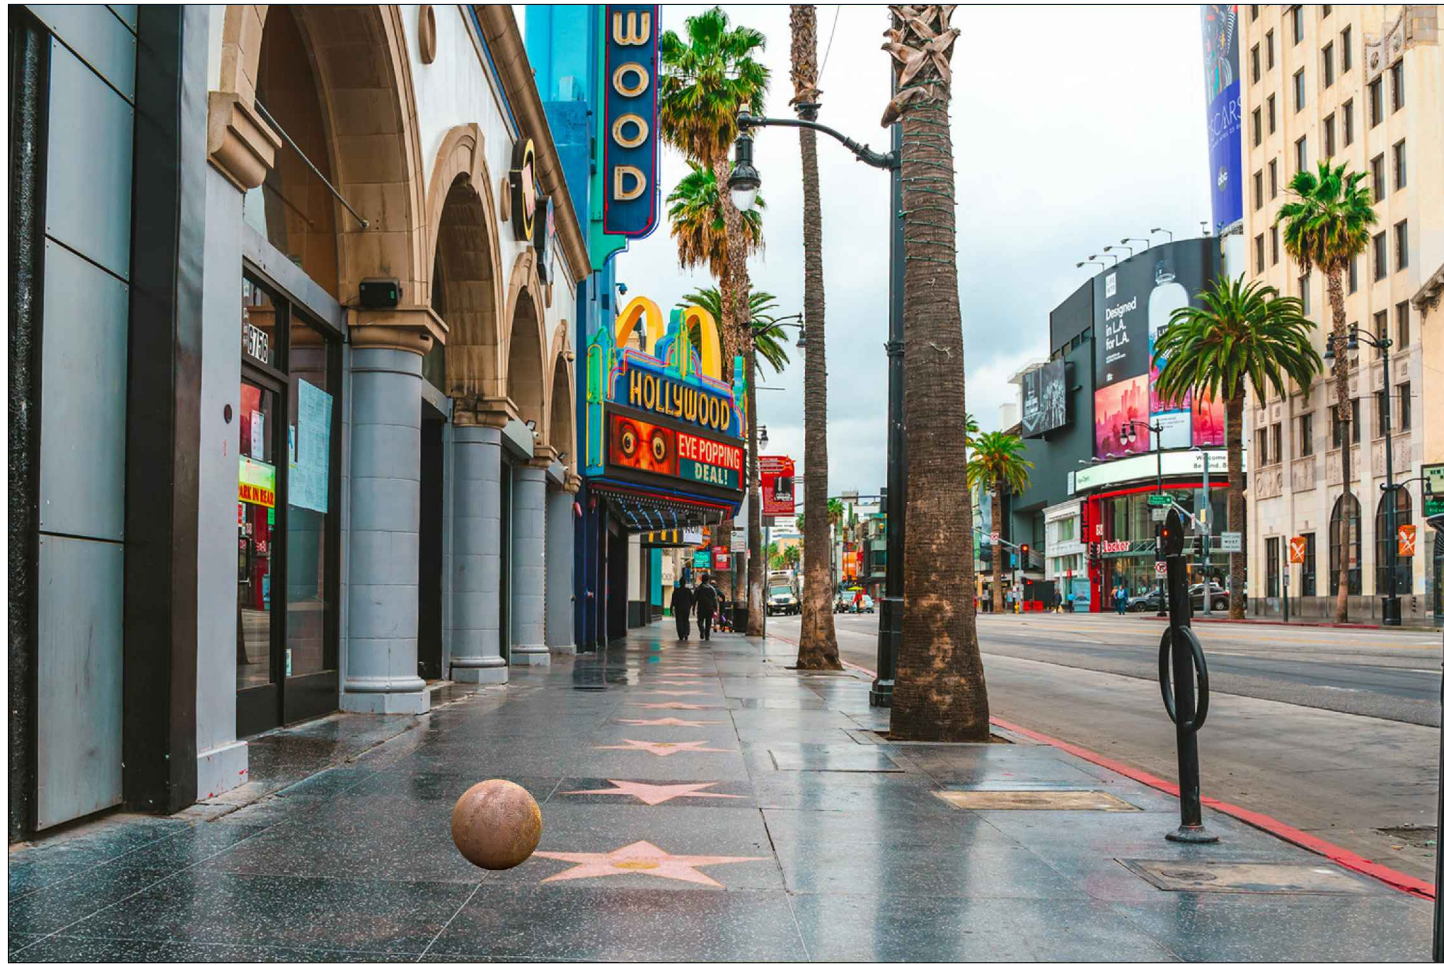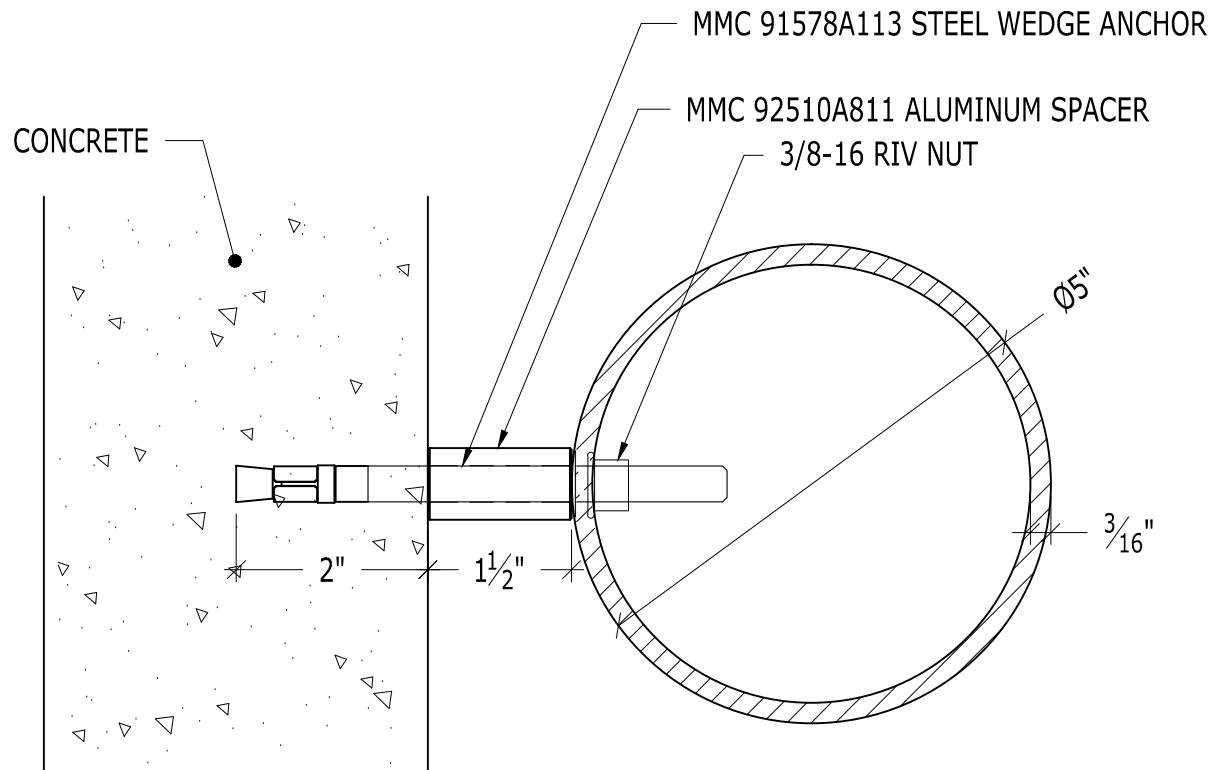


1 SECTION - INSTALLATION
SCALE: HALF SCALE

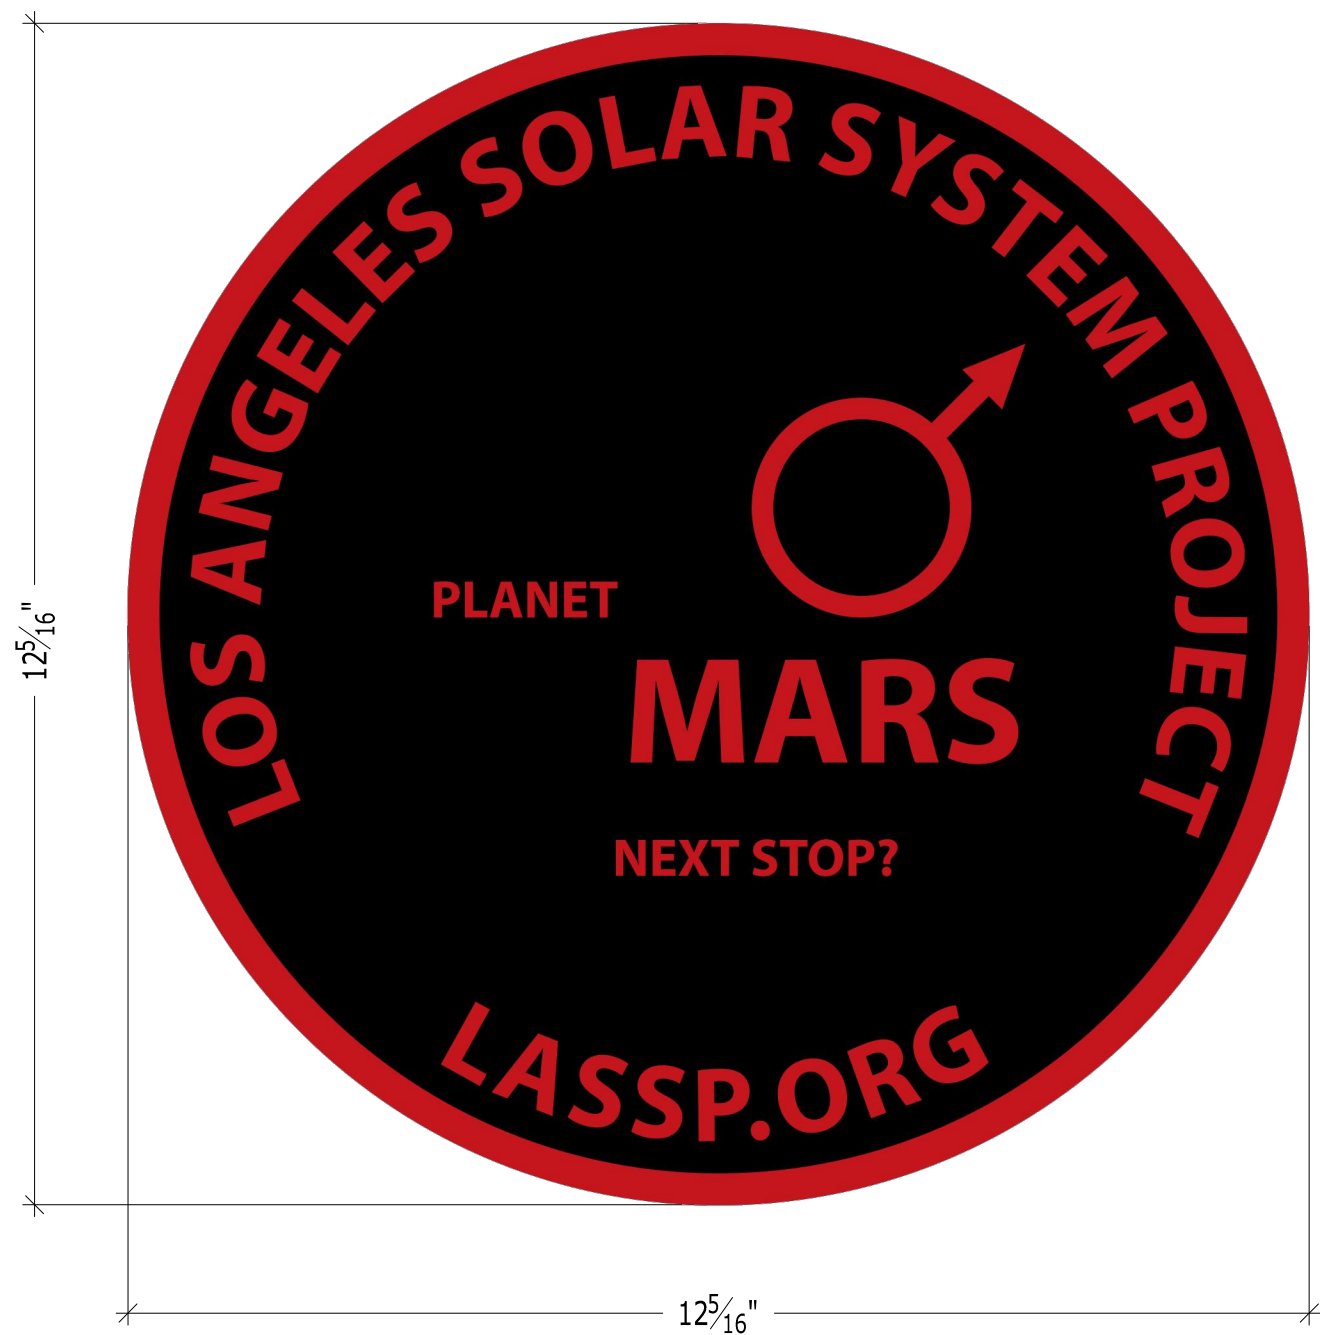


B ELEVATION - COMPANION GRAPHIC
SCALE: HALF SCALE

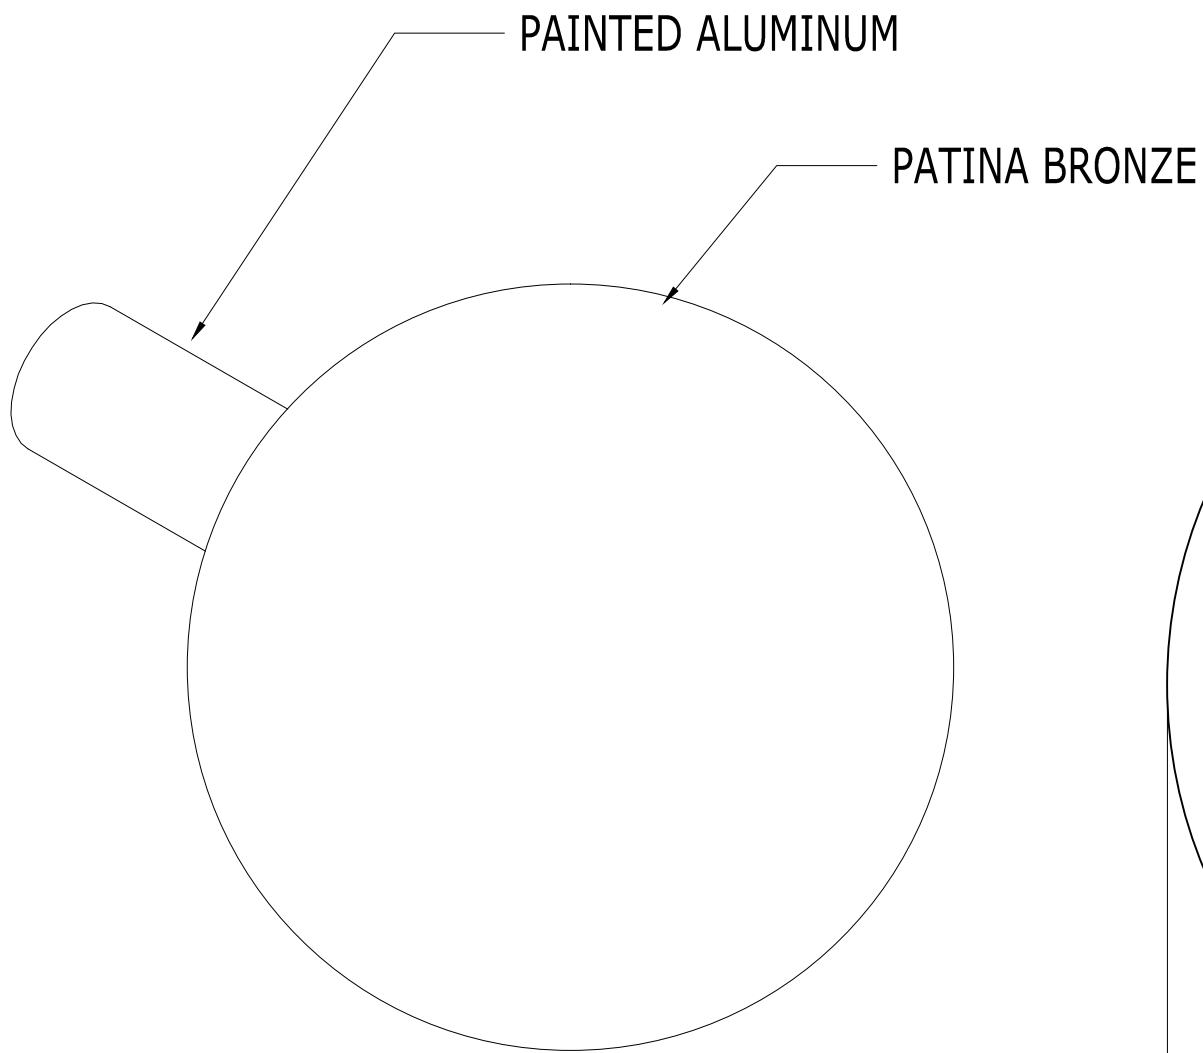

ISO VIEW
NTS

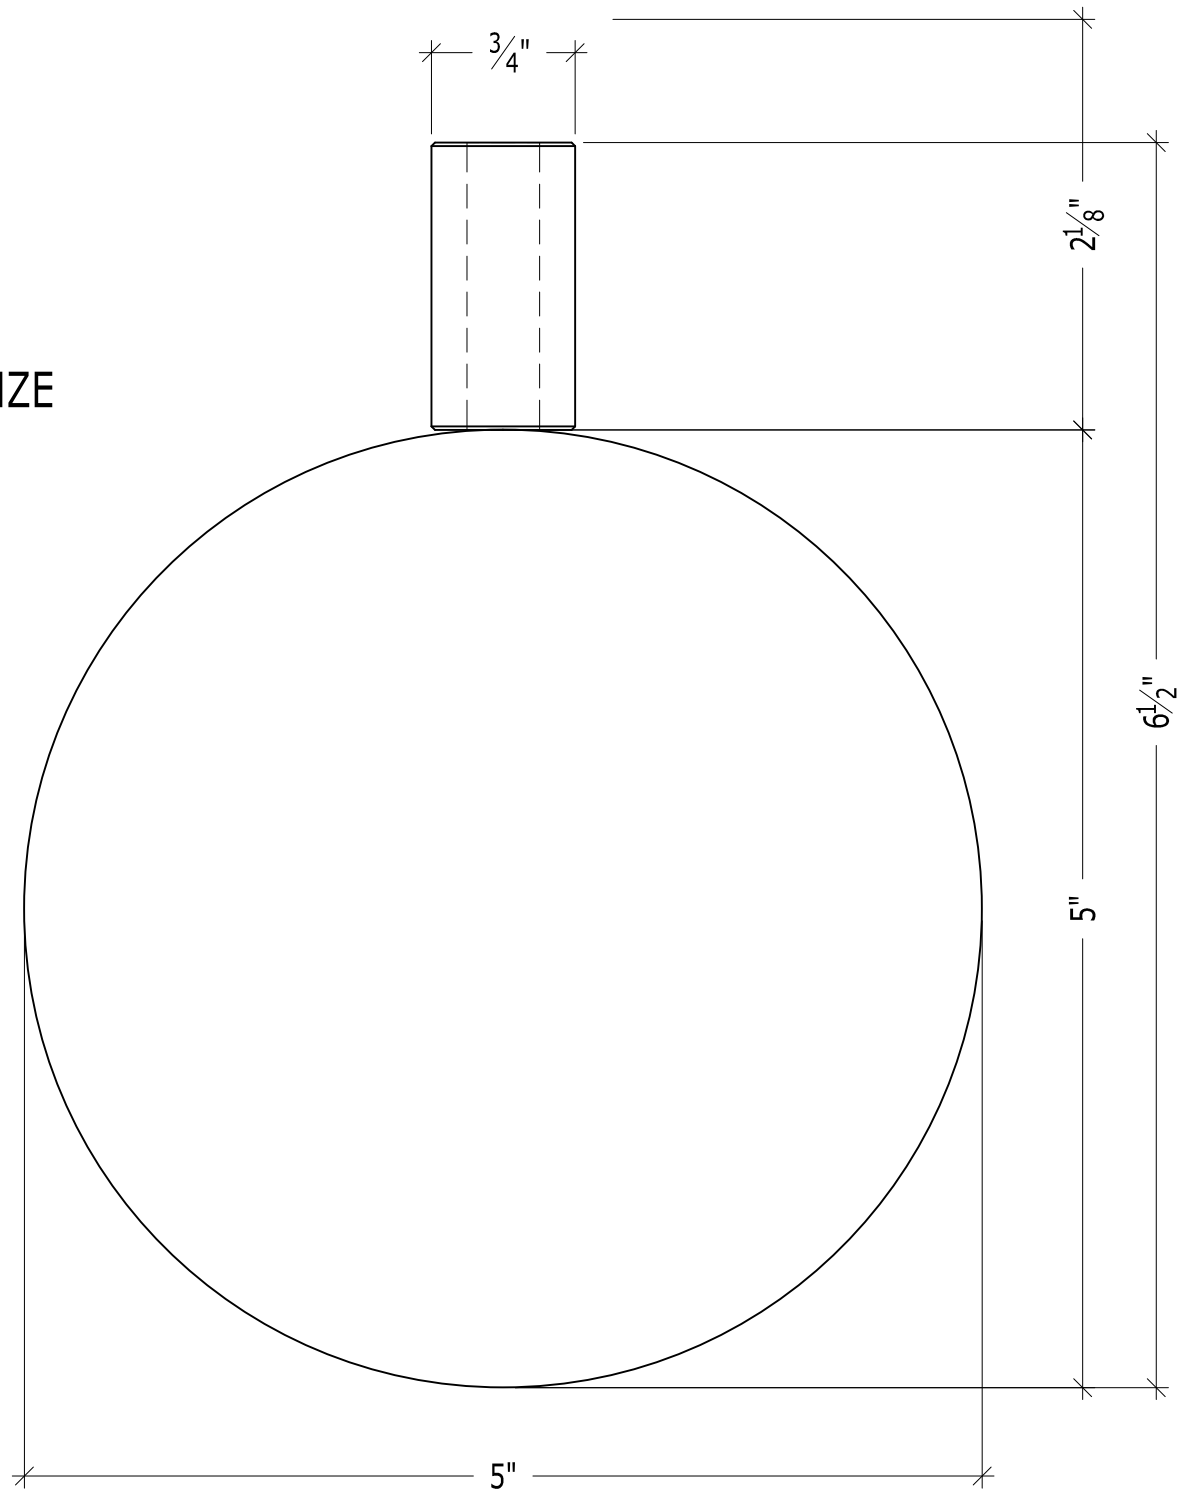

PLAN -
SCALE: FULL SCALE

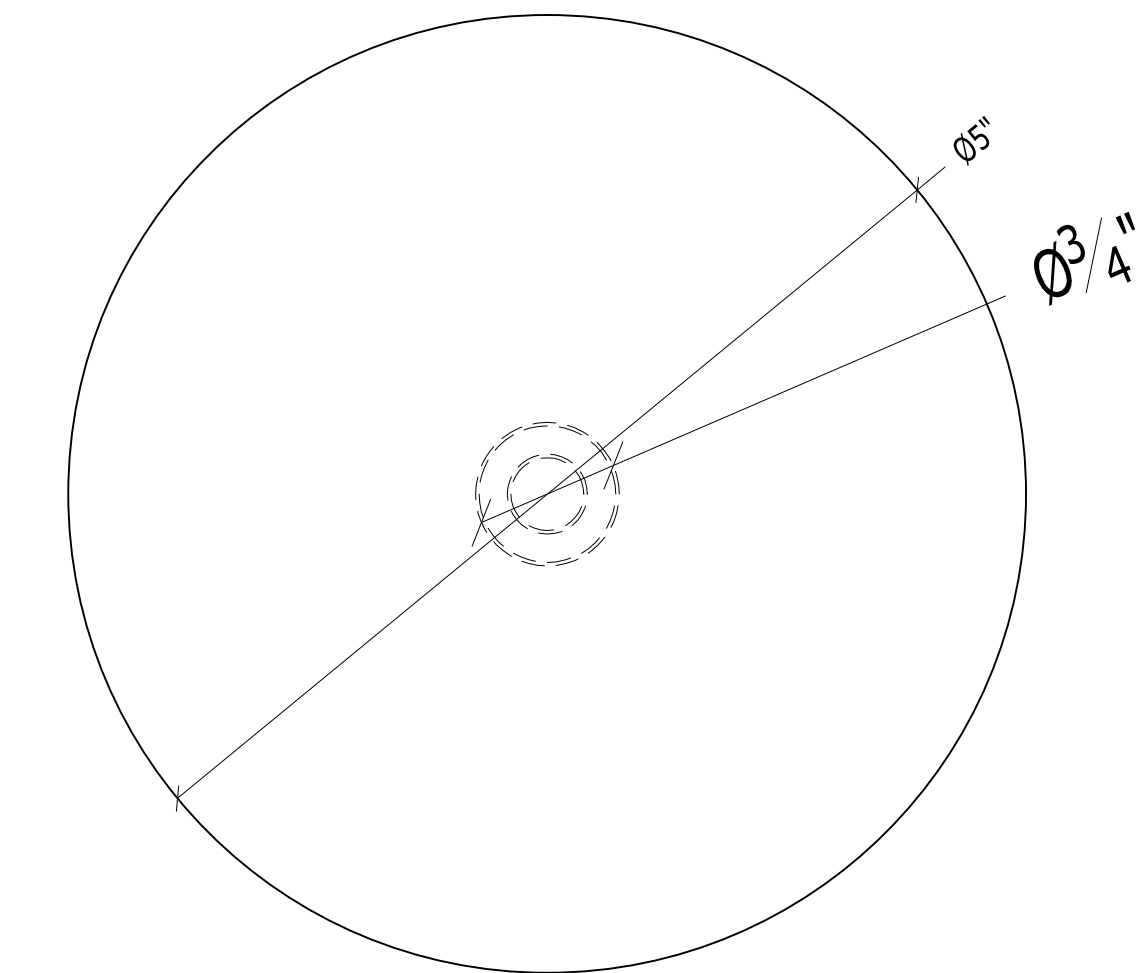

A ELEVATION -
SCALE: FULL SCALE

FOR REVIEW



LOS ANGELES SOLAR SYSTEM PROJECT
WALL MOUNT MARS

2800 E. Observatory Rd
Los Angeles, CA 90027

DRAWN BY	JACK
DRAWING DATE	2-5-2026
REVISION DATE	--/--/----
TITLE	ELEVATION, SECTIONS
SCALE	AS NOTED
SHEET	MA400

CICLAVIA LIGHT SPEED RIDE MOUNT
LOCATION: NORMANDIE & WILSHIRE

JACK ANDERSON
FABRICATION DESIGN
3326 CAZADOR STREET
LOS ANGELES CA 90065
623-419-4802
jack4congrss@protonmail.com

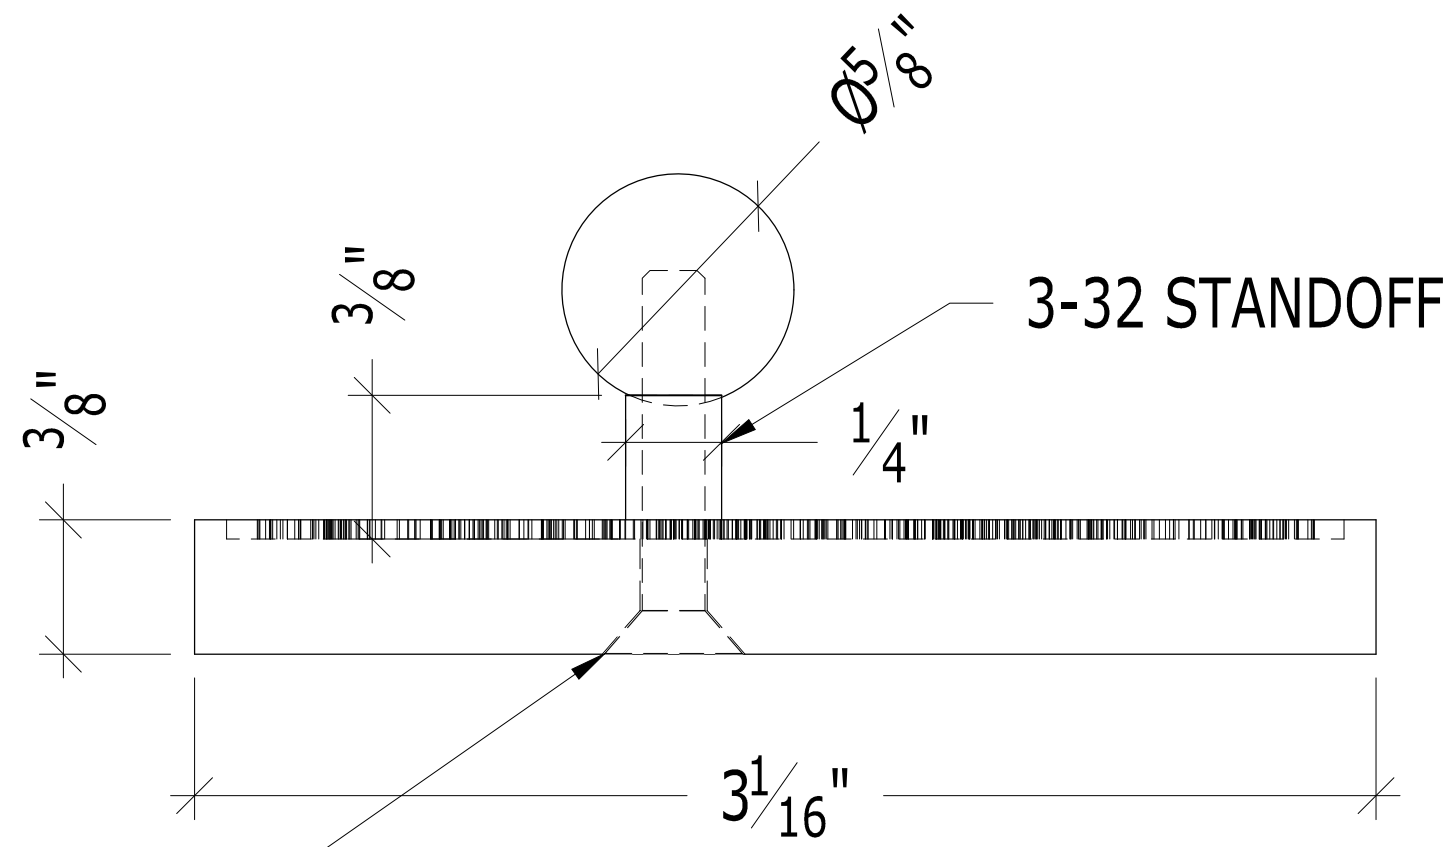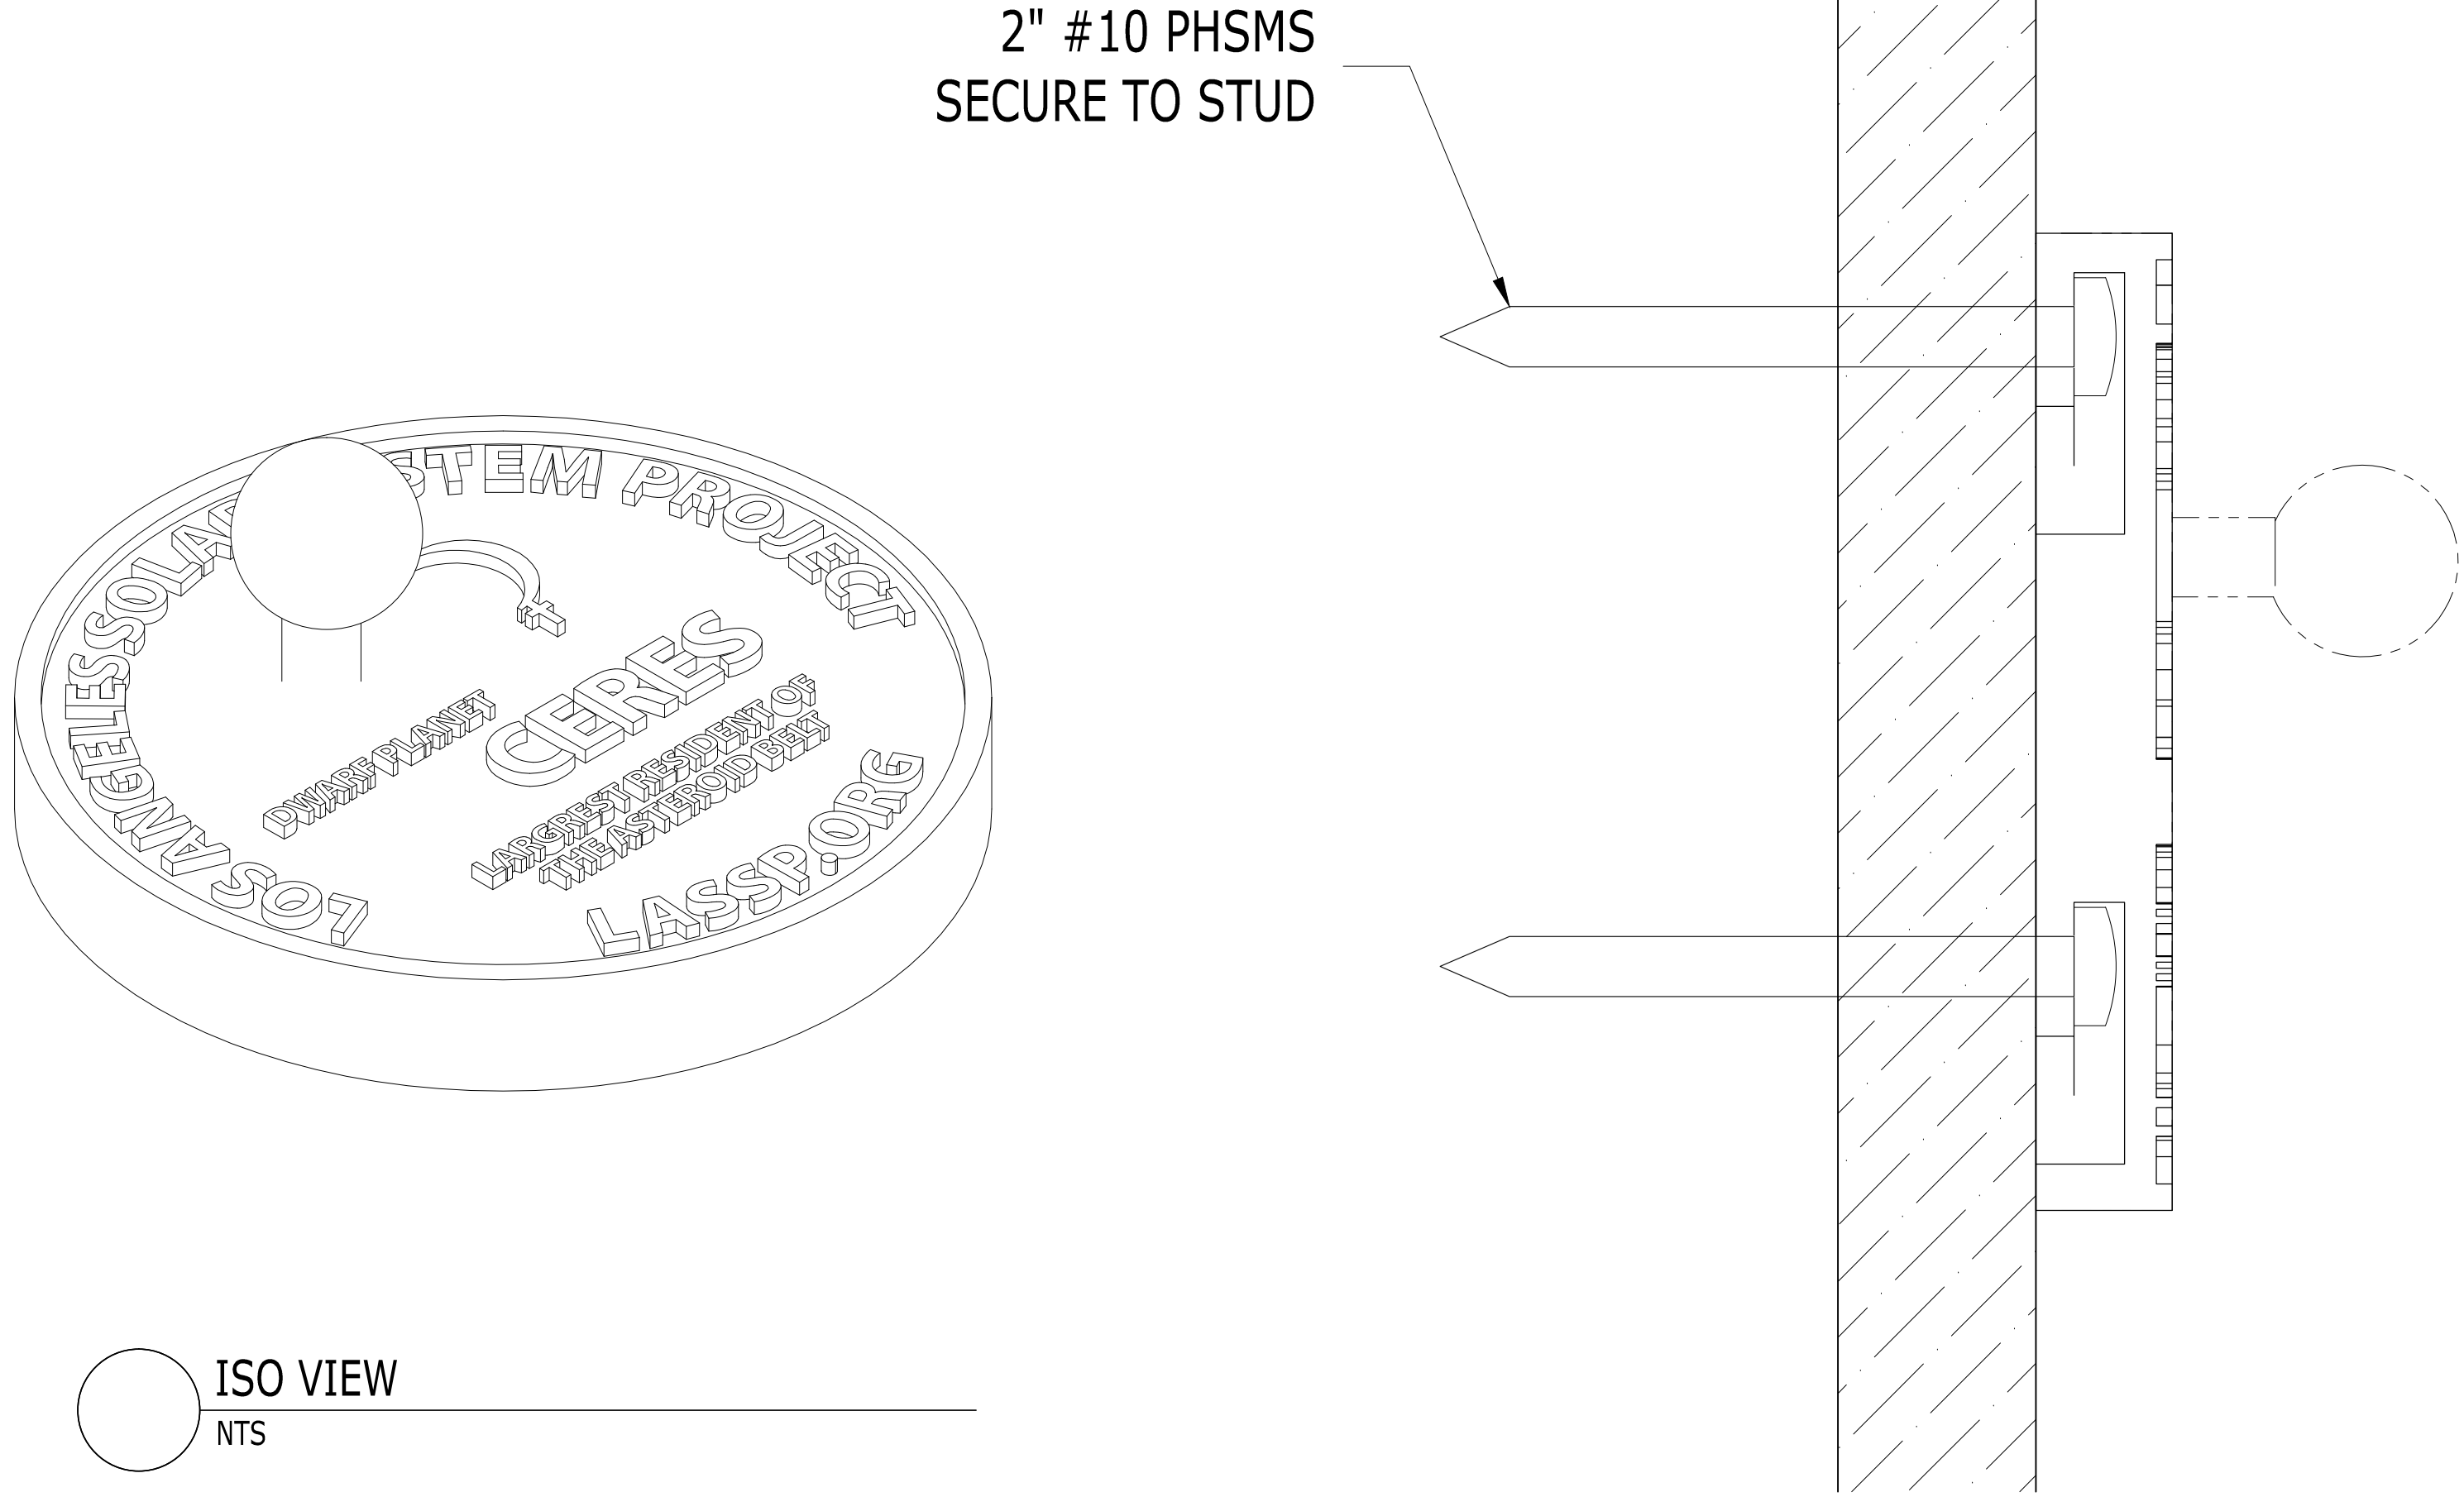

LOS ANGELES SOLAR SYSTEM PROJECT

2800 E. Observatory Rd
Los Angeles, CA 90027

WALL MOUNT DWARF PLANET / ASTEROID

DRAWN BY
JACK


DRAWING DATE
2-5-2026

REVISION DATE
--/--/----


TITLE
ELEVATION, SECTIONS

SCALE
AS NOTED


SHEET
CE500

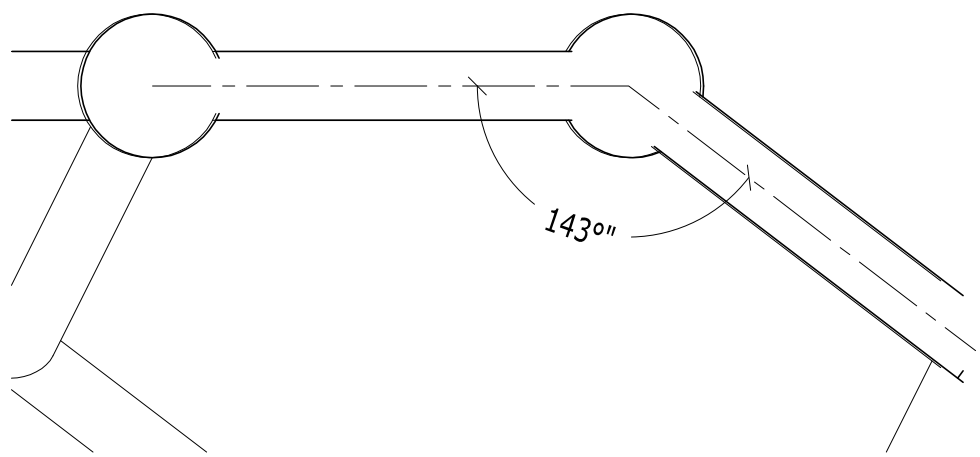


3 DETAIL -HEXAGON TO PENTAGON
SCALE: 1-1/2" = 1'-0"

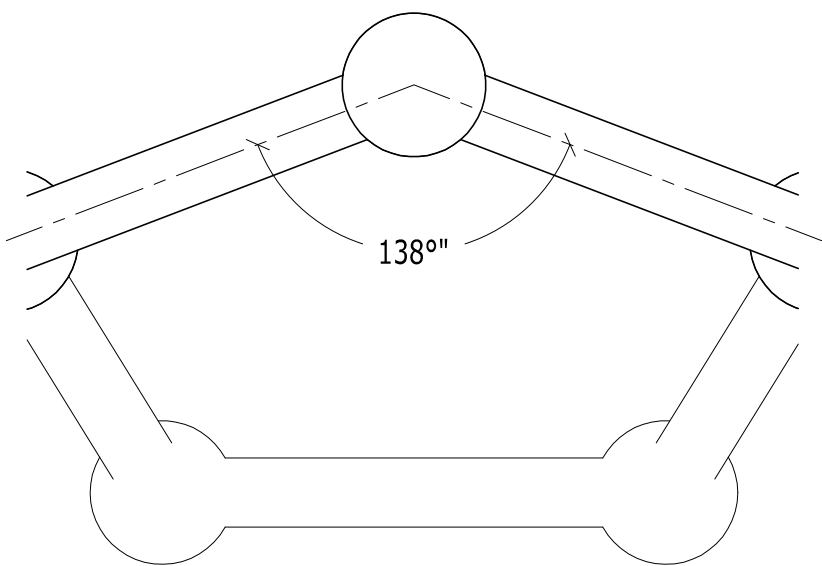


2 DETAIL - HEXAGON TO HEXAGON
SCALE: 1-1/2" = 1'-0"

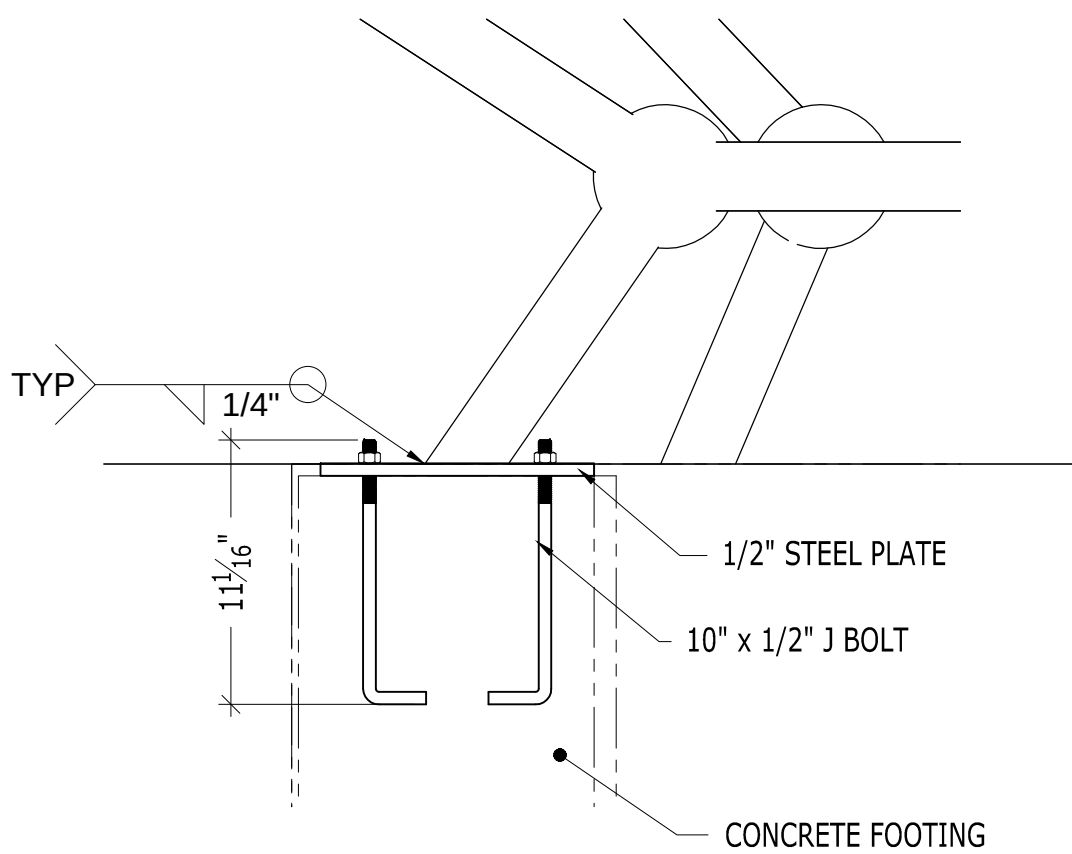


1 DETAIL - FOOTING
SCALE: 1-1/2" = 1'-0"

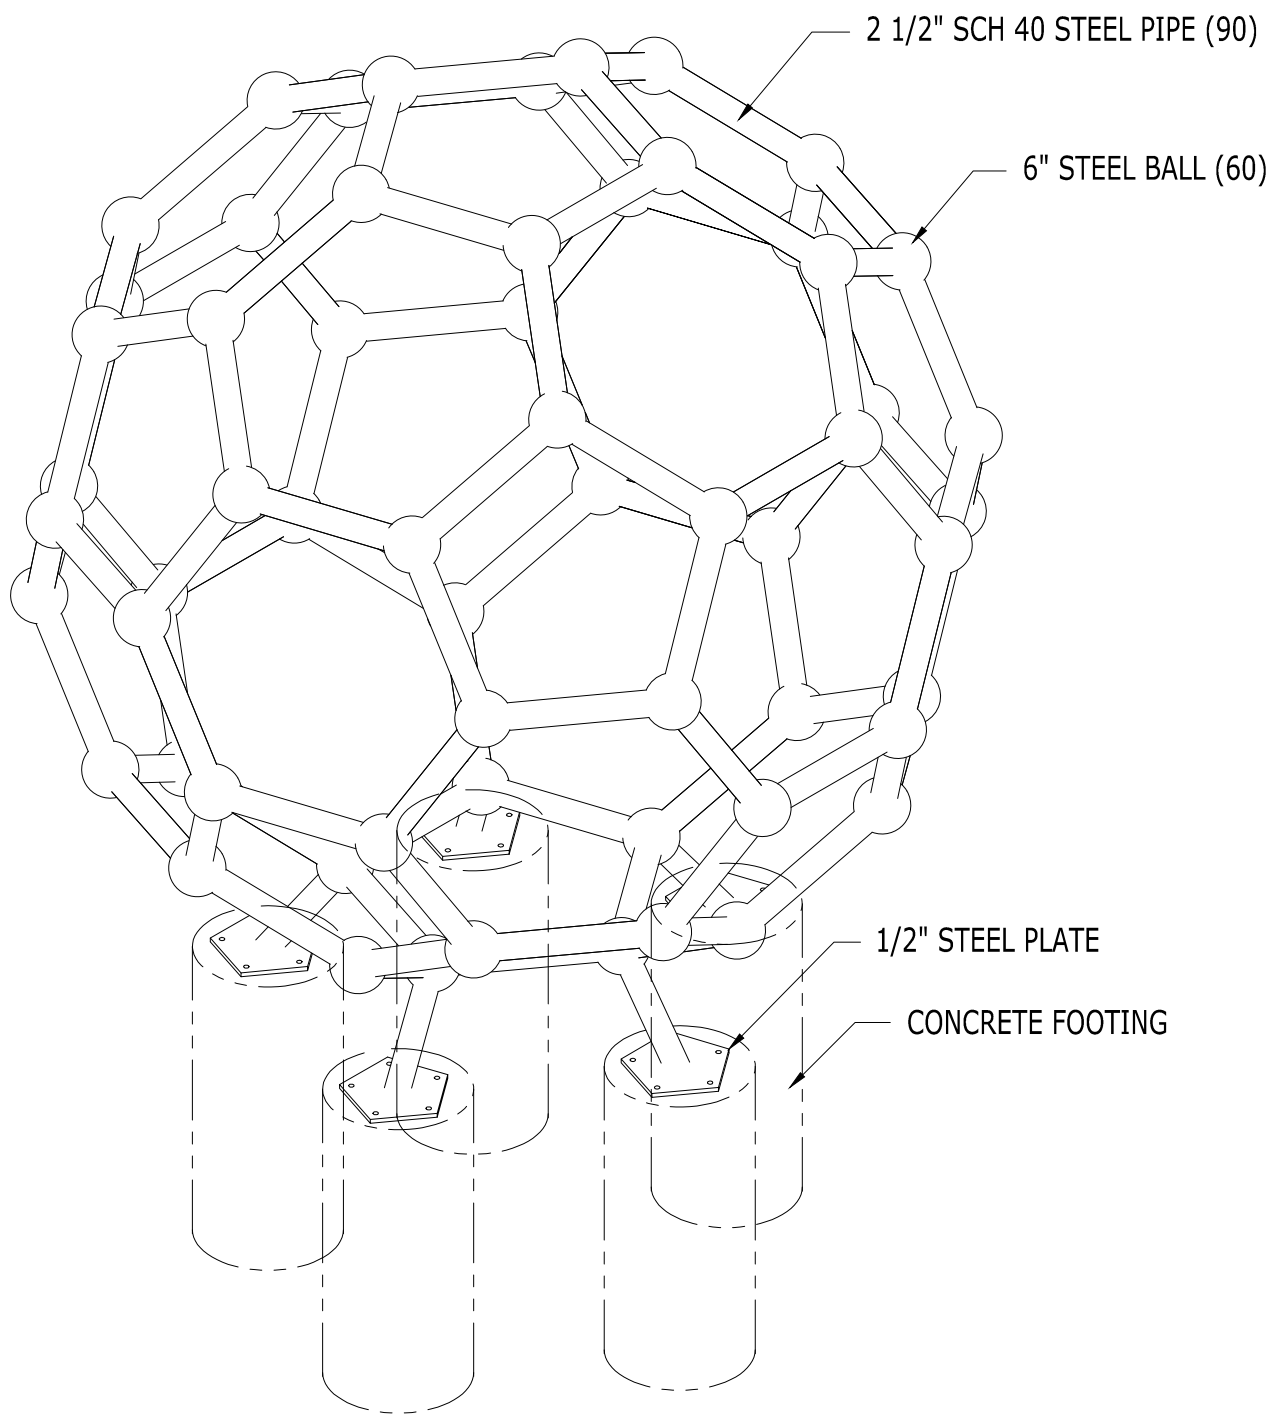


ISO VIEW
NTS

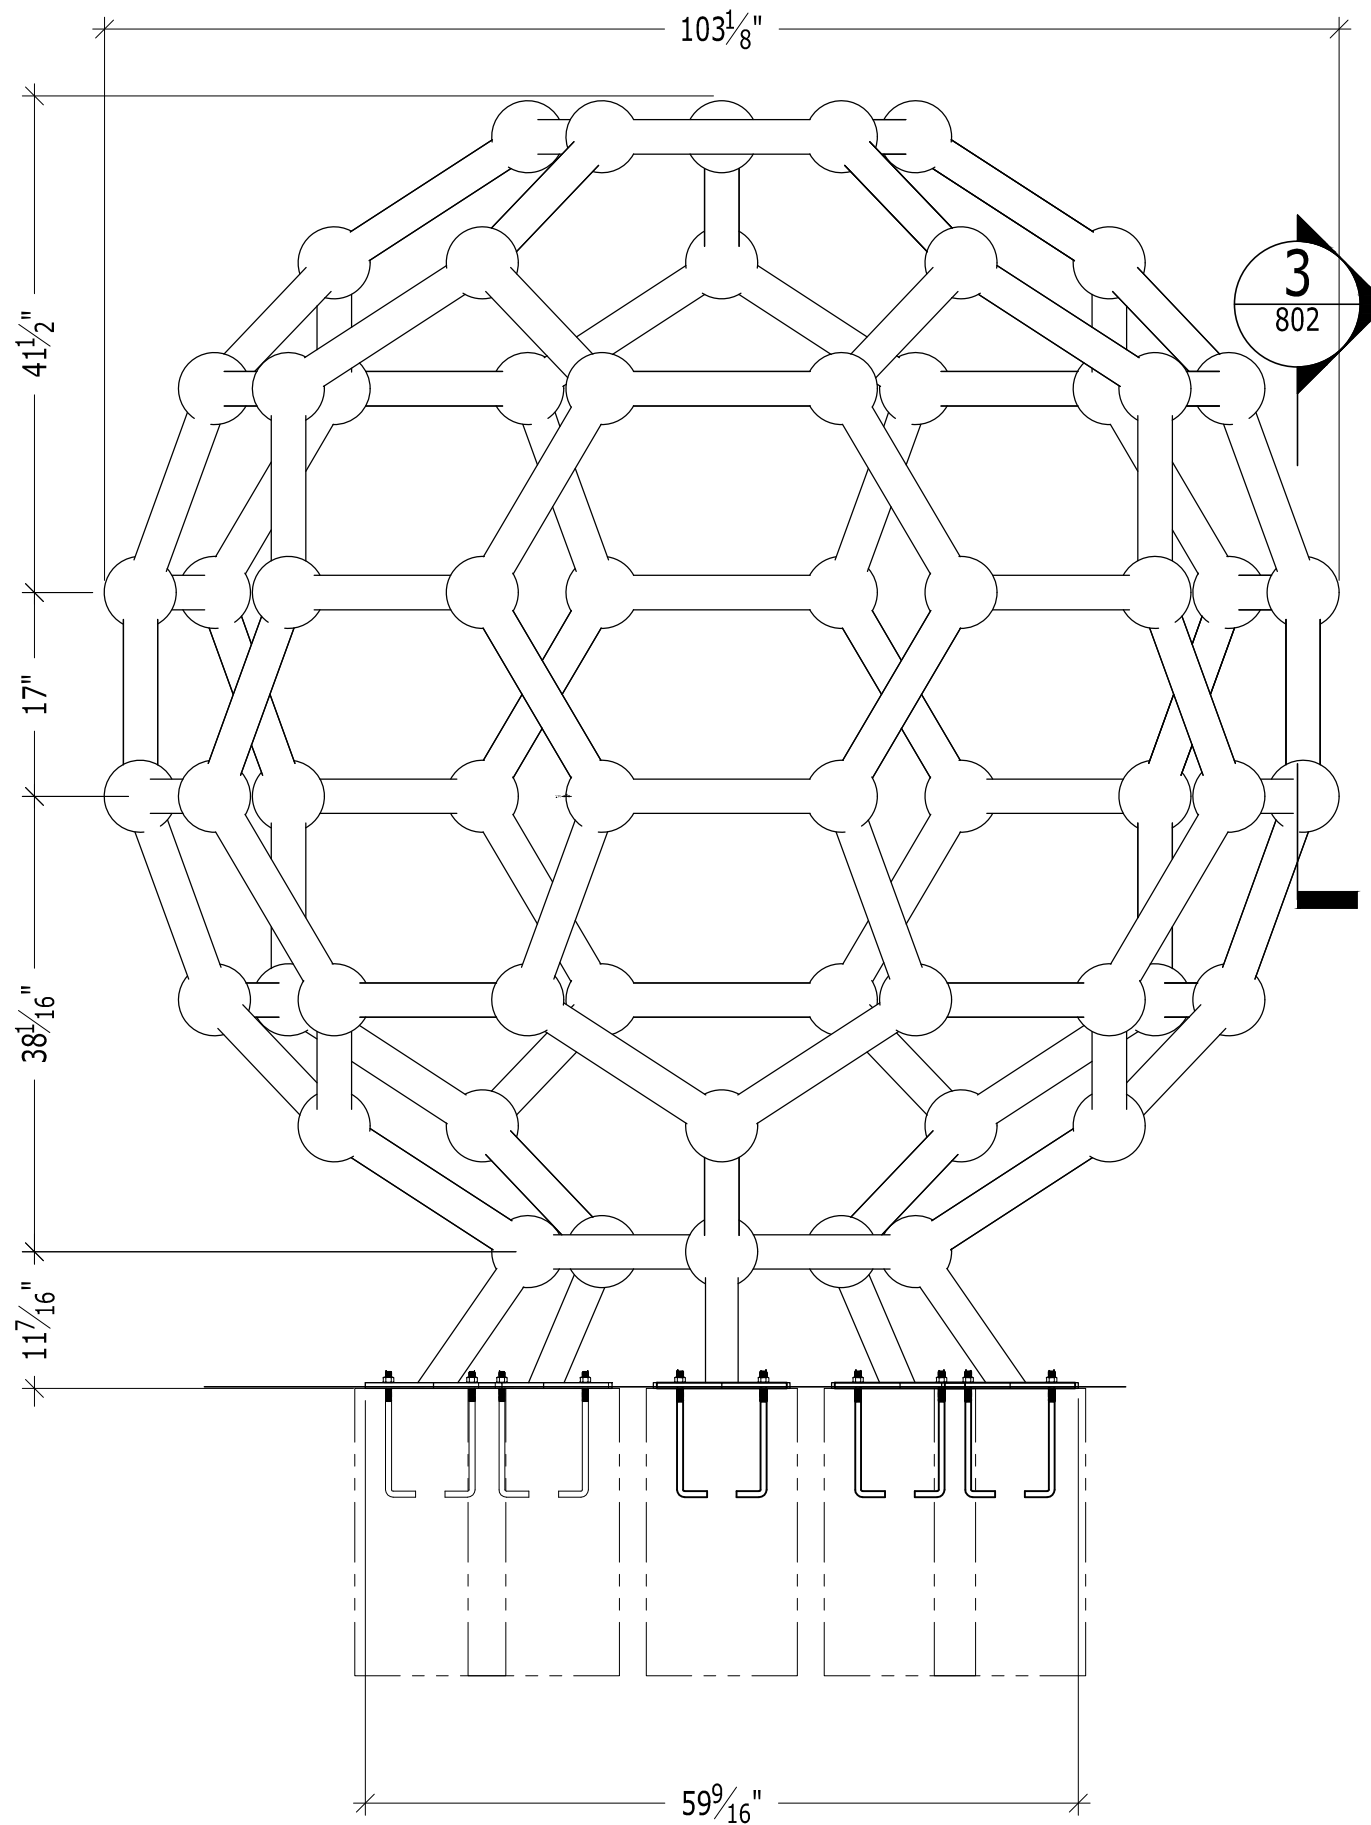

B ELEVATION -
SCALE: 3/4" = 1'-0"

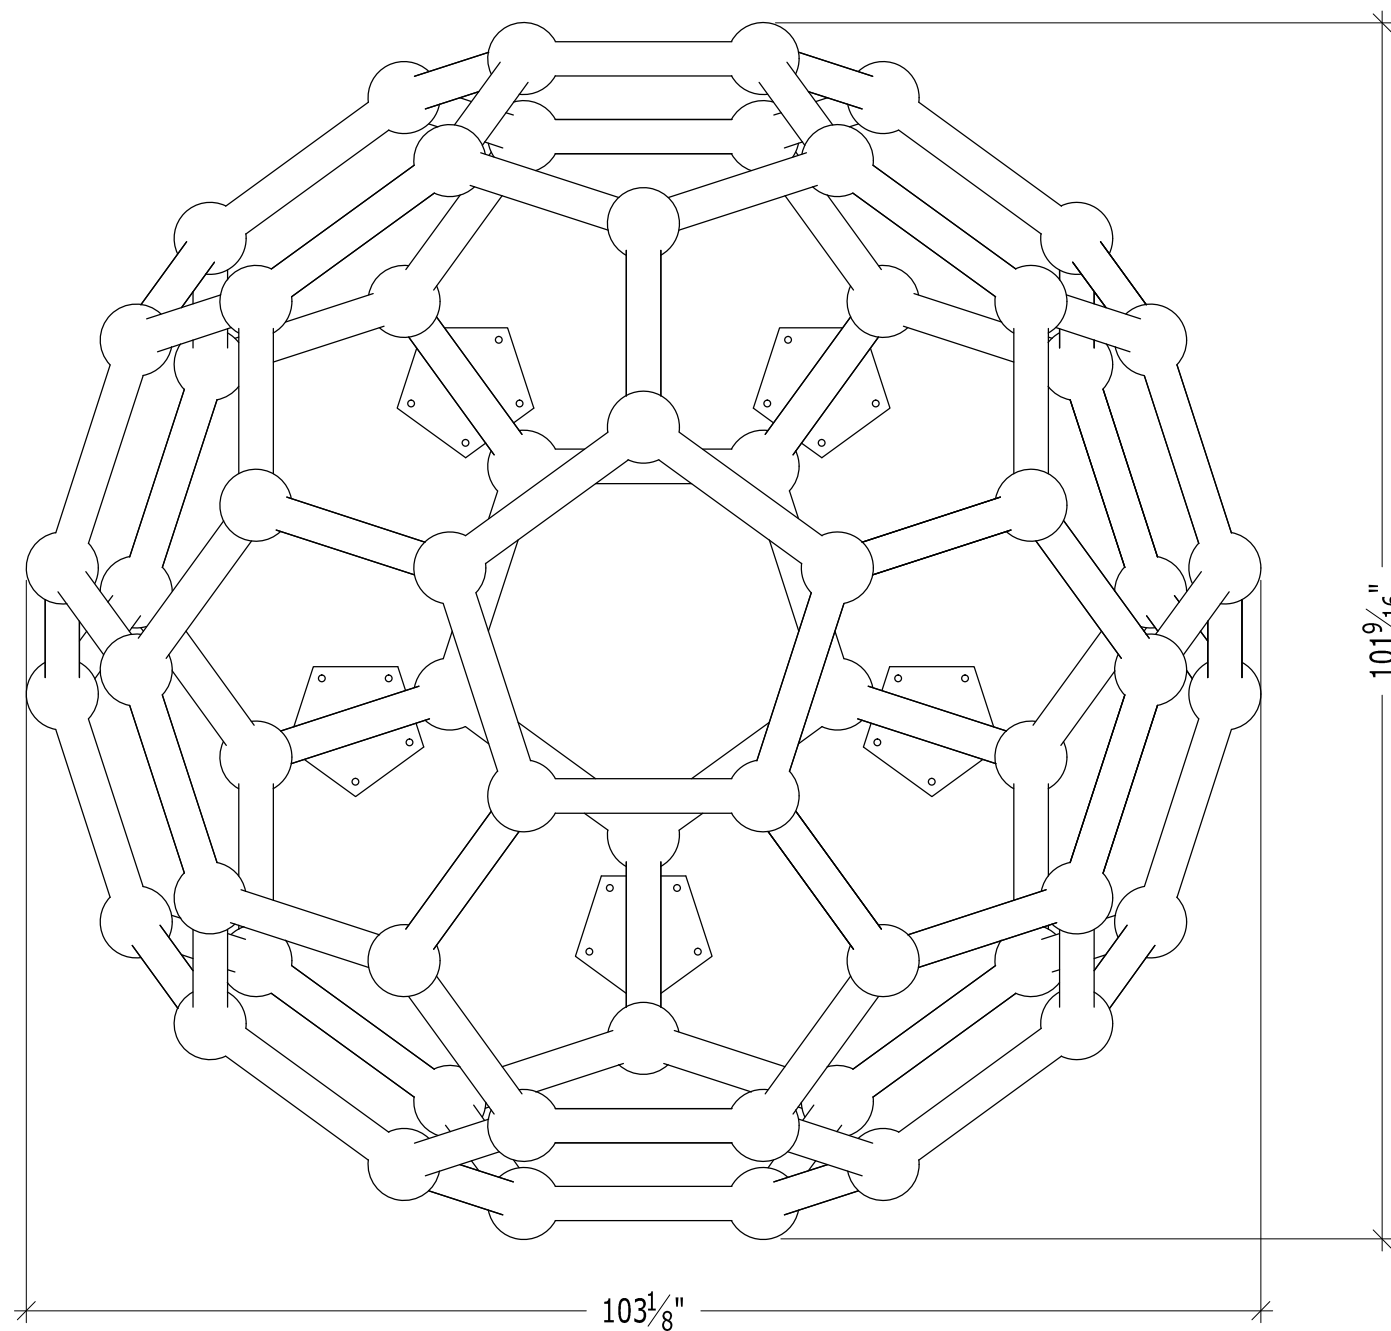


PLAN -
SCALE: 3/4" = 1'-0"

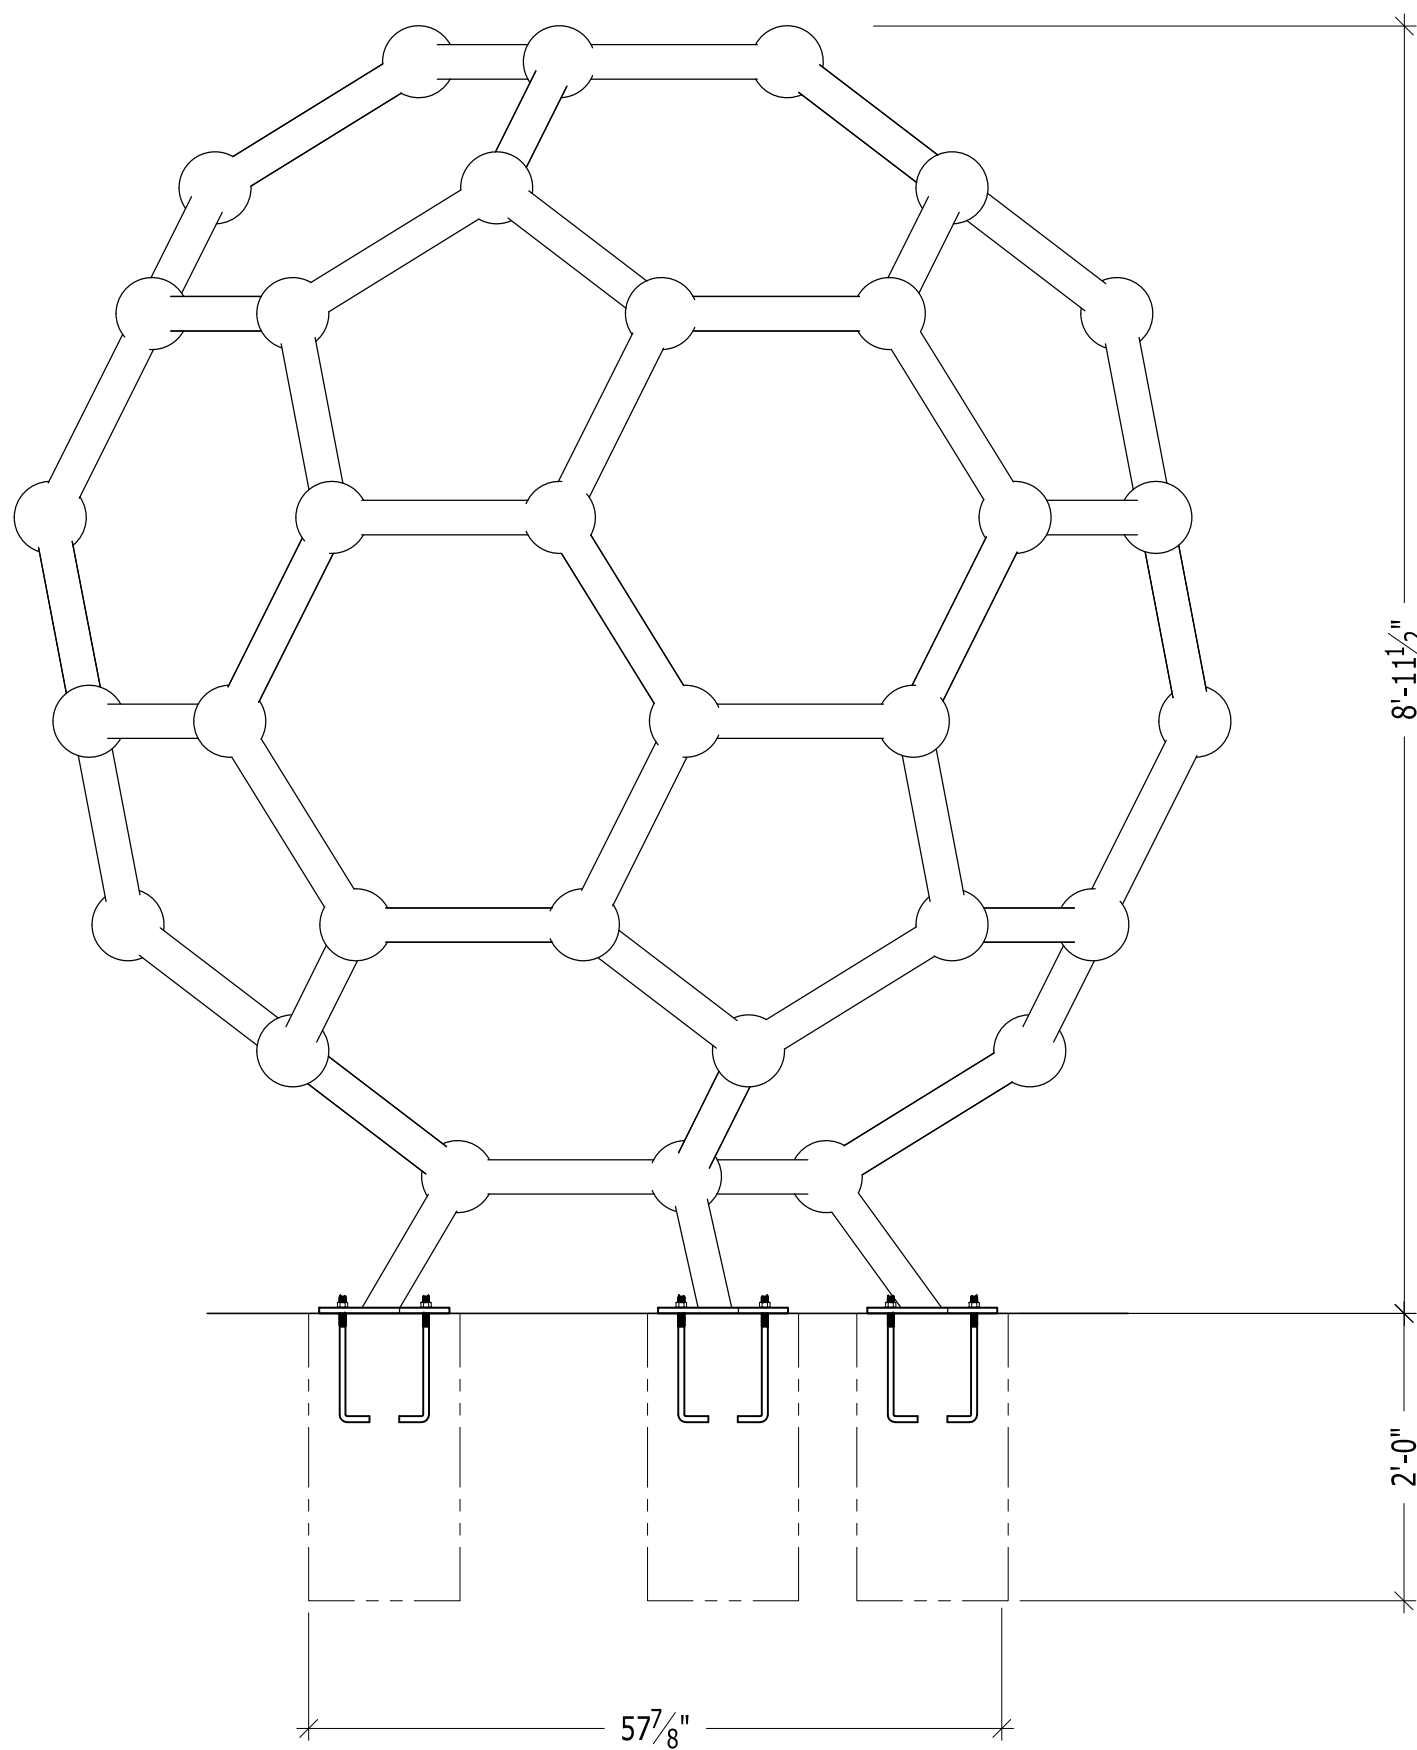

A ELEVATION -
SCALE: 3/4" = 1'-0"

FOR REVIEW

BECAUSE IT'S AT KID'S SPACE, AND IN A PARK KIDS ARE DEFINITELY GOING TO CLIMB THIS INSTALLATION. I WOULD SUGGEST ADDING A ROPE INTERIOR FOR SAFETY AND TO GET AHEAD OF CLIMBING CONCERNS

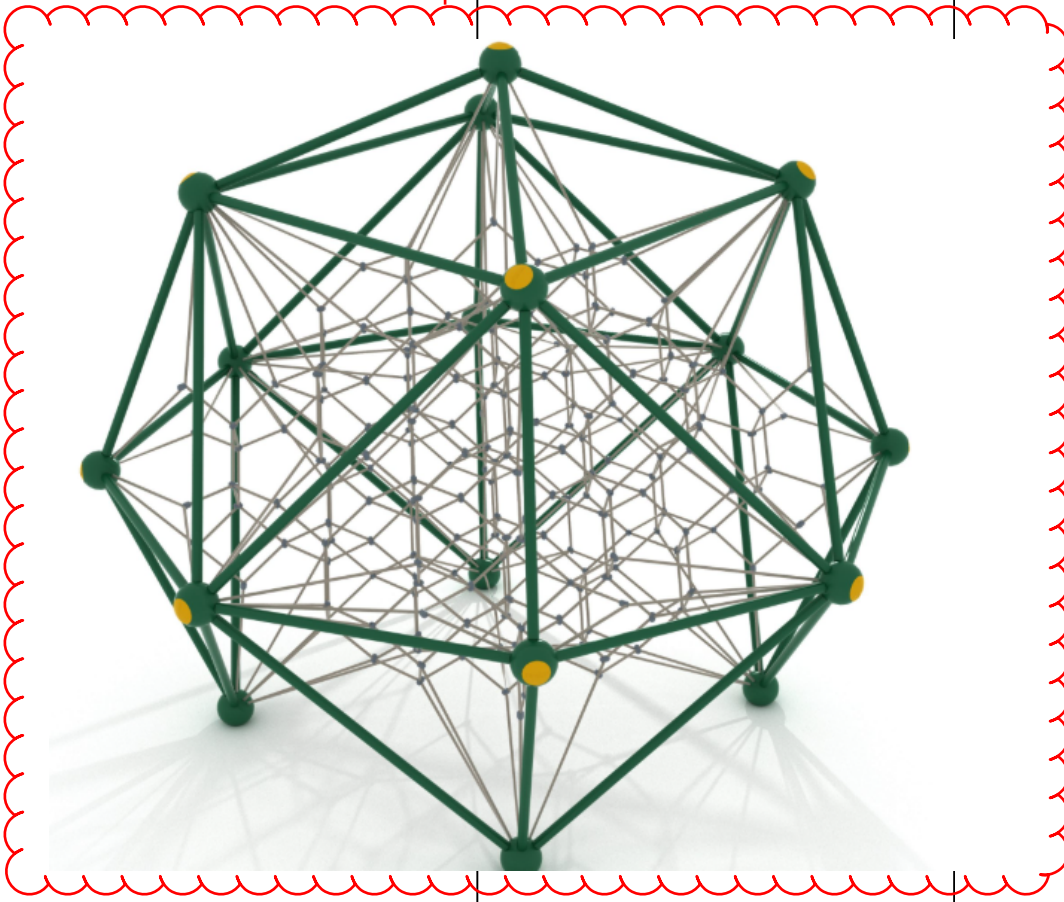

JACK ANDERSON
FABRICATION DESIGN

3326 CAZADOR STREET
LOS ANGELES CA 90065
623-419-4802
jack4congrss@protonmail.com

LOS ANGELES SOLAR SYSTEM PROJECT

JUPITER

2800 E. Observatory Rd
Los Angeles, CA 90027

DRAWN BY
JACK

DRAWING DATE
2-5-2026

REVISION DATE
--/------

TITLE
ELEVATION, SECTIONS

SCALE
AS NOTED

SHEET
JU800

JACK ANDERSON
FABRICATION DESIGN
3326 CAZADOR STREET
LOS ANGELES CA 90065
623-419-4802
jack4congrss@protonmail.com

JUPITER GALILEAN SATELLITES

LOS ANGELES SOLAR SYSTEM PROJECT

2800 E. Observatory Rd
Los Angeles, CA 90027

DRAWN BY
JACK


DRAWING DATE
2-5-2026

REVISION DATE
--/------


TITLE
ELEVATION, SECTIONS

SCALE
AS NOTED


SHEET
JU801

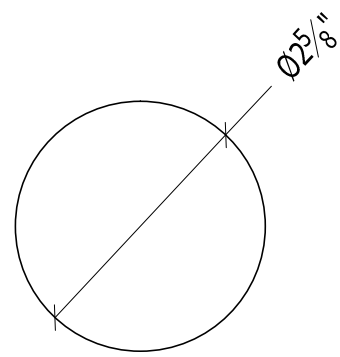


1 DETAIL - IO
SCALE: HALF SCALE

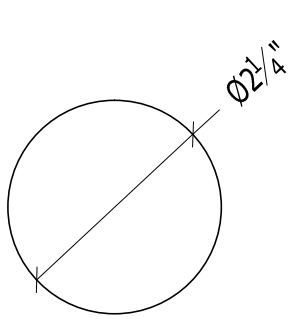

2 DETAIL - EUROPA
SCALE: HALF SCALE

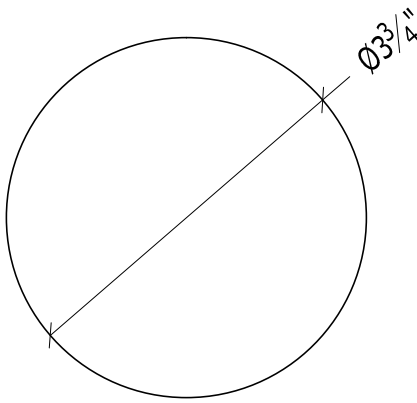


3 DETAIL - GANYMEDE
SCALE: HALF SCALE

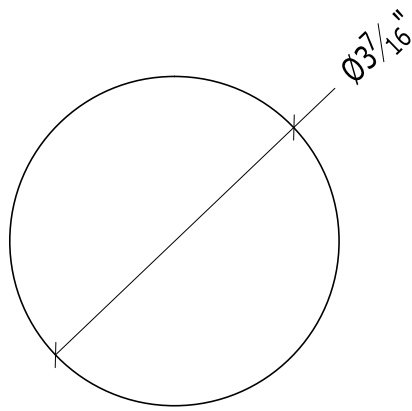

4 DETAIL - CALLISTO
SCALE: HALF SCALE




A ELEVATION - COMPANION GRAPHIC
SCALE: HALF SCALE




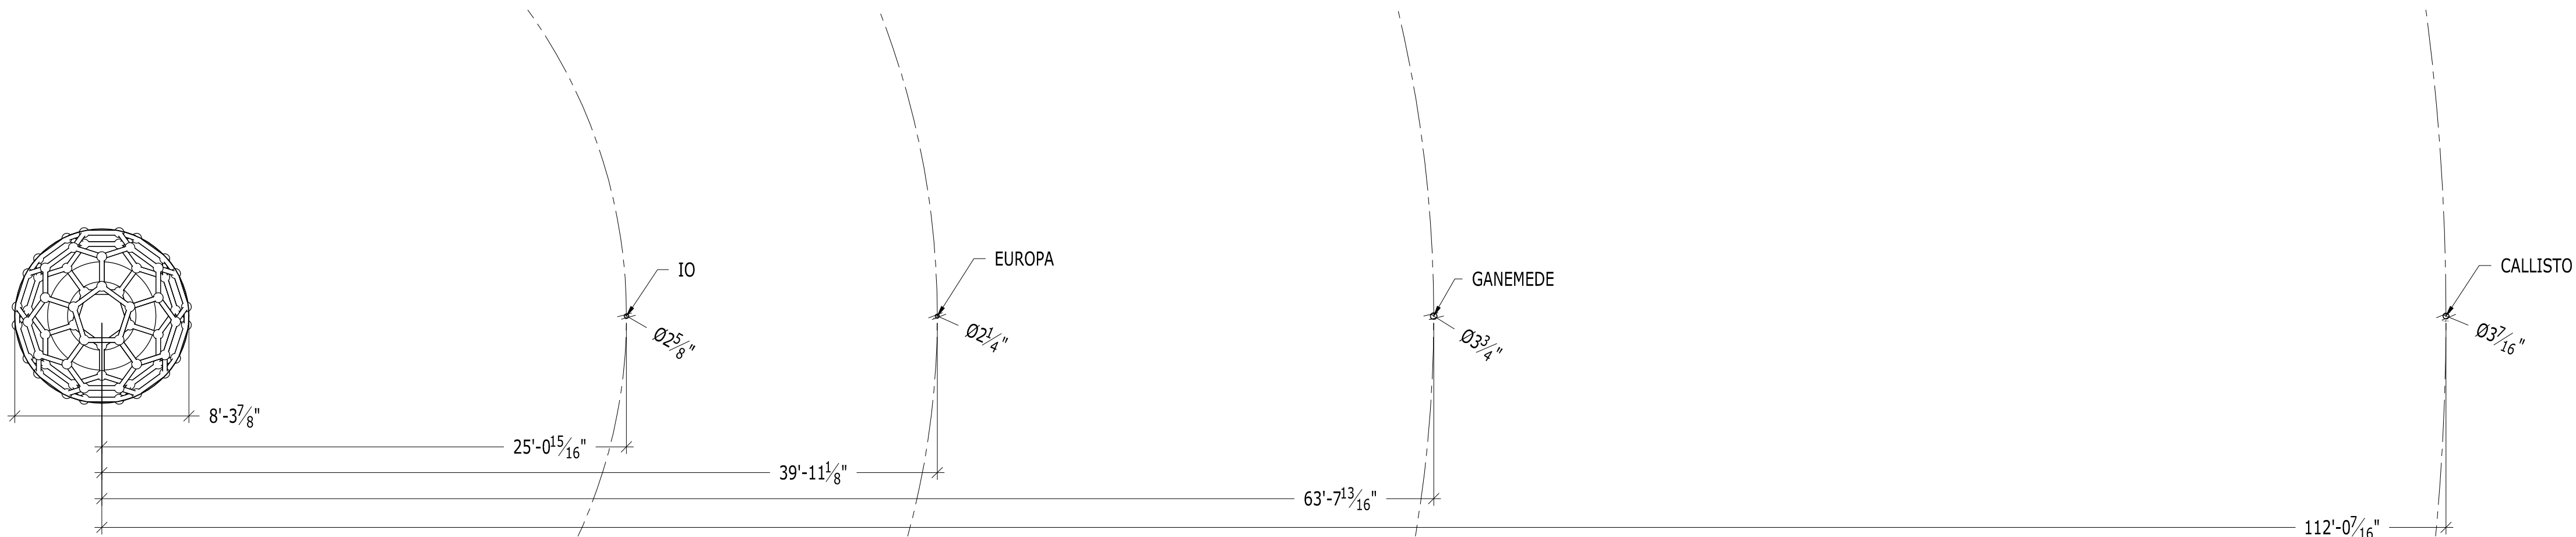


PLAN - GALILEAN SATELLITES
SCALE: 3/16" = 1'-0"


FOR REVIEW

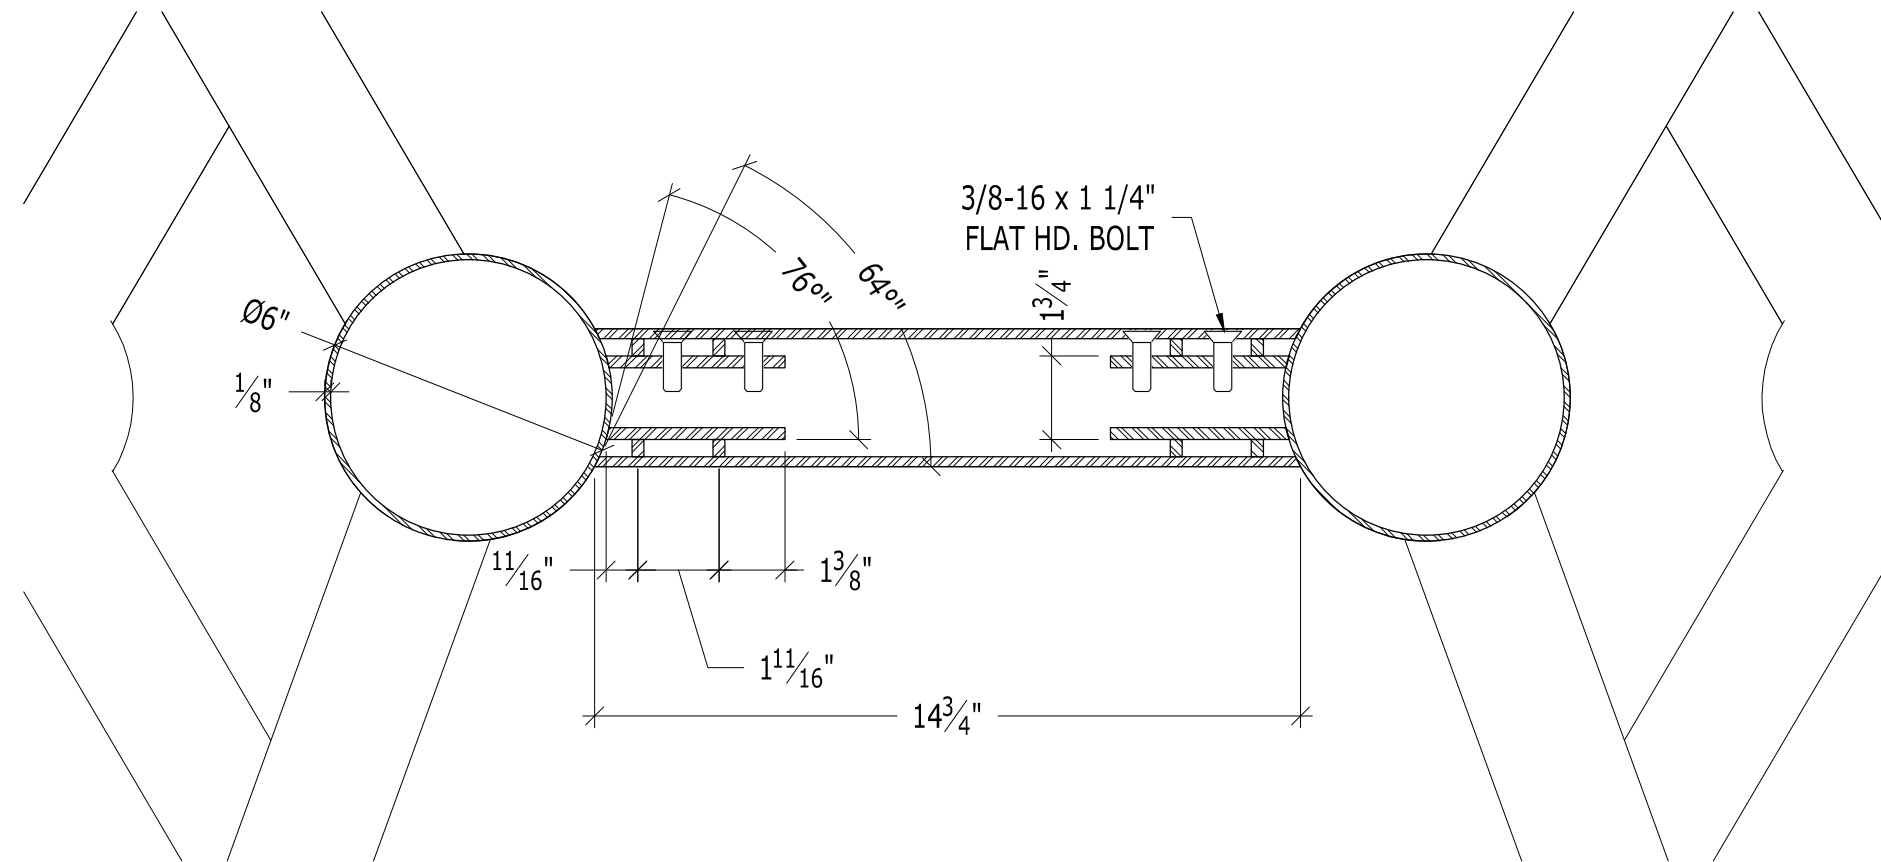


3 SECTION -
SCALE: 3" = 1'-0"

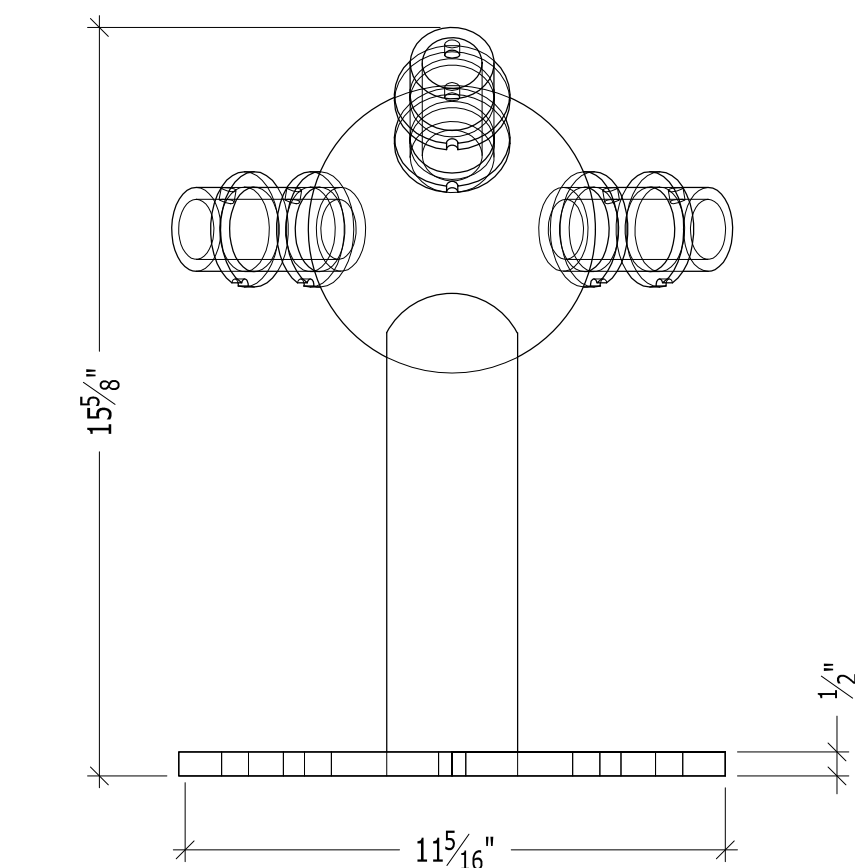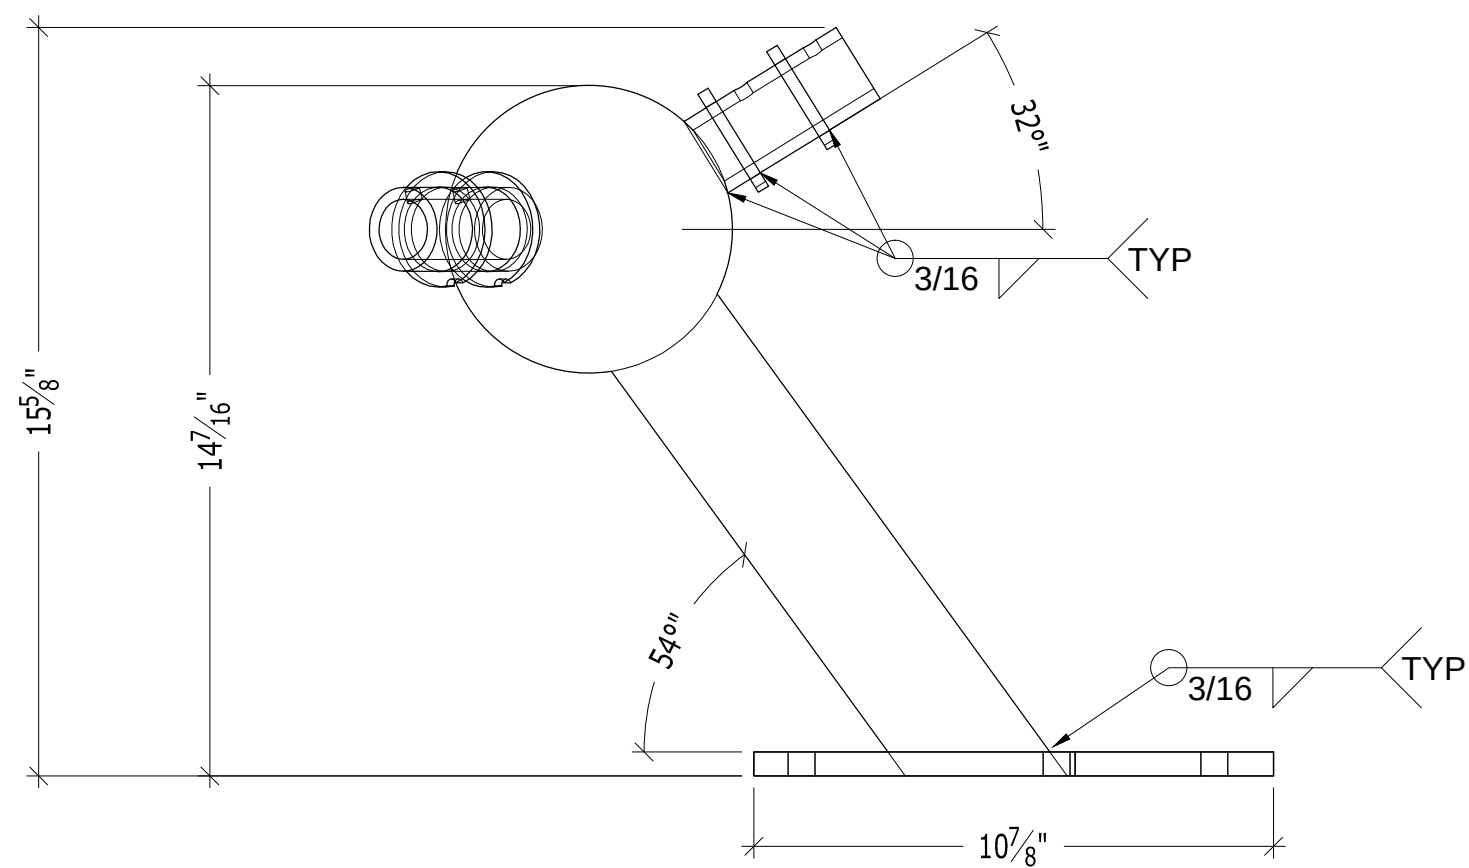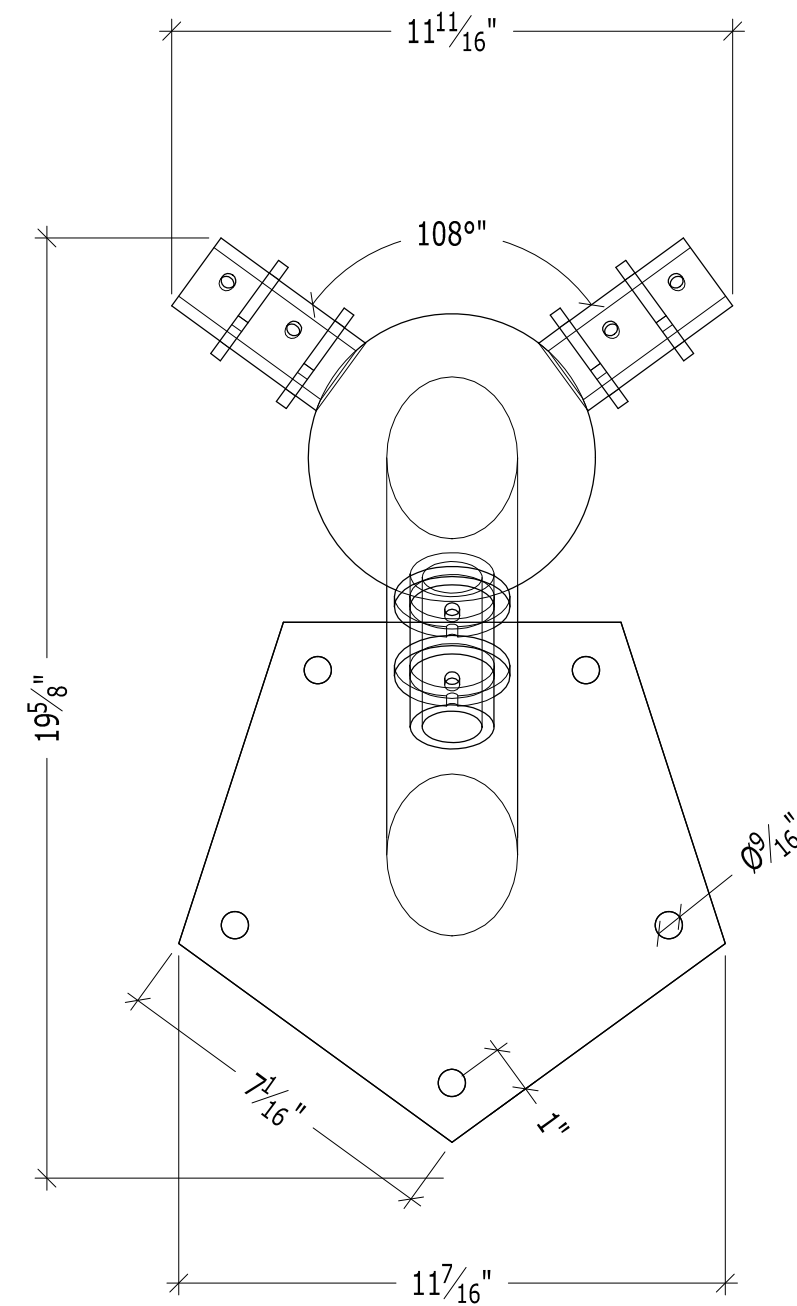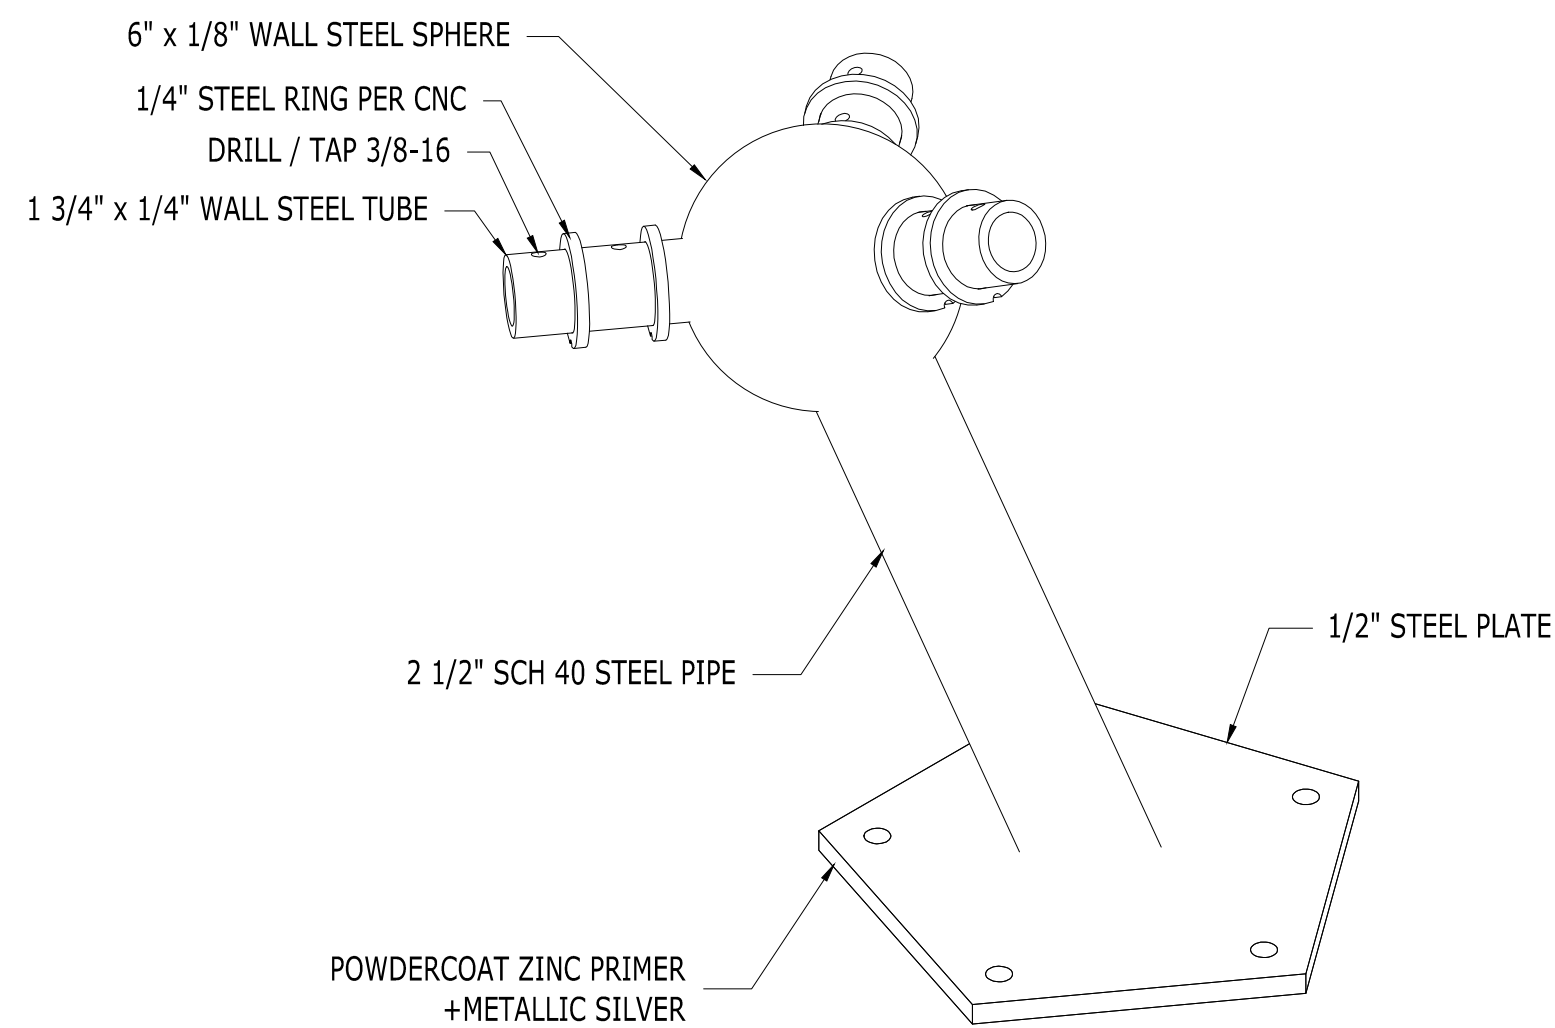


4 DETAIL -FOOT (5) 26.6 LBS EACH
SCALE: 3" = 1'-0"

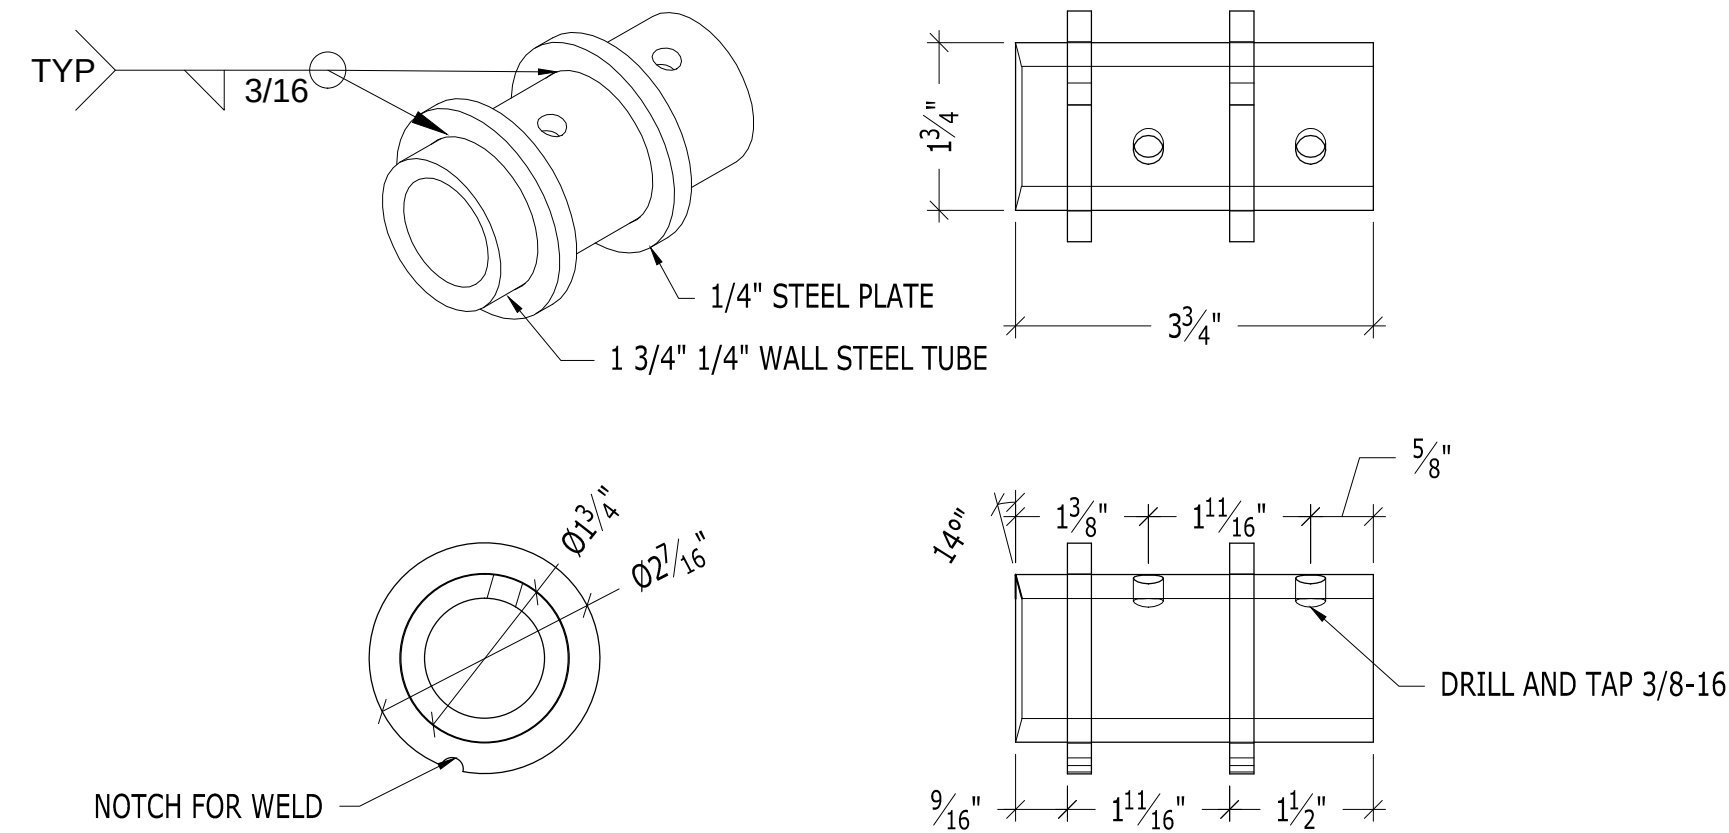

5 DETAIL - STUB (MAKE 180)
SCALE: HALF SCALE

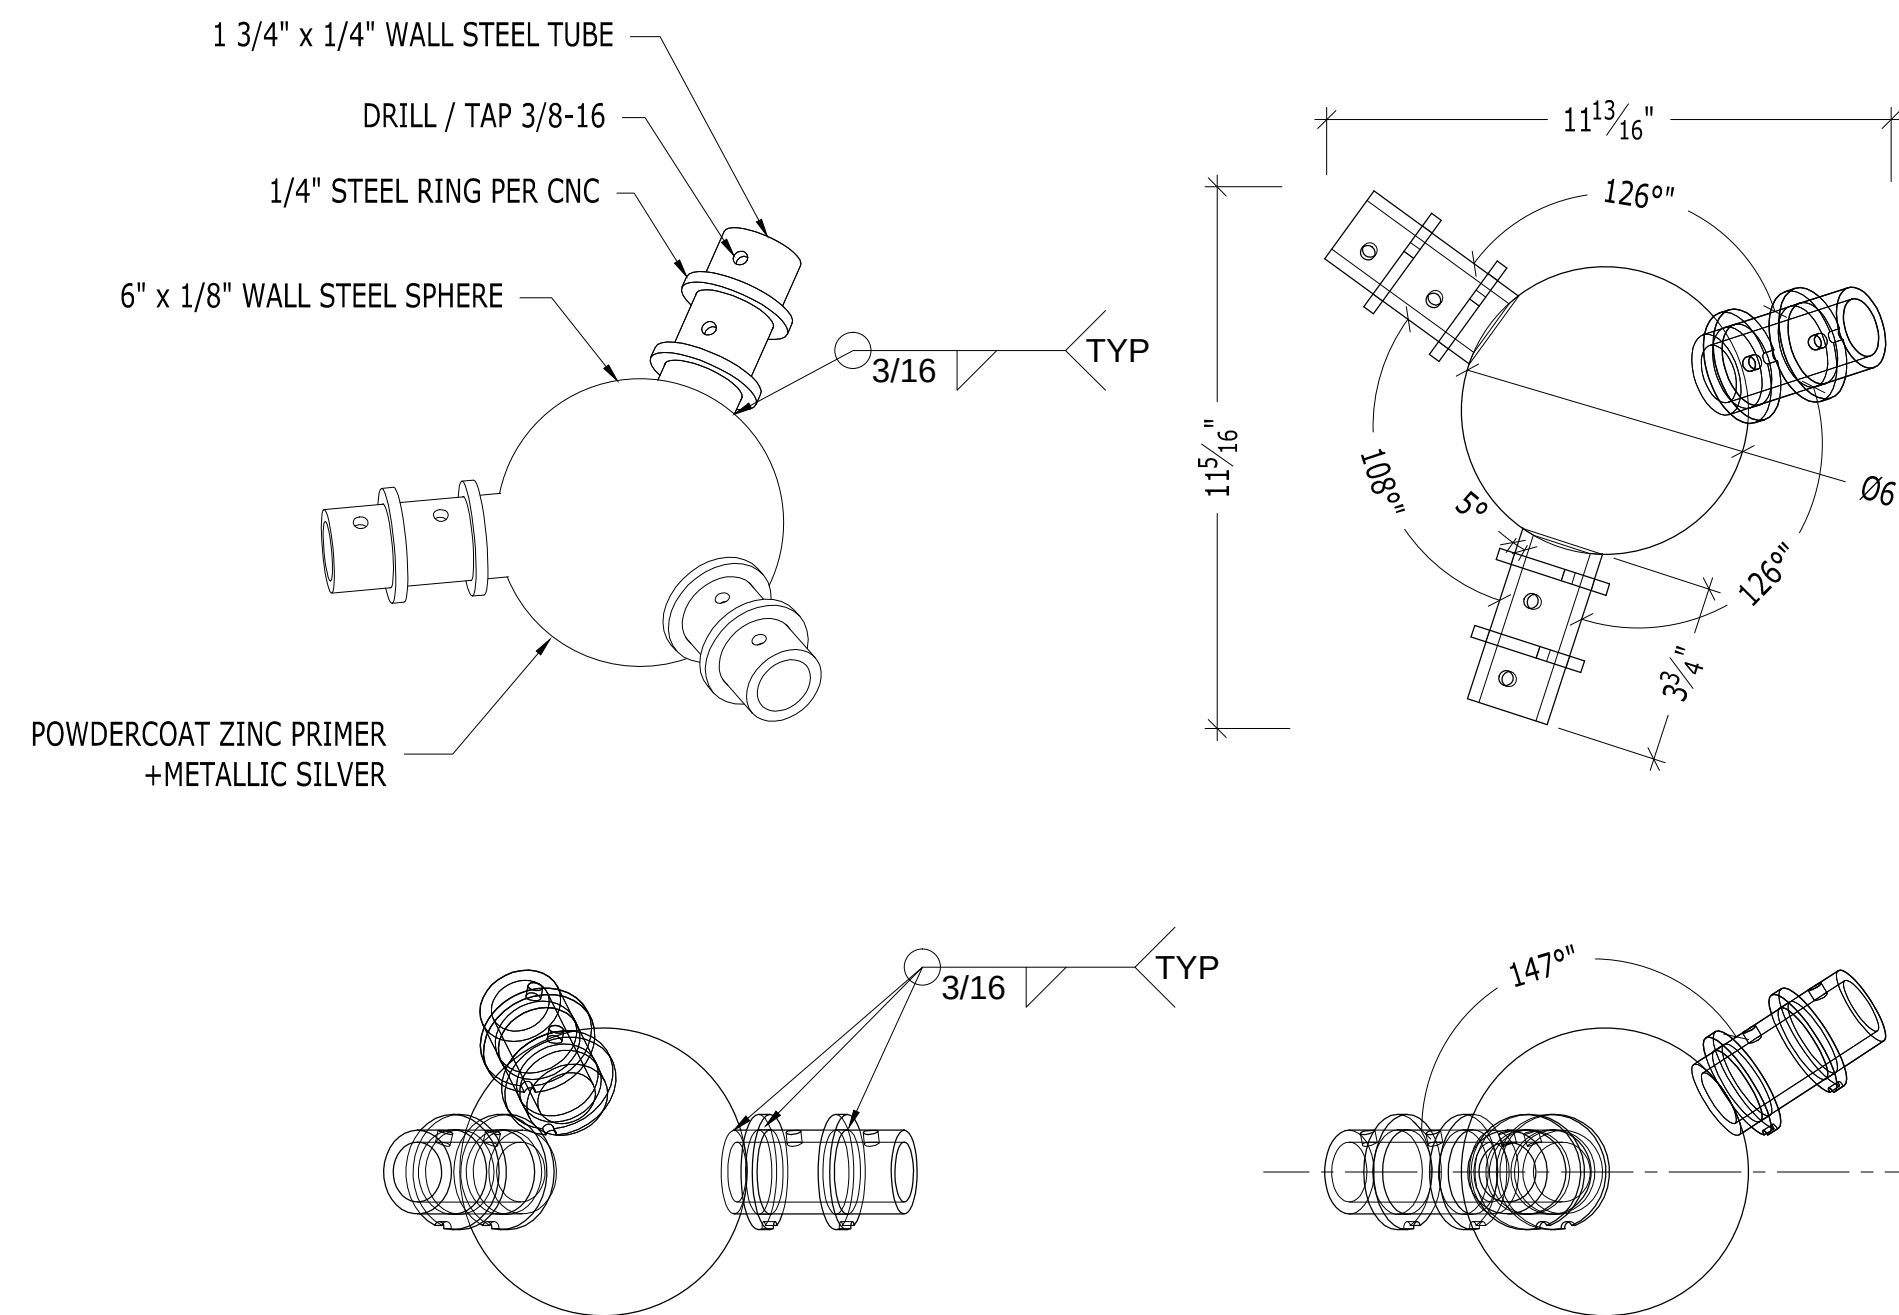

2 DETAIL -VERTEX (55) 7.6 LBS EACH
SCALE: 3" = 1'-0"

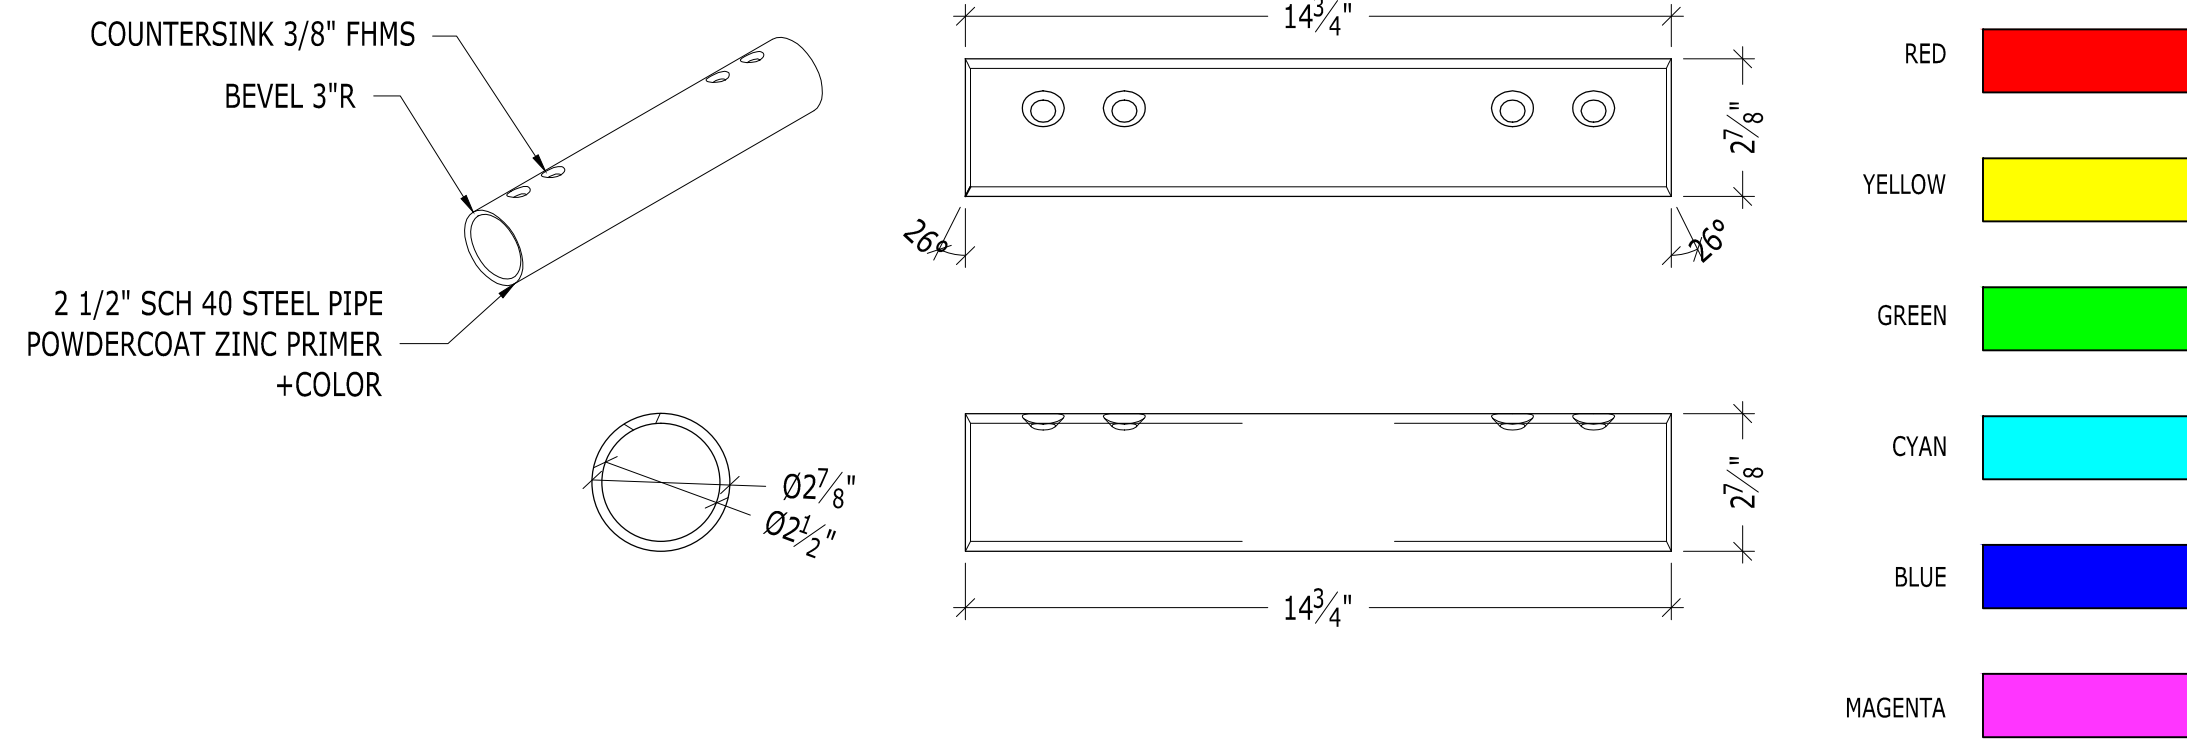


1 DETAIL -BONDS 90 (15 EACH COLOR) 7.0 LBS EACH
SCALE: 3" = 1'-0"

FOR REVIEW


JACK ANDERSON
FABRICATION DESIGN
3326 CAZADOR STREET
LOS ANGELES CA 90065
623-419-4802
jack4congrss@protonmail.com

LOS ANGELES SOLAR SYSTEM PROJECT
JUPITER DETAILS
2800 E. Observatory Rd
Los Angeles, CA 90027



DRAWN BY
JACK
DRAWING DATE
2-5-2026
REVISION DATE
--/--/----
TITLE
FAB DETAILS
SCALE
AS NOTED
SHEET
JU802

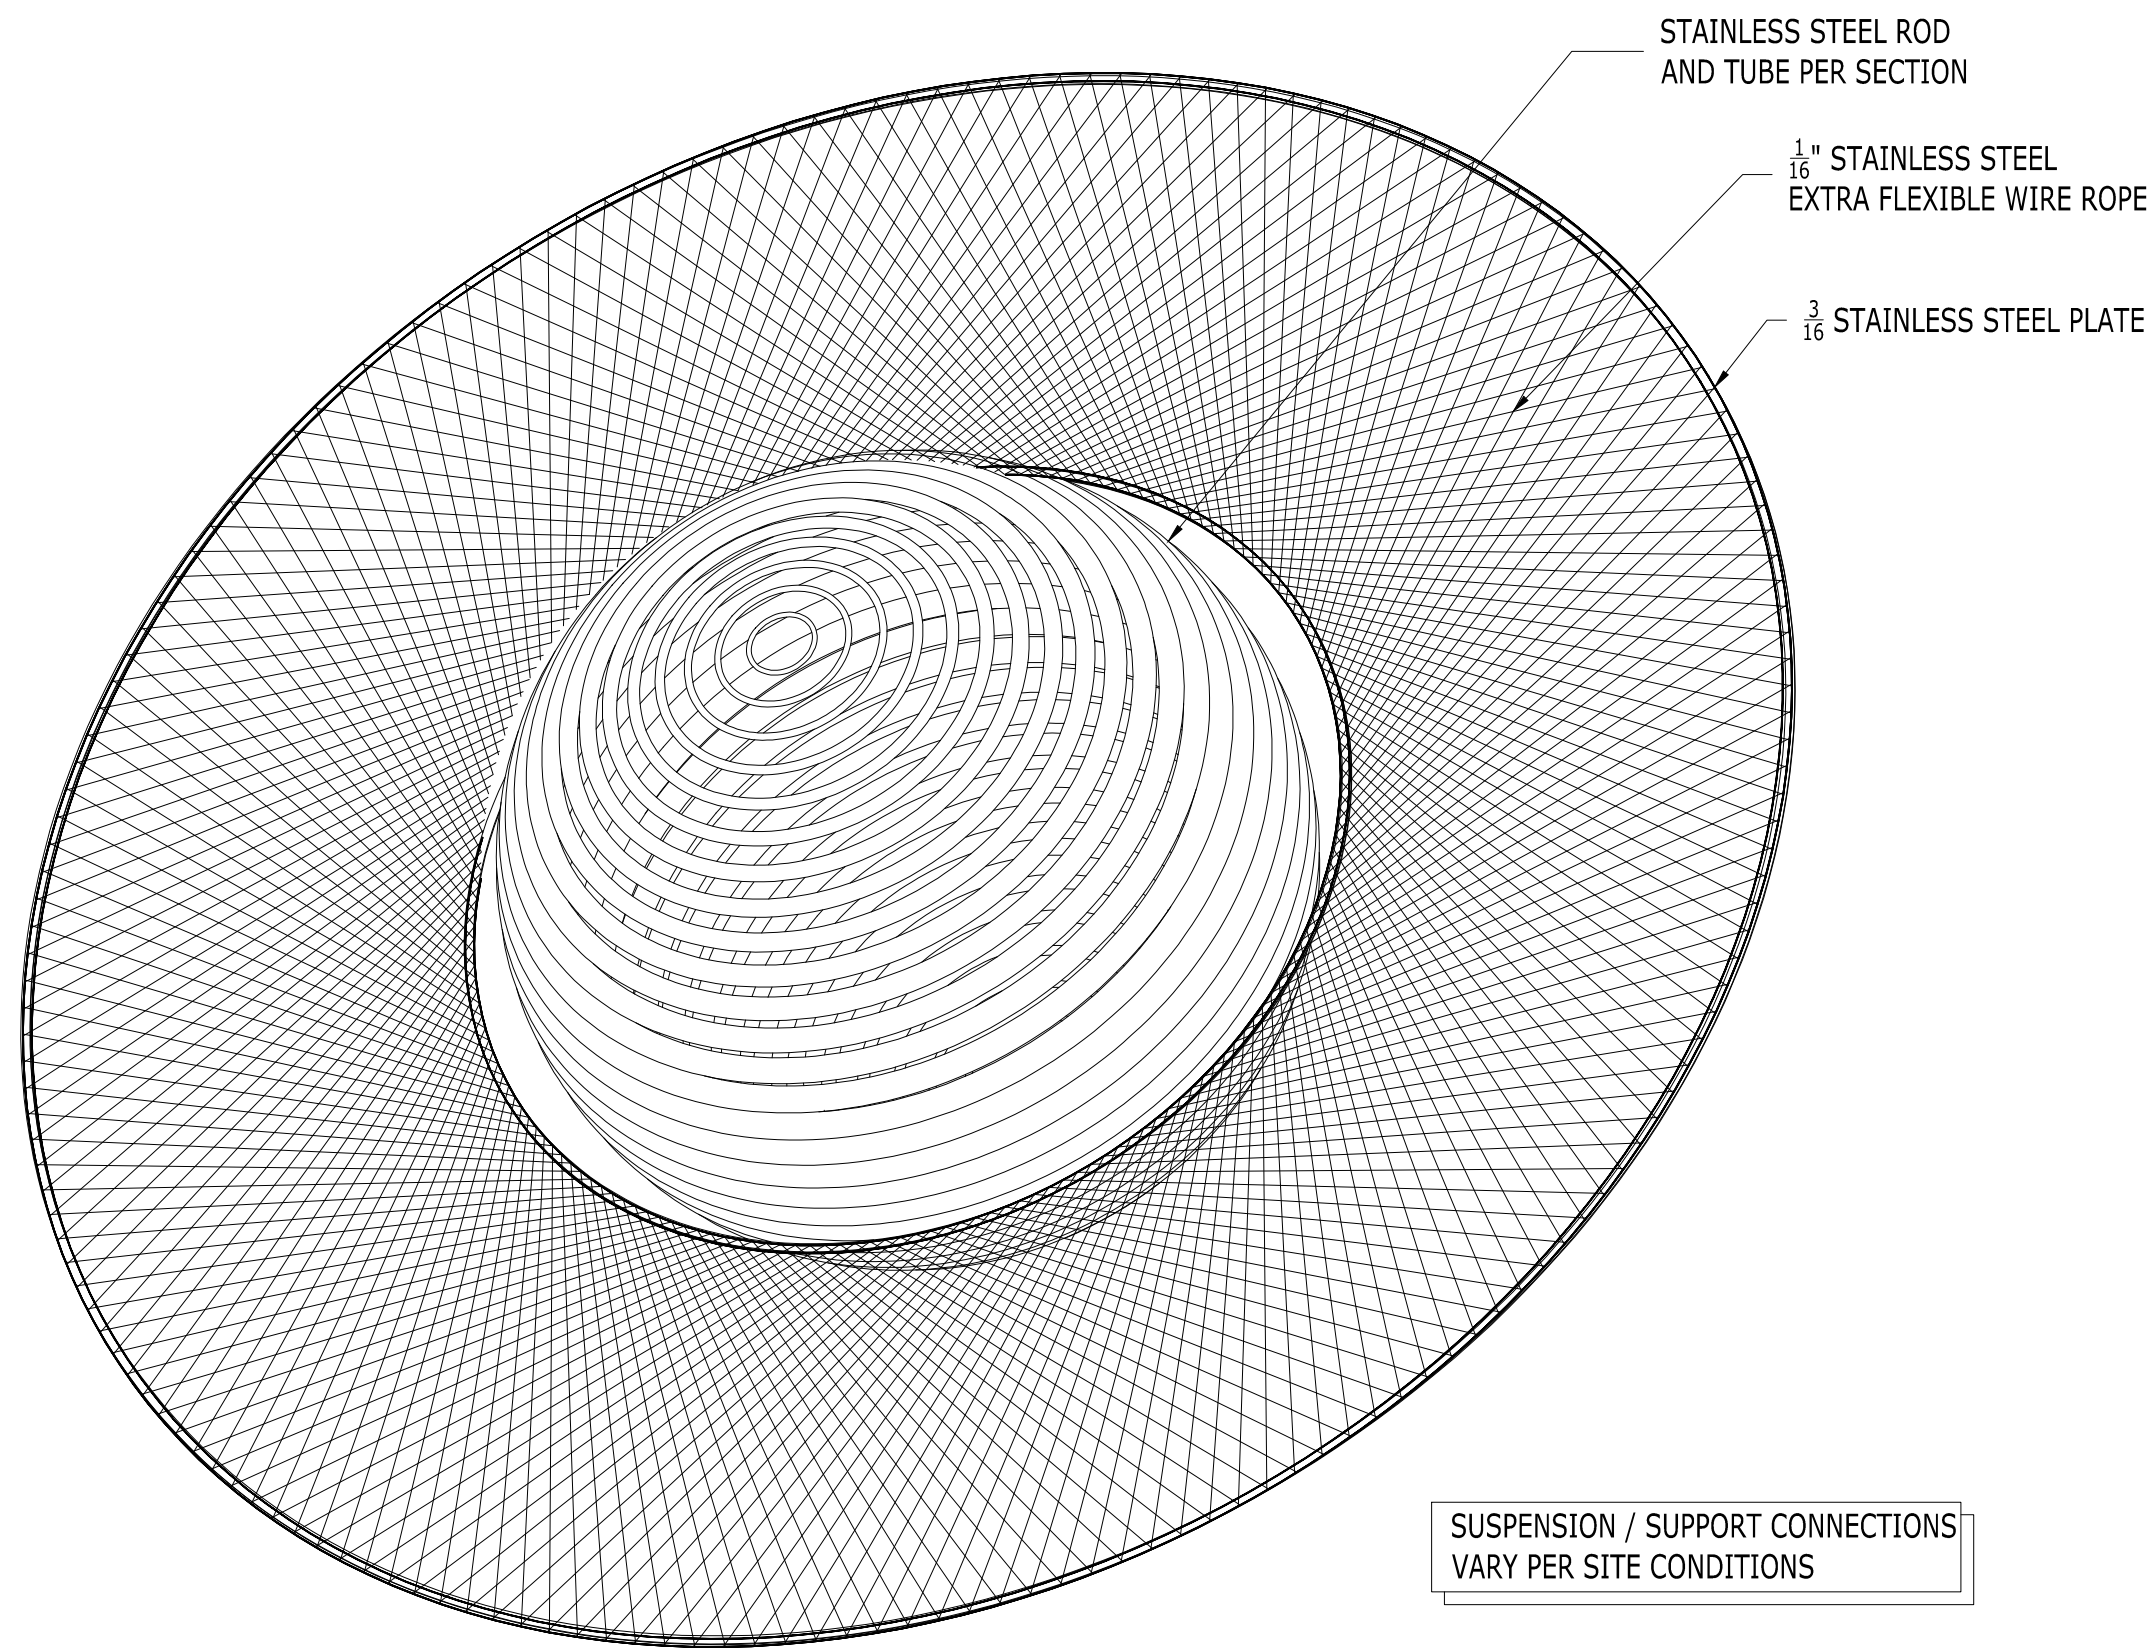


ISO VIEW
NTS

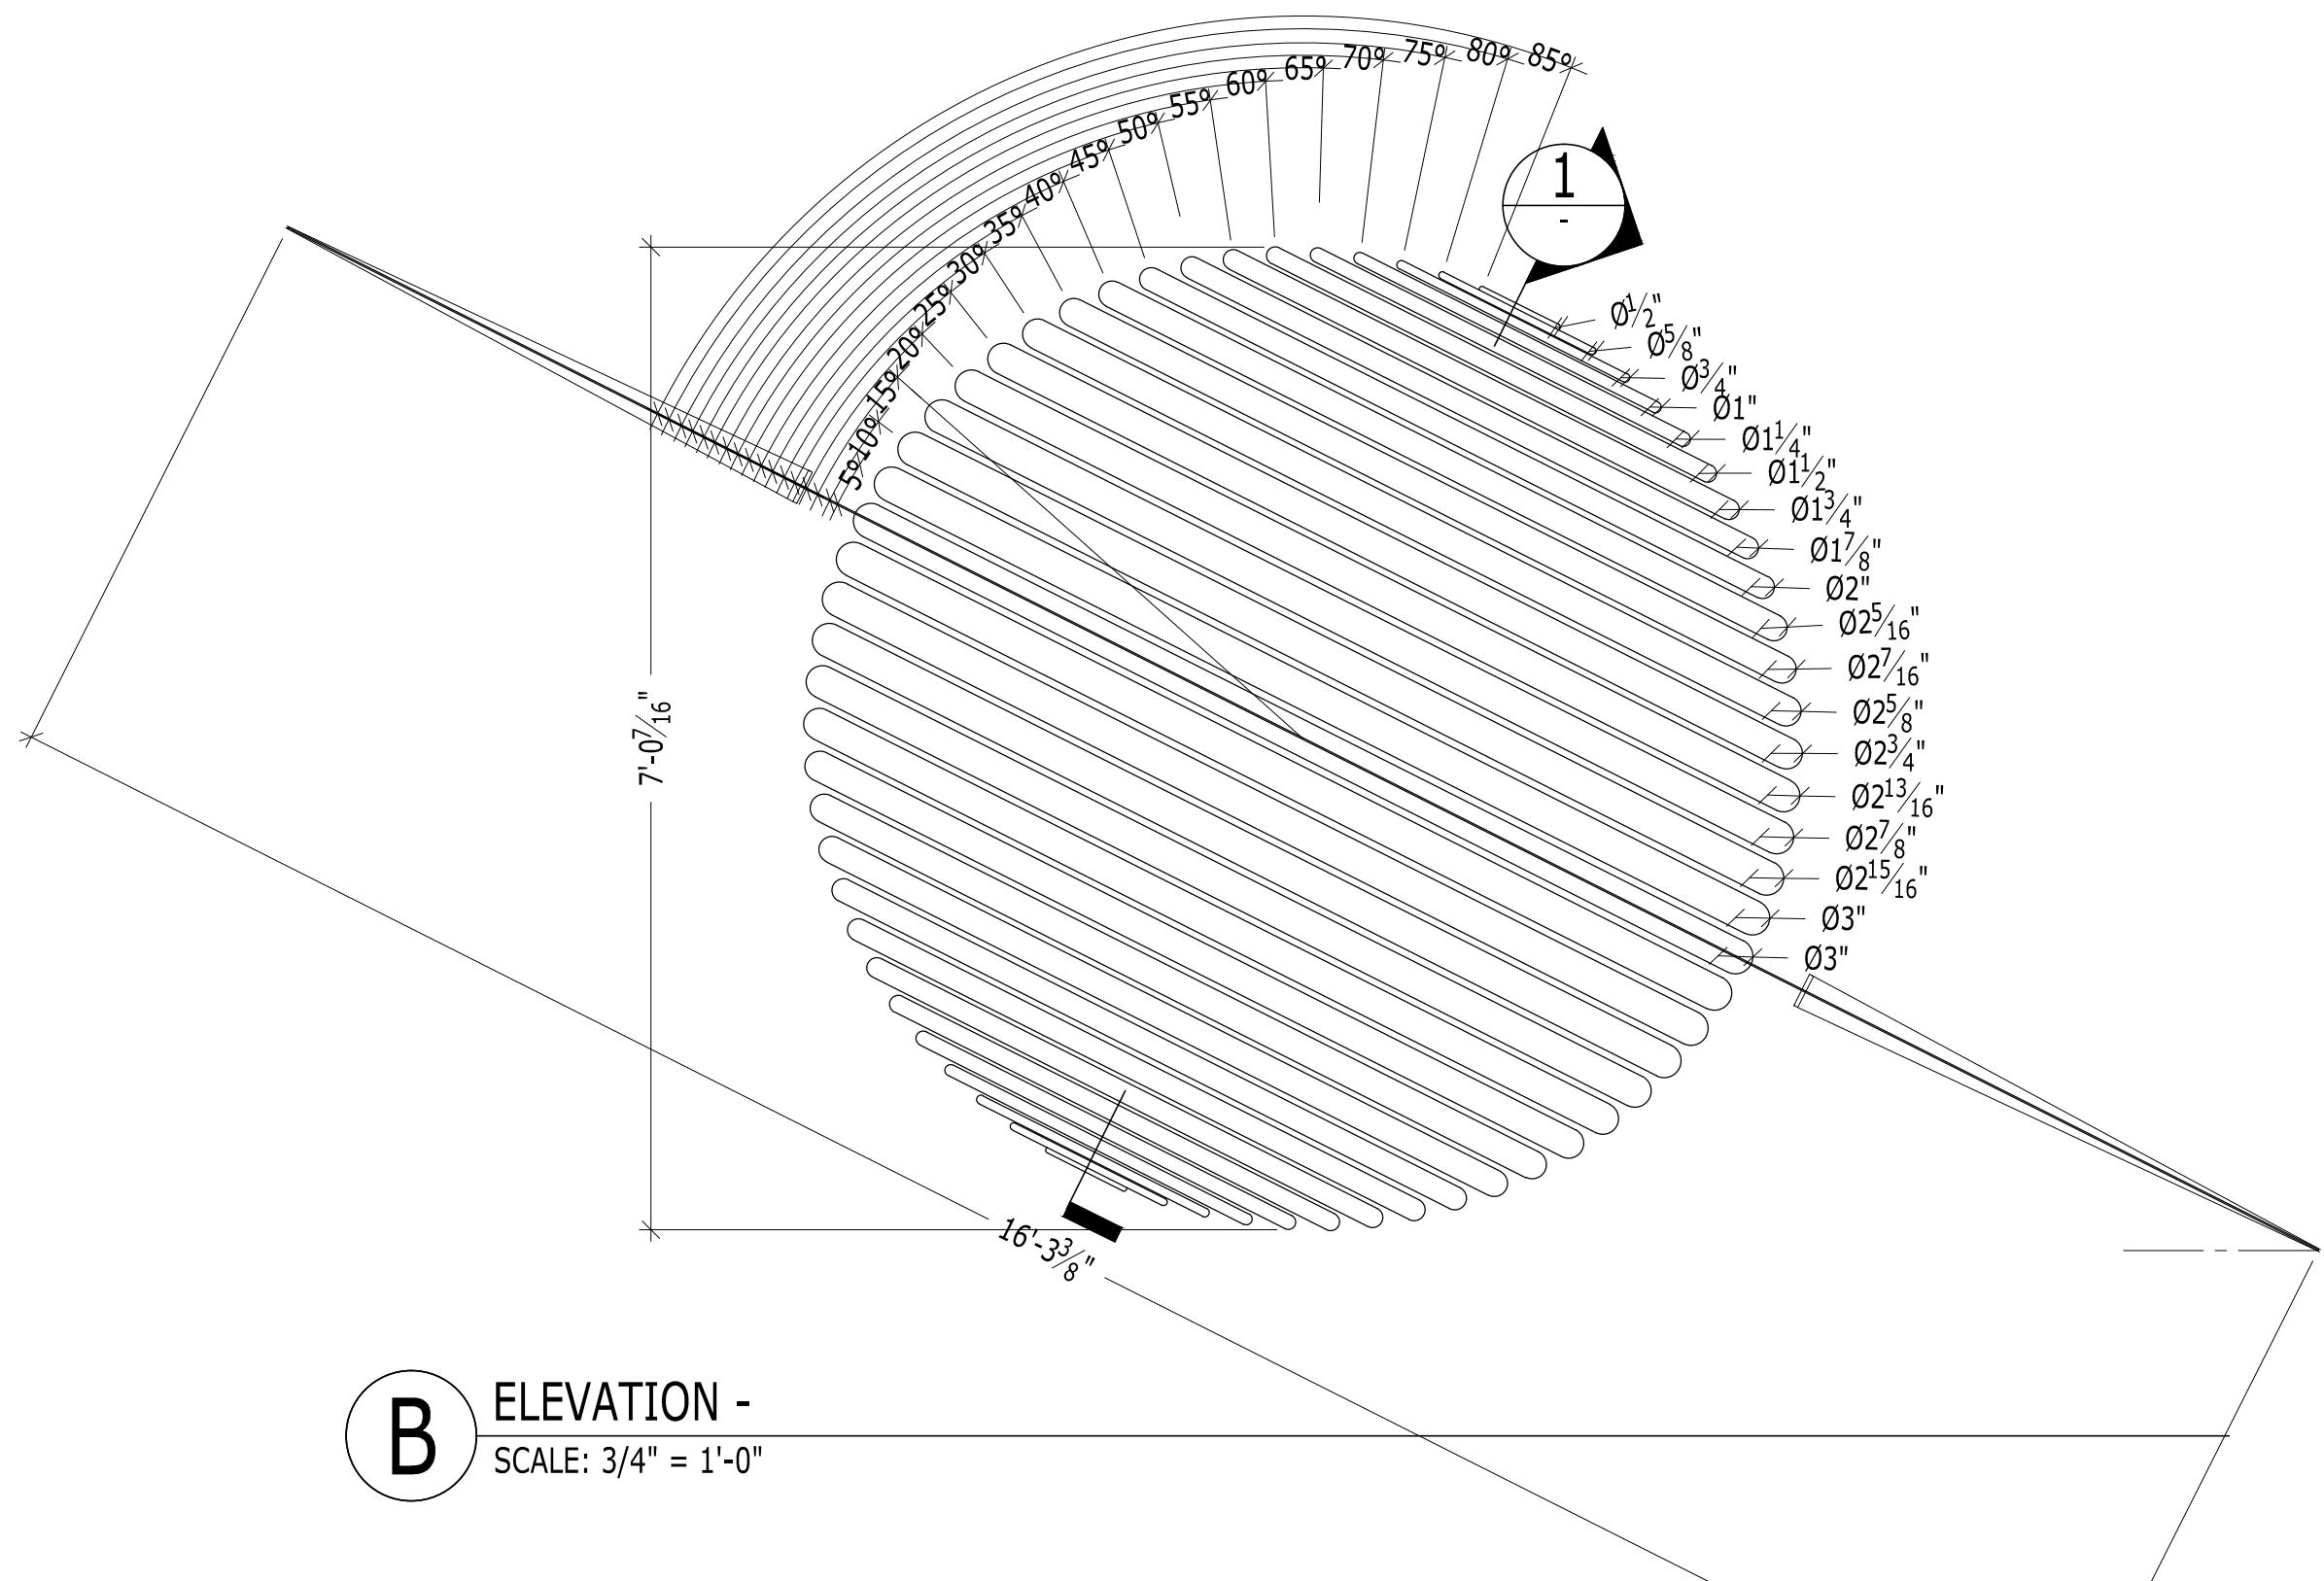

B ELEVATION -
SCALE: 3/4" = 1'-0"

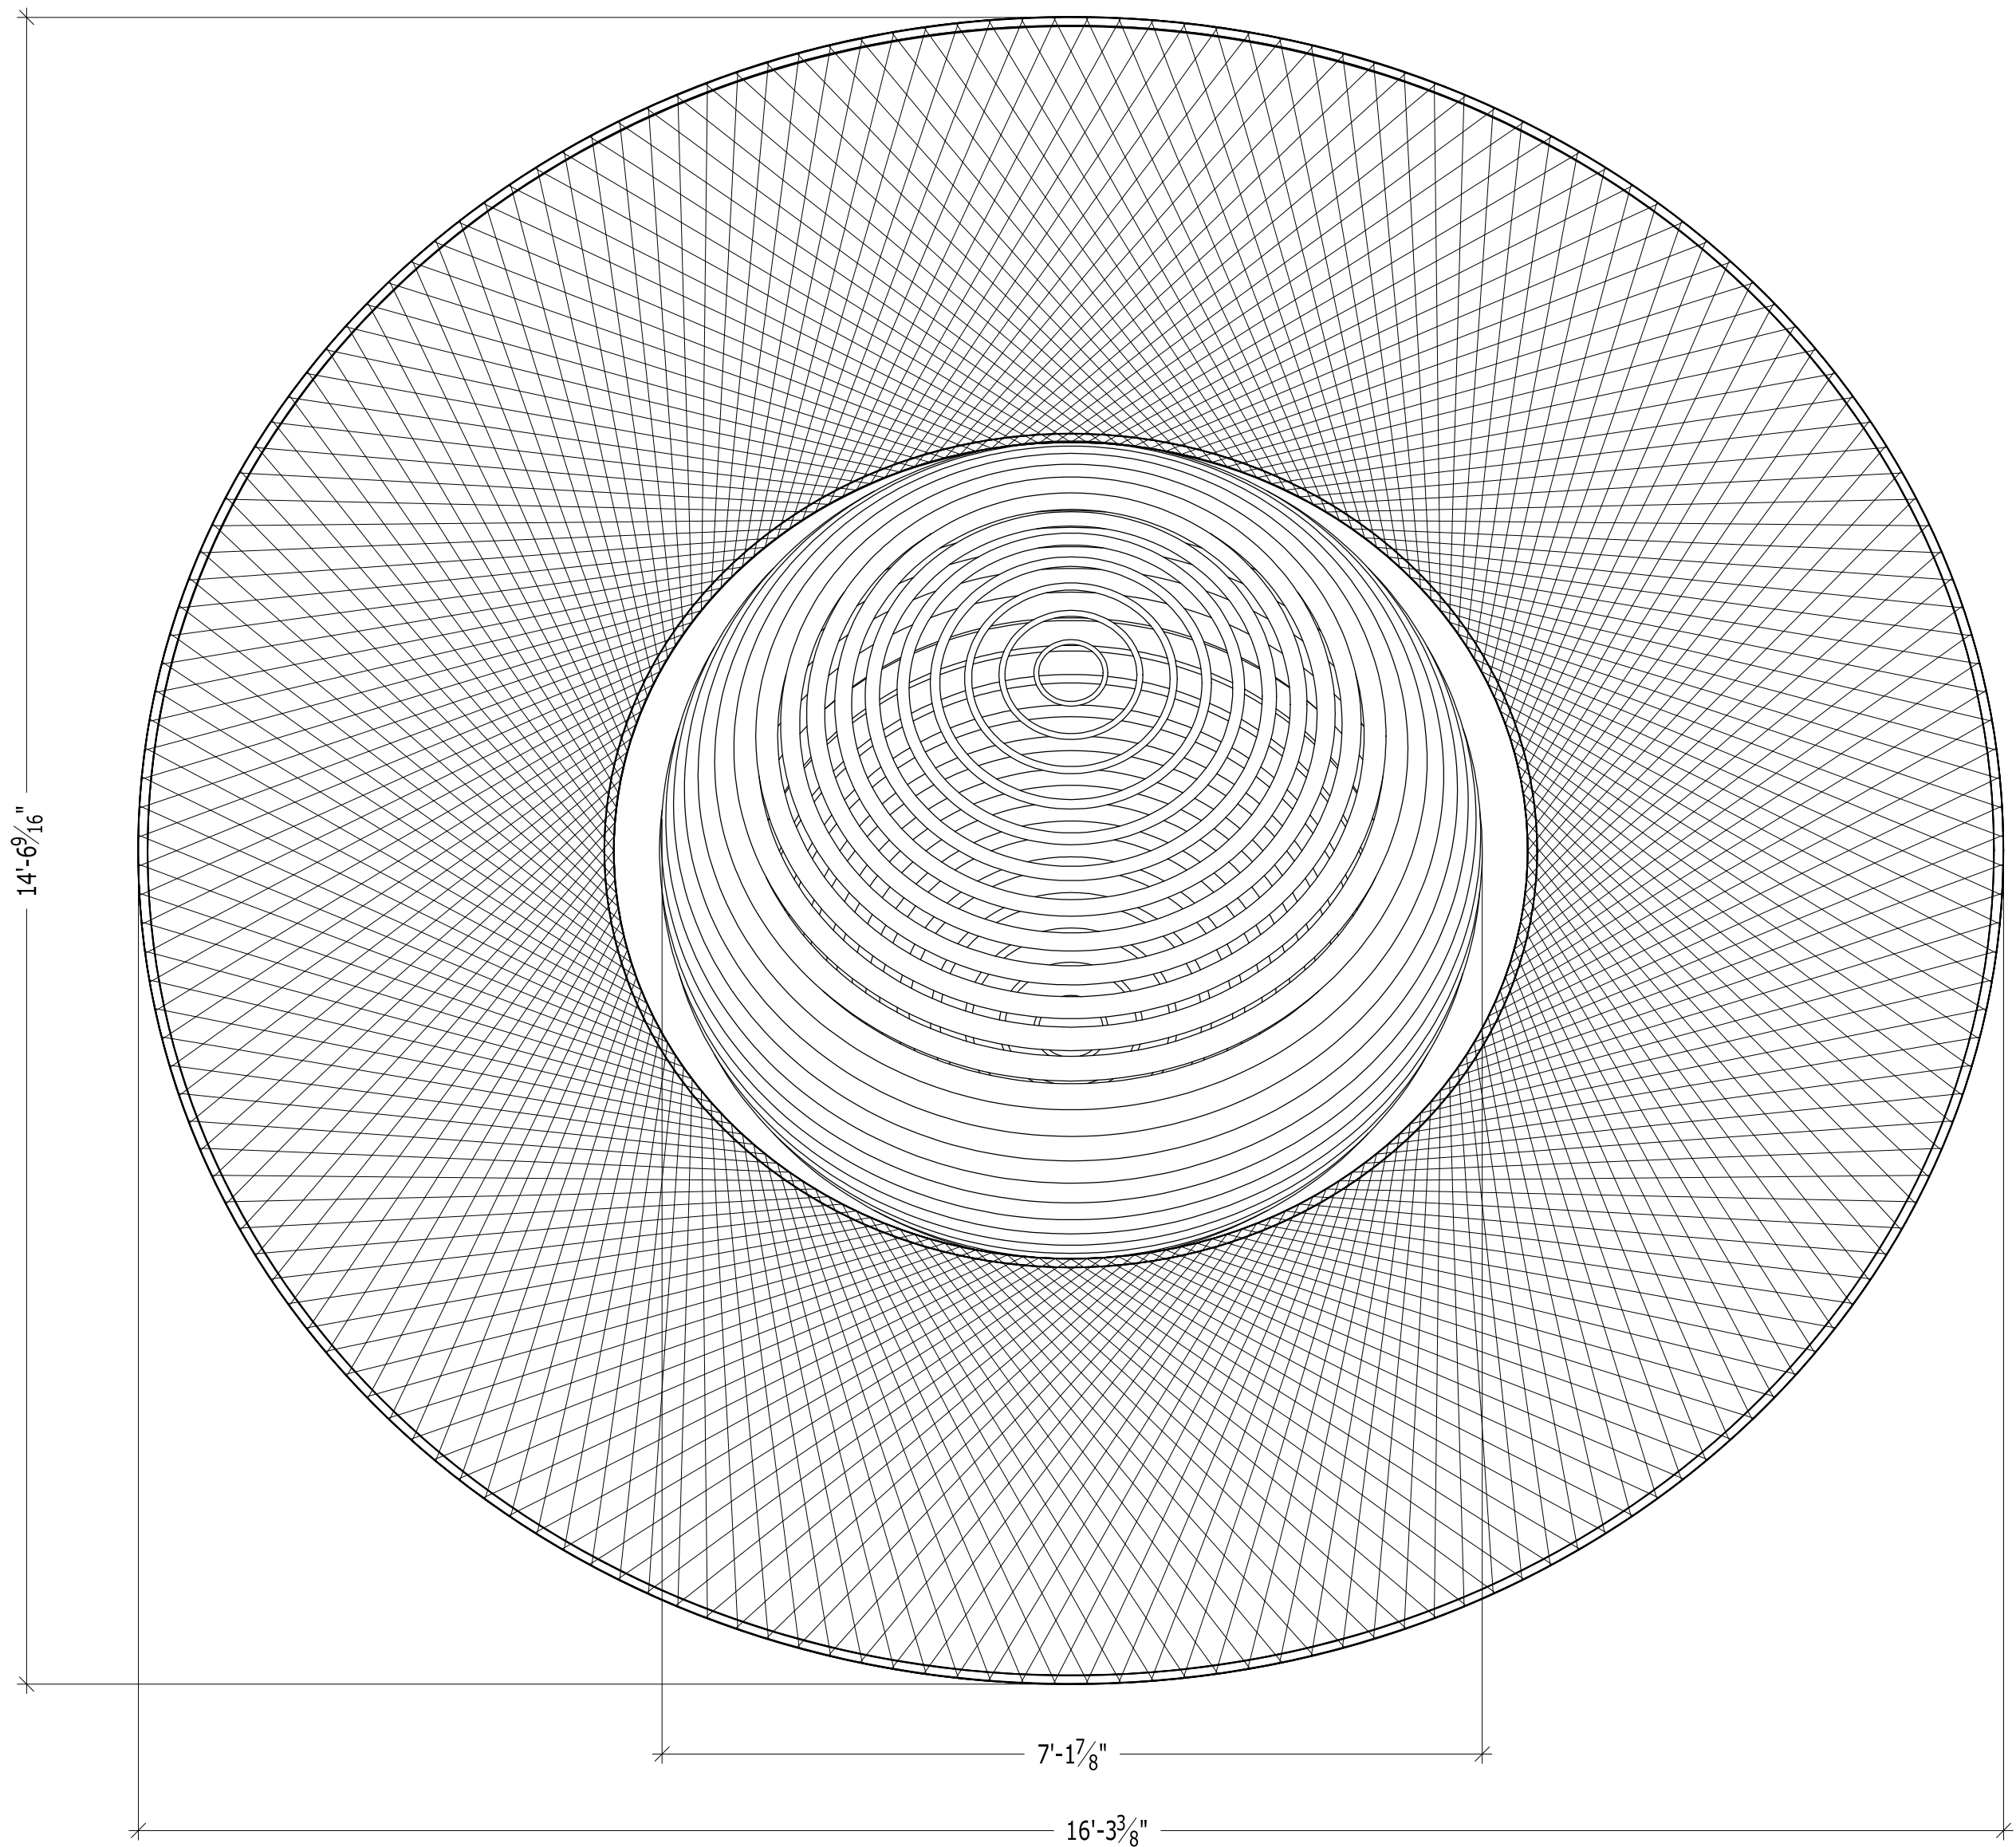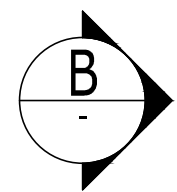

PLAN -
SCALE: 3/4" = 1'-0"

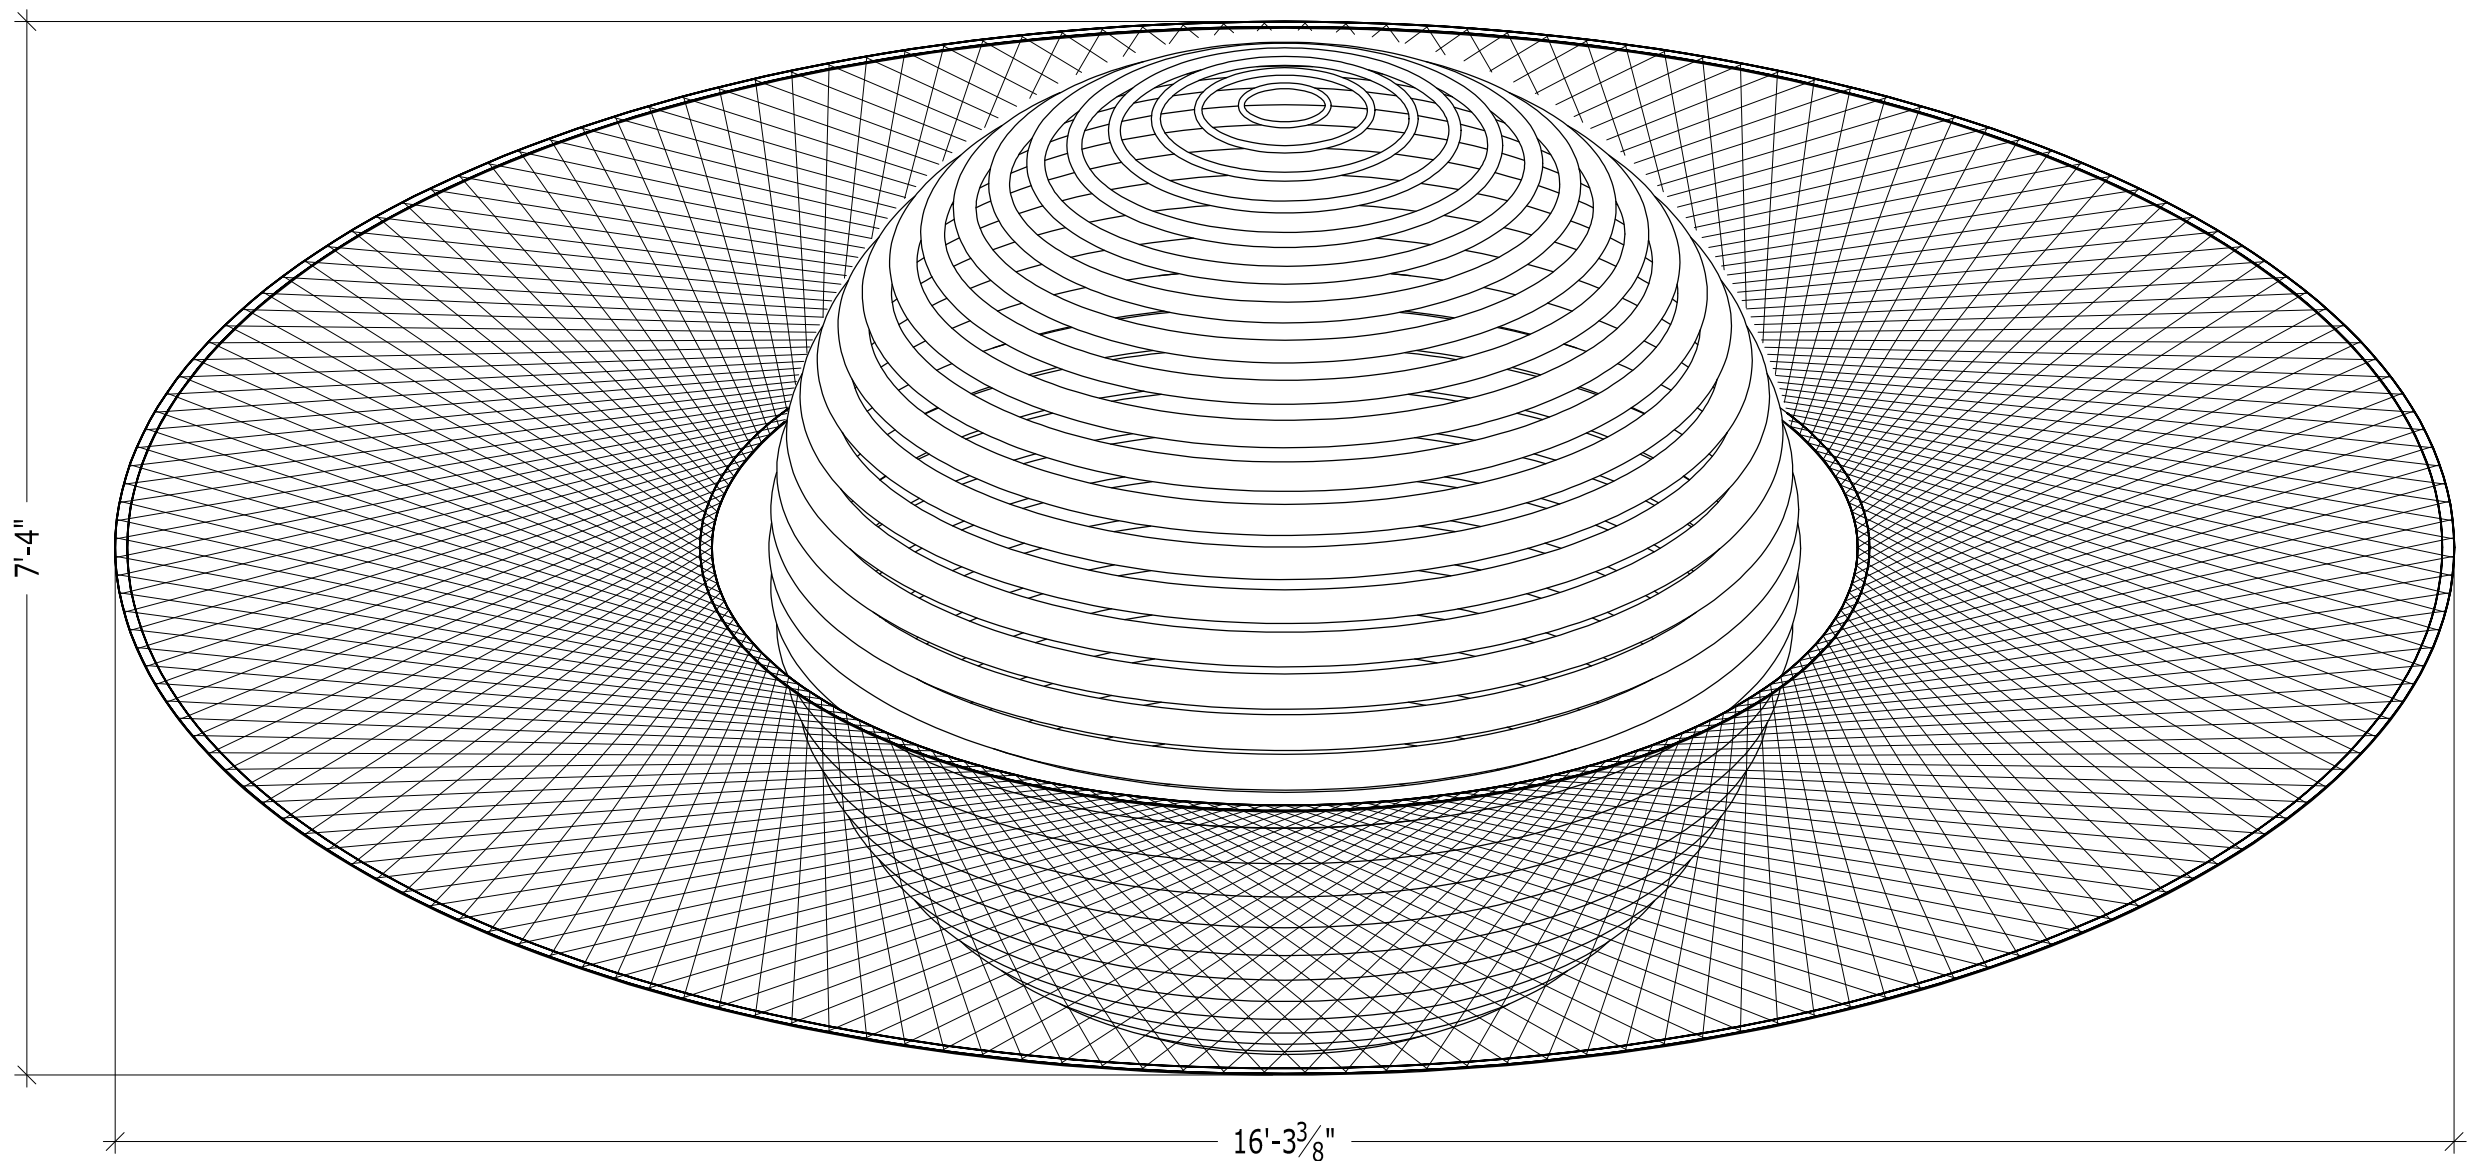

A ELEVATION -
SCALE: 3/4" = 1'-0"

FOR REVIEW

JACK ANDERSON
FABRICATION DESIGN

3326 CAZADOR STREET
LOS ANGELES CA 90065
623-419-4802
jack4congrss@protonmail.com

HOW ARE THE ROLLED
VARYING DIAMETER TUBES
ATTACHED?

LOS ANGELES SOLAR SYSTEM PROJECT

SATURN

2800 E. Observatory Rd
Los Angeles, CA 90027

DRAWN BY
JACK


DRAWING DATE
2-5-2026

REVISION DATE
--/--/----


TITLE
FAB DETAILS

SCALE
AS NOTED


SHEET
SA600

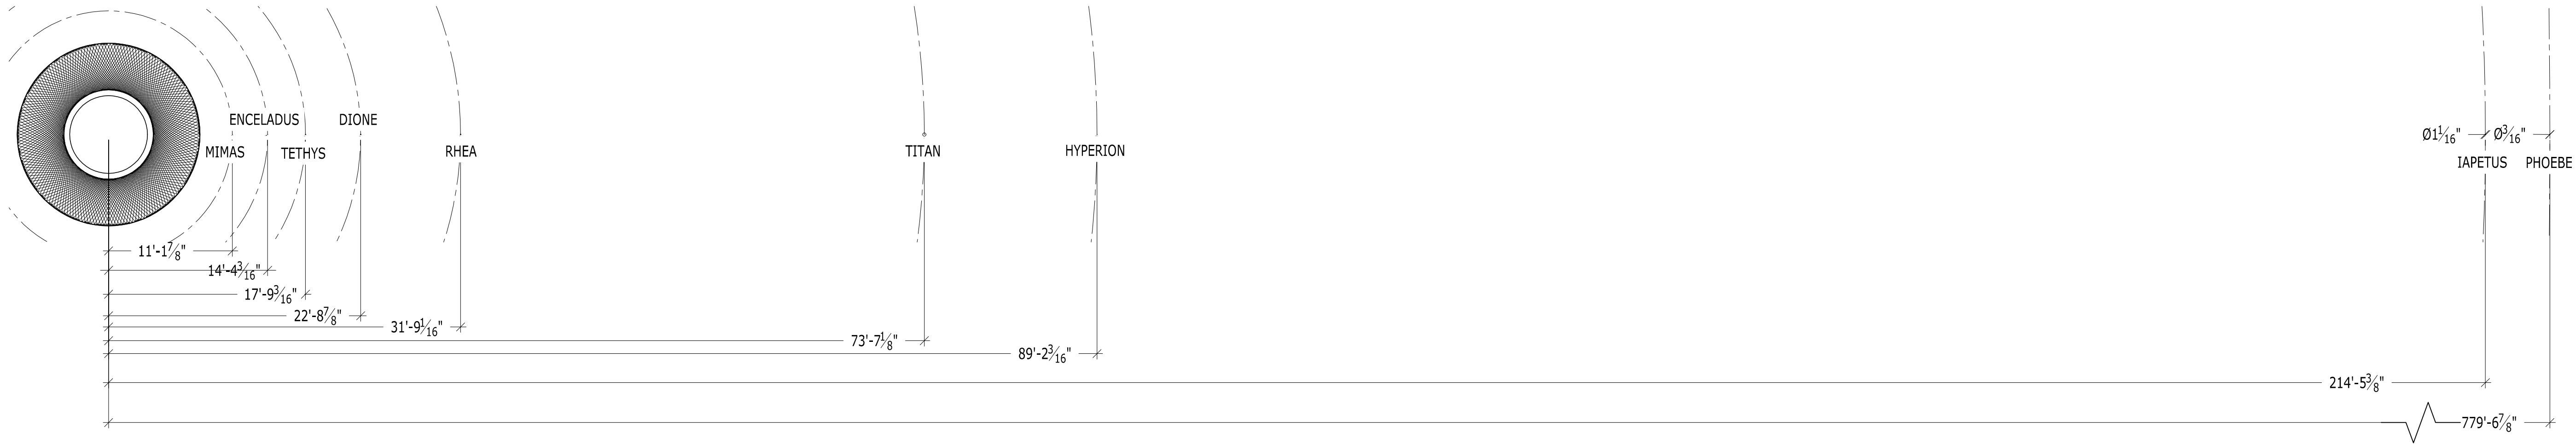

PLAN -
SCALE: 1/8" = 1'-0"

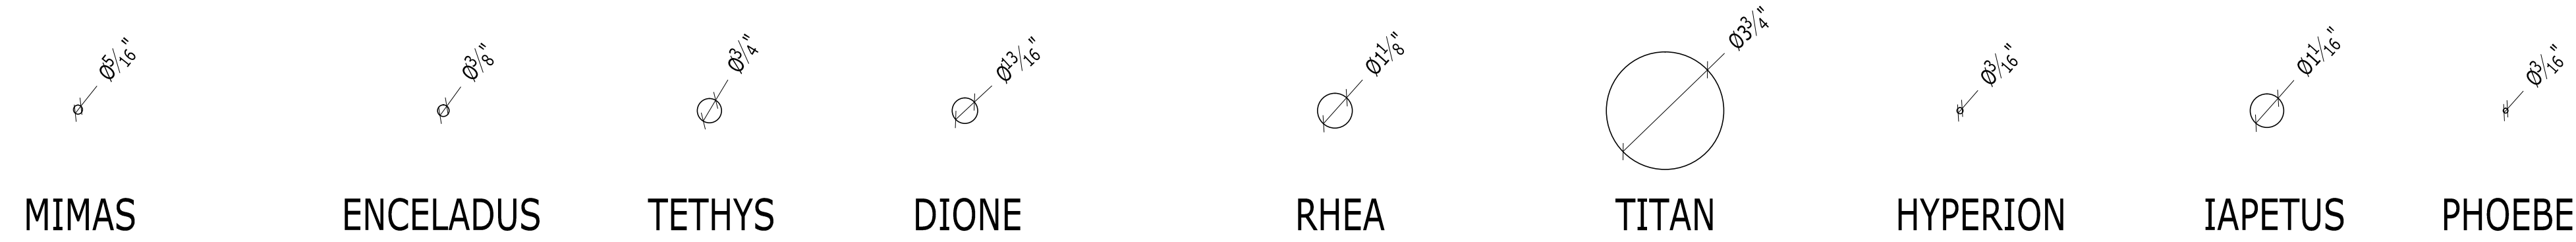

A ELEVATION - MOONS
SCALE: 3" = 1'-0"

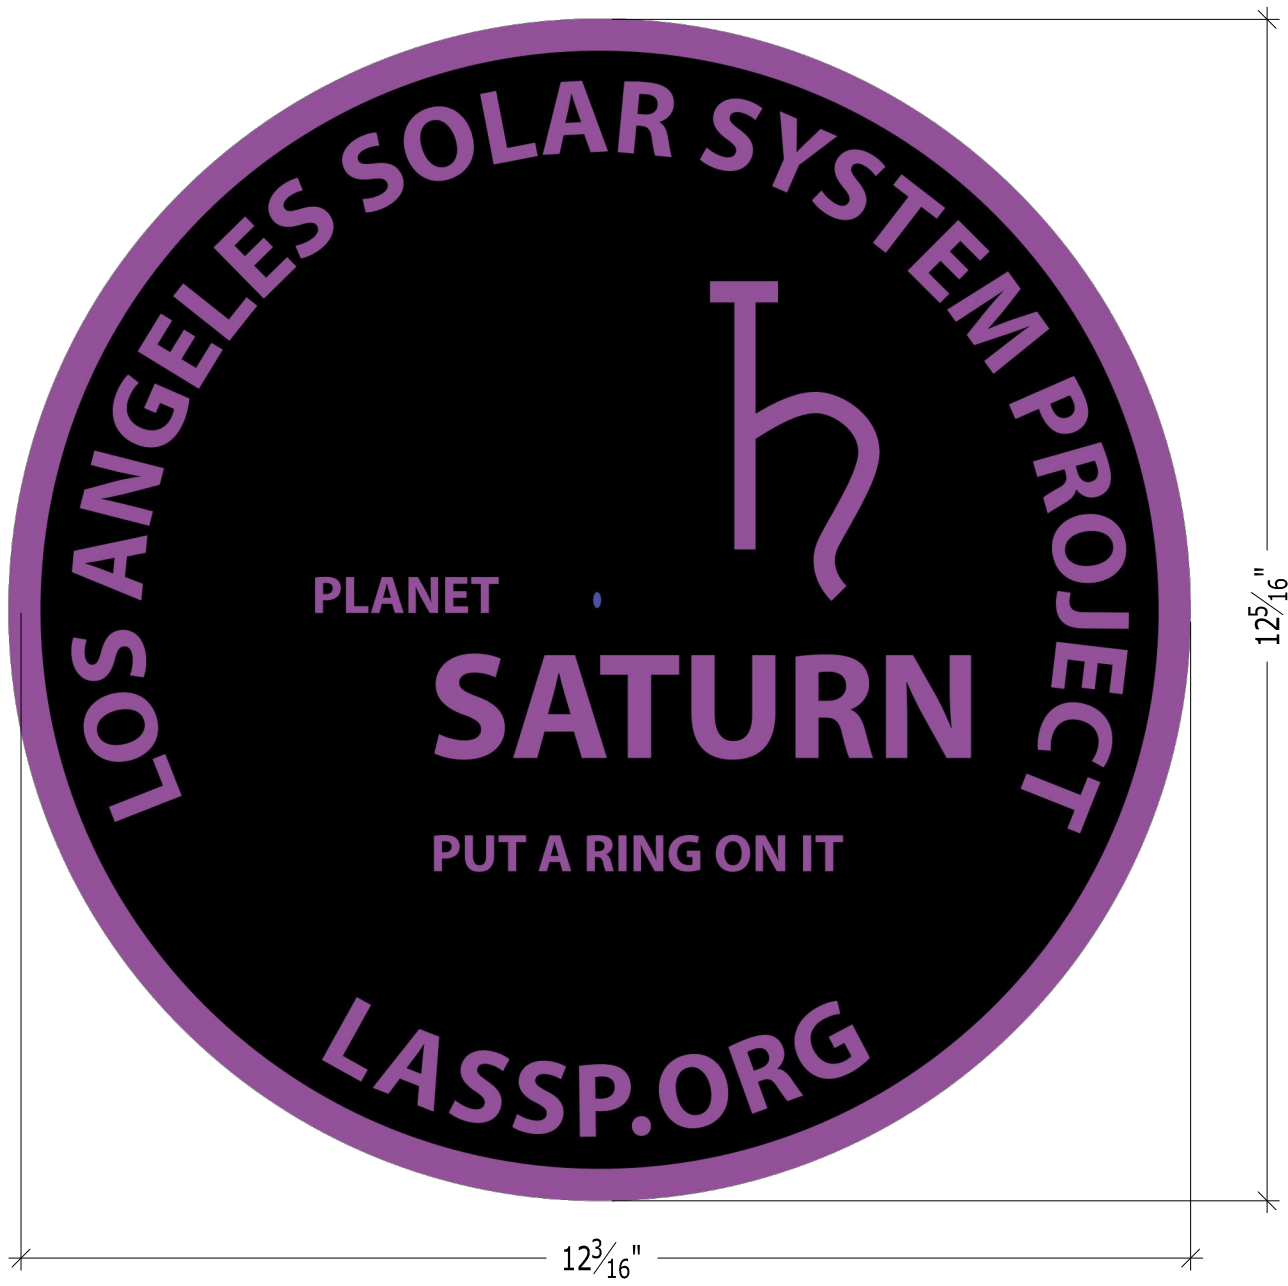

B ELEVATION - COMPANION GRAPHIC
SCALE: HALF SCALE

JACK ANDERSON
FABRICATION DESIGN
3326 CAZADOR STREET
LOS ANGELES CA 90065
623-419-4802
jack4congrss@protonmail.com

LOS ANGELES SOLAR SYSTEM PROJECT
SATURN MOONS
2800 E. Observatory Rd
Los Angeles, CA 90027

DRAWN BY
JACK

DRAWING DATE
2-5-2026


REVISION DATE
--/------

TITLE
FAB DETAILS



SCALE
AS NOTED

SHEET
SA601

FOR REVIEW

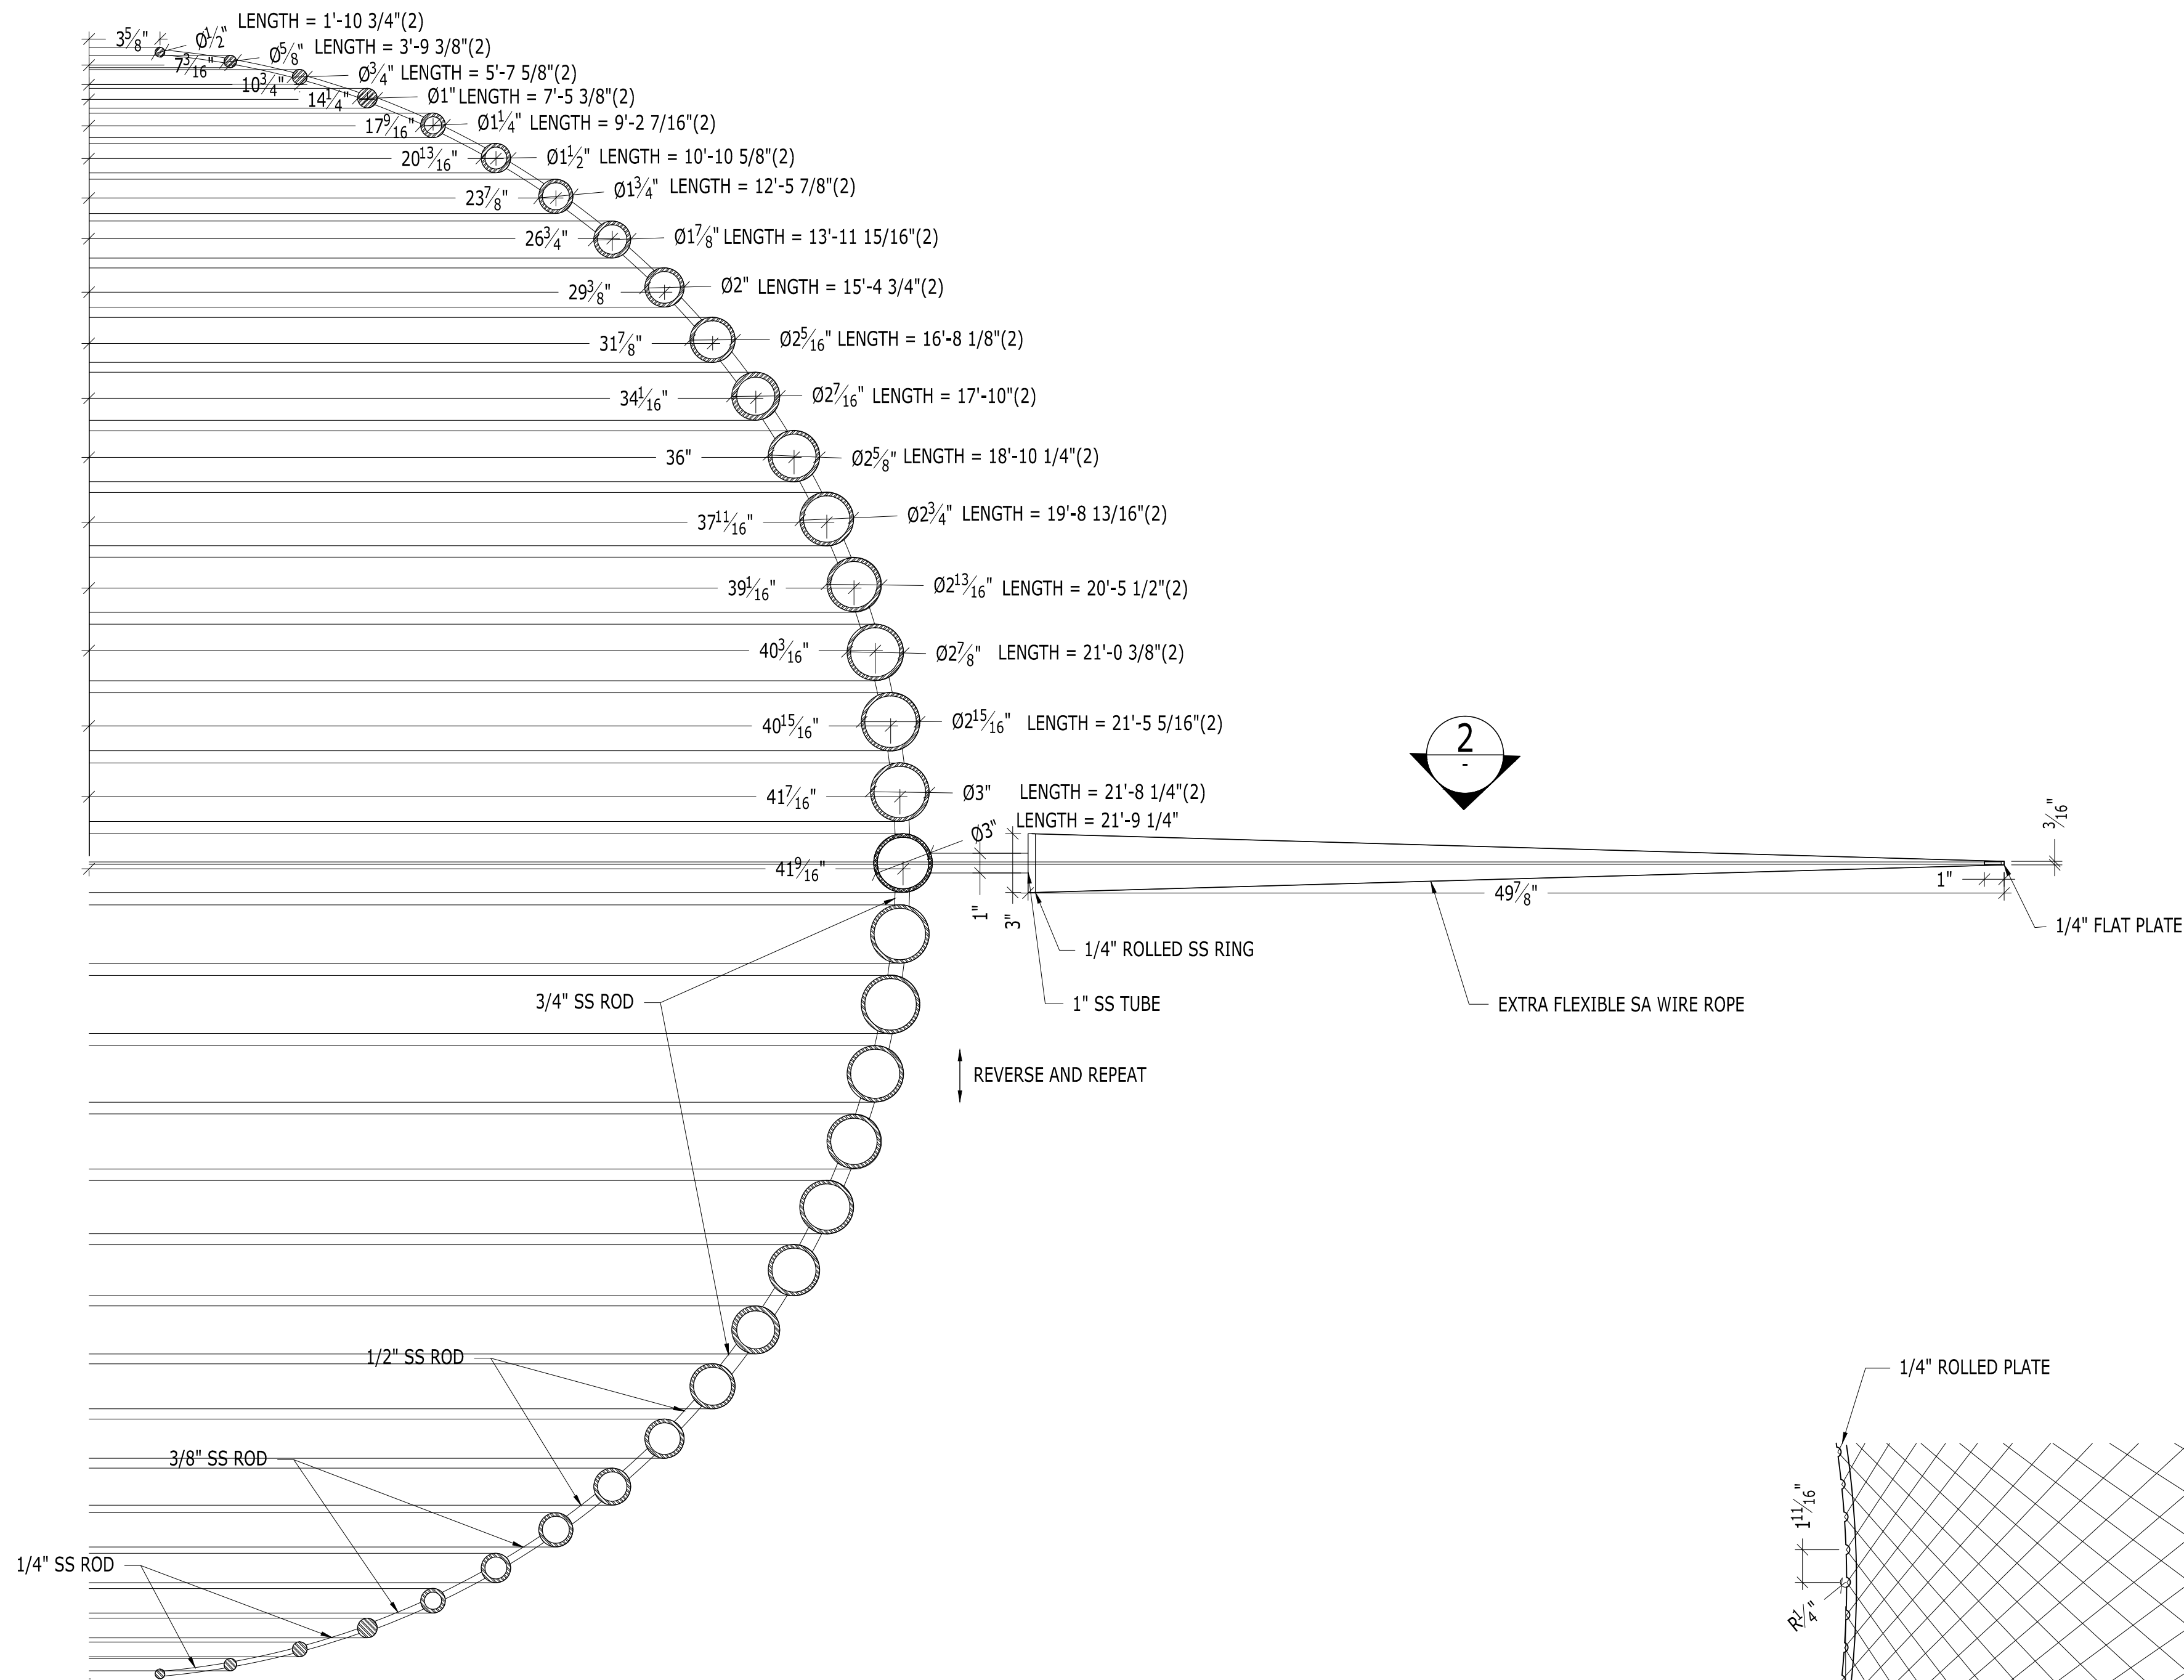

1 SECTION -
SCALE: 2" = 1'-0"

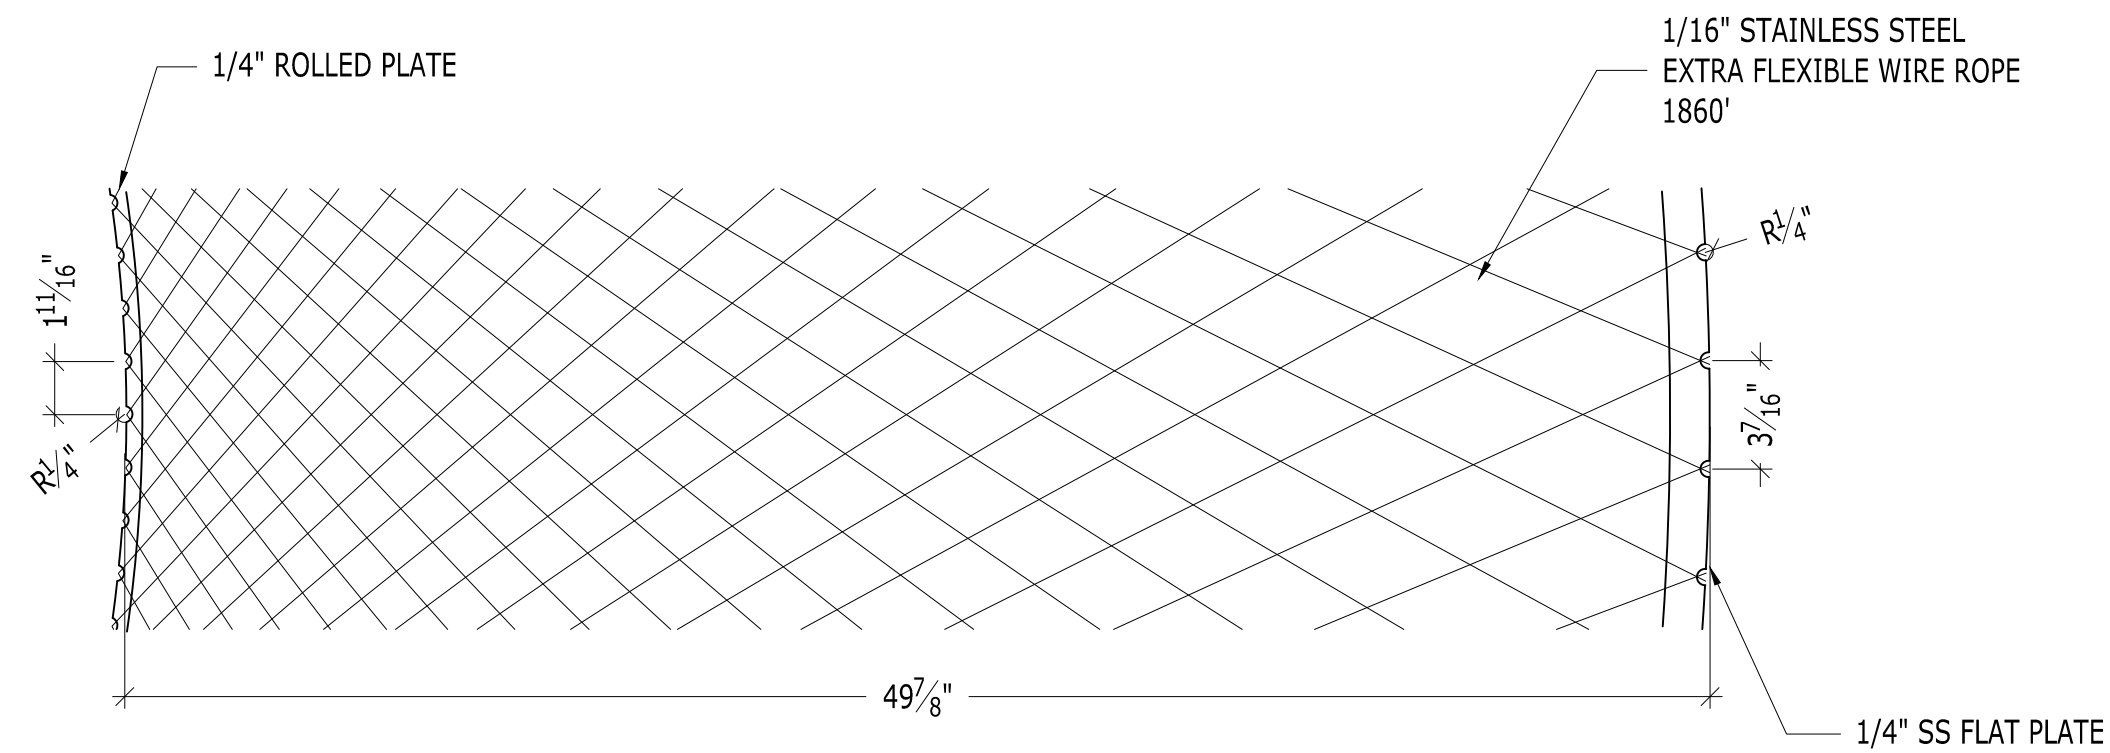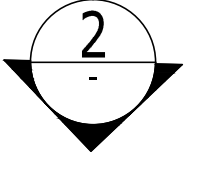


2 DETAIL - WIRE LACE
SCALE: 2" = 1'-0"

FOR REVIEW


JACK ANDERSON
FABRICATION DESIGN
3326 CAZADOR STREET
LOS ANGELES CA 90065
623-419-4802
jack4congrss@protonmail.com

LOS ANGELES SOLAR SYSTEM PROJECT
SATURN DETAILS
2800 E. Observatory Rd
Los Angeles, CA 90027


DRAWN BY	JACK
DRAWING DATE	2-5-2026
REVISION DATE	--/--/----
TITLE	FAB DETAILS
SCALE	AS NOTED
SHEET	SA602

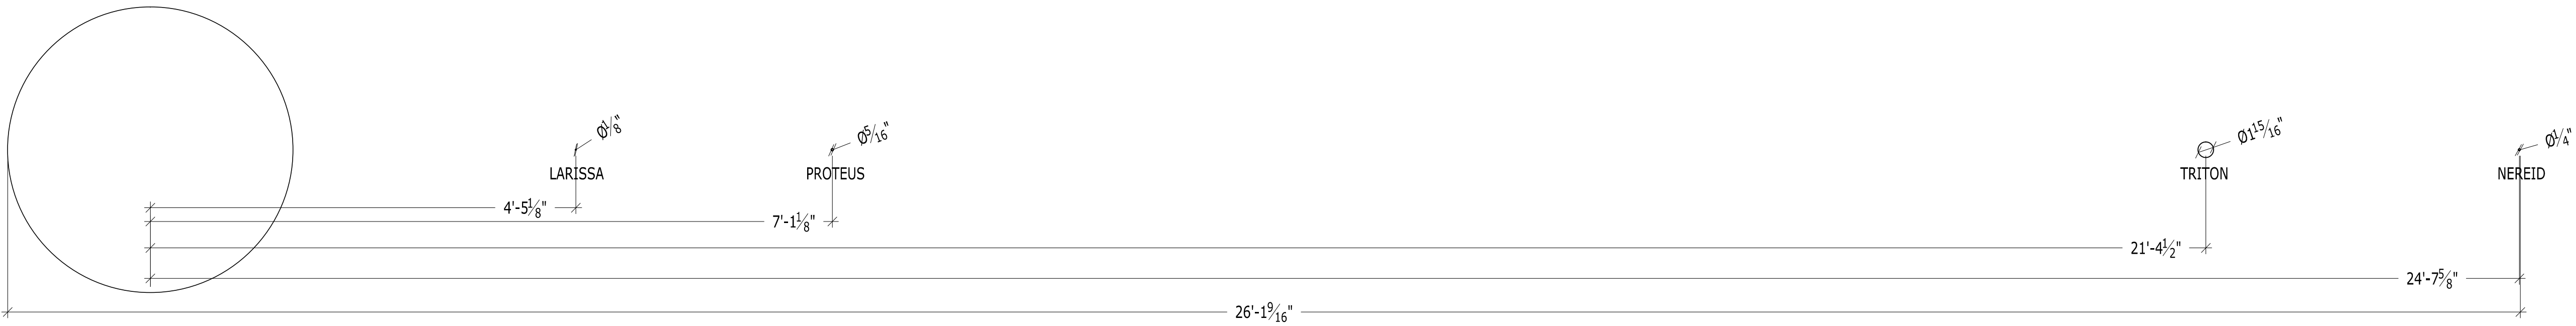


PLAN -
SCALE: 1" = 1'-0"

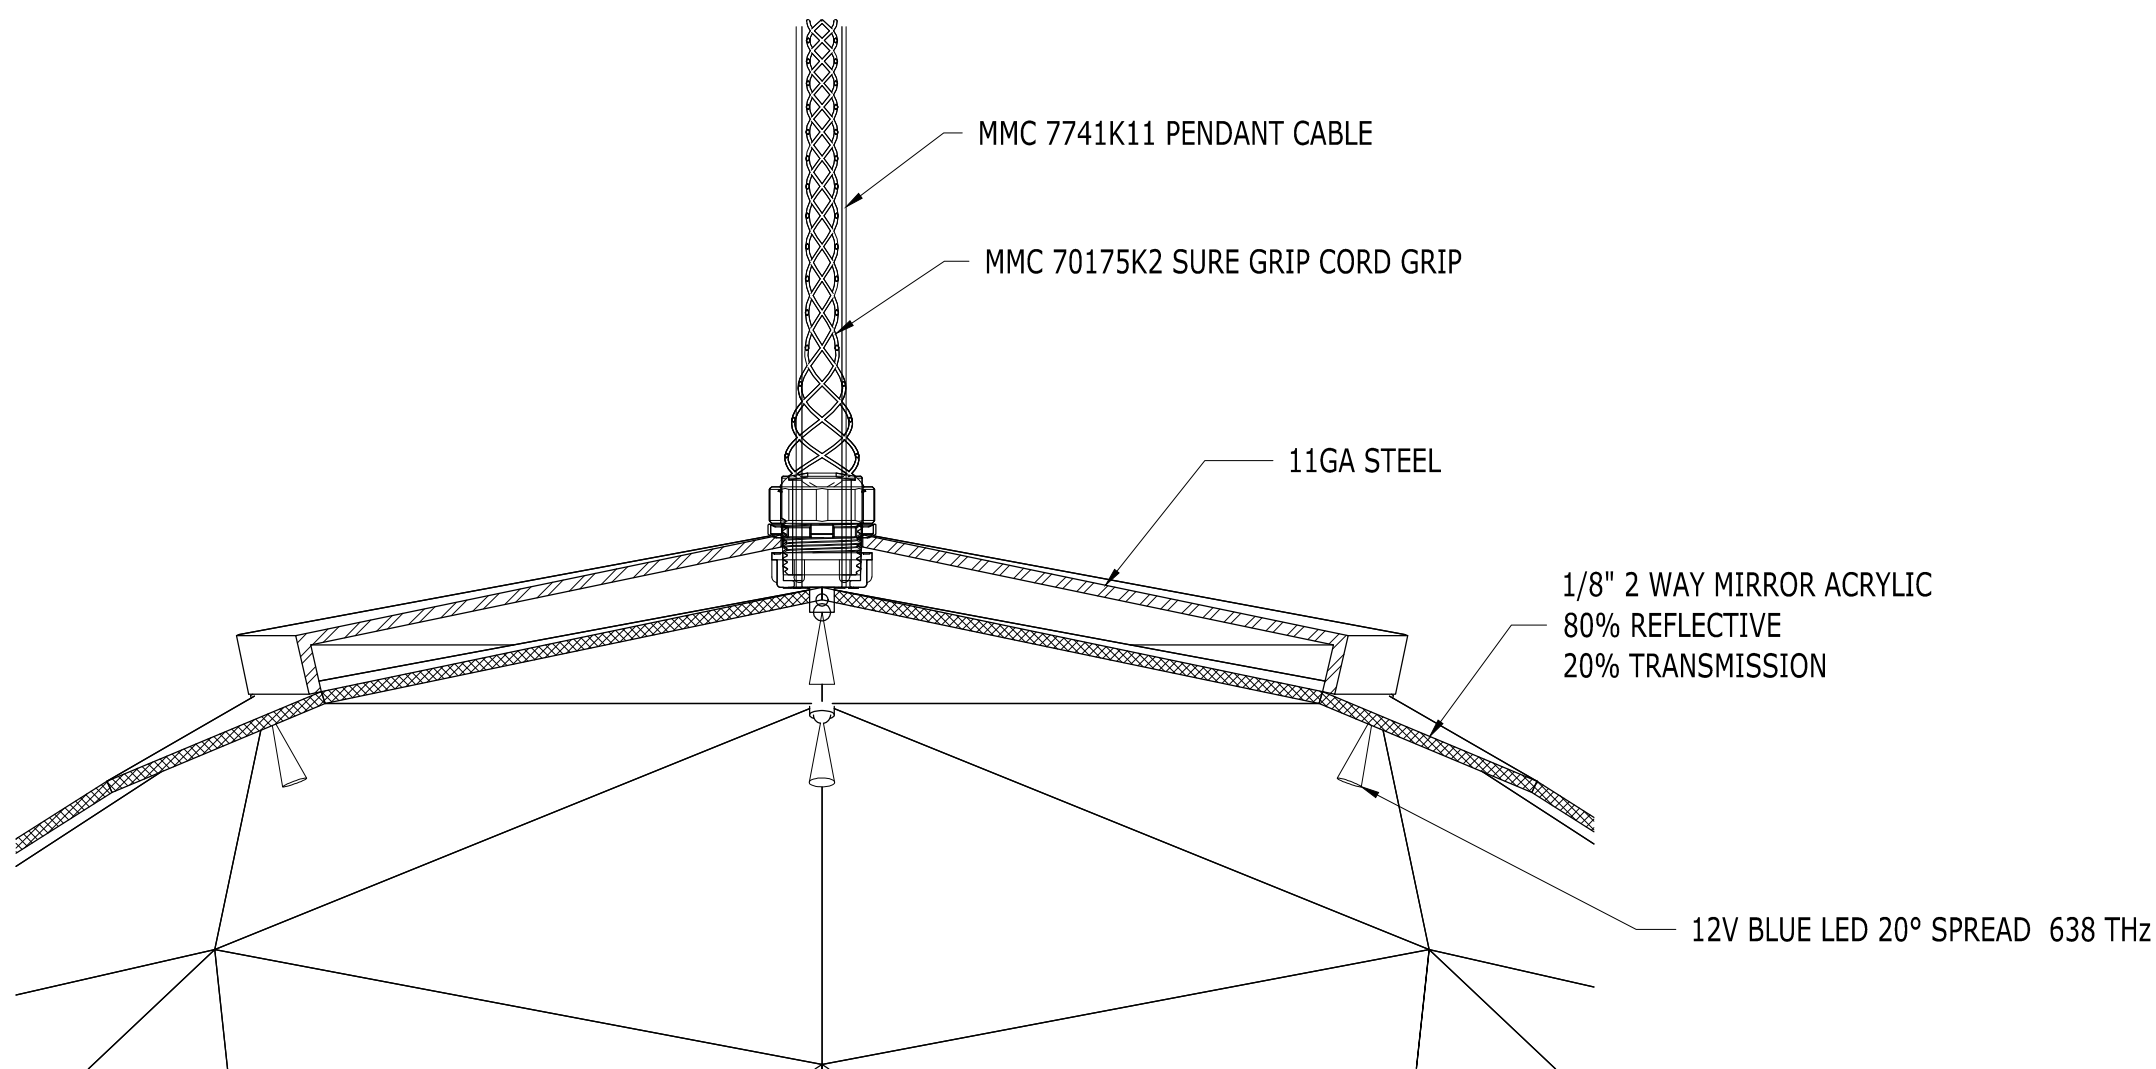


1 SECTION - DETAIL
SCALE: HALF SCALE

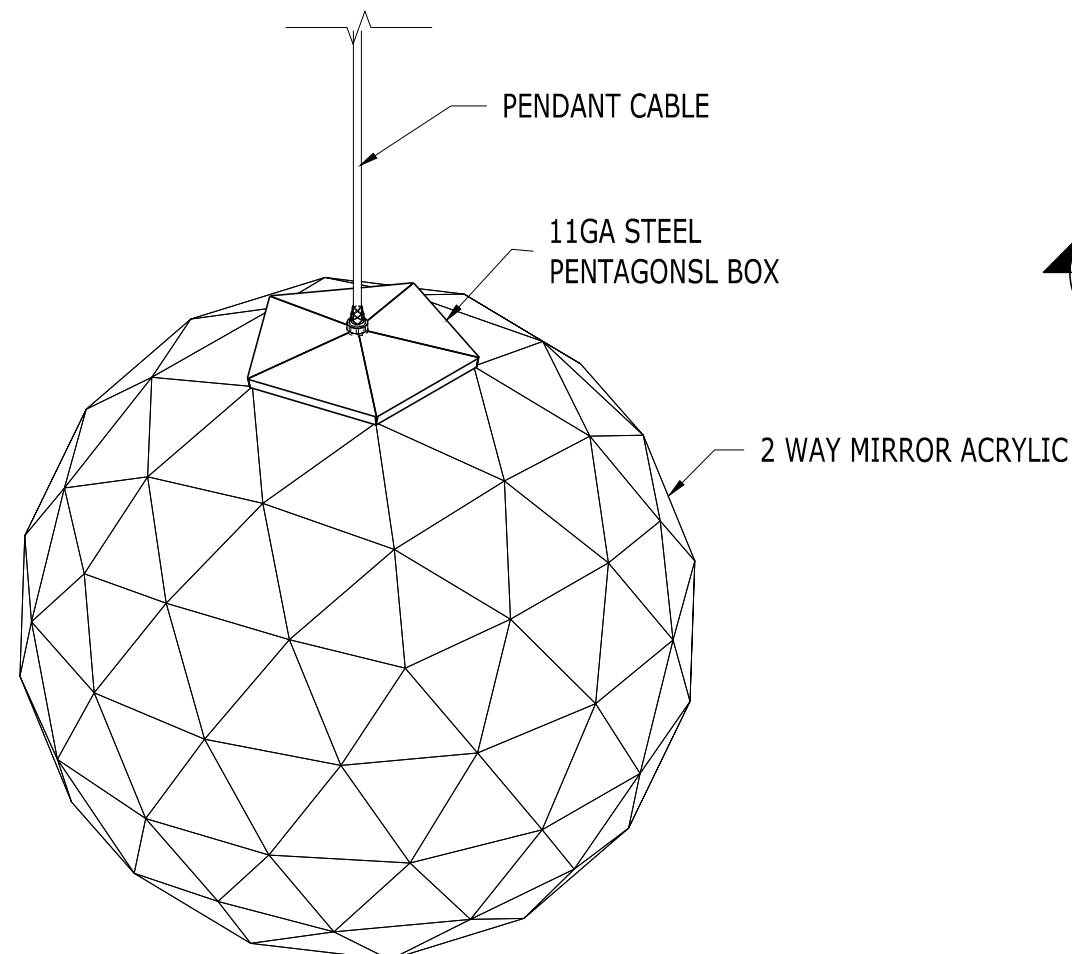

ISO VIEW
NTS

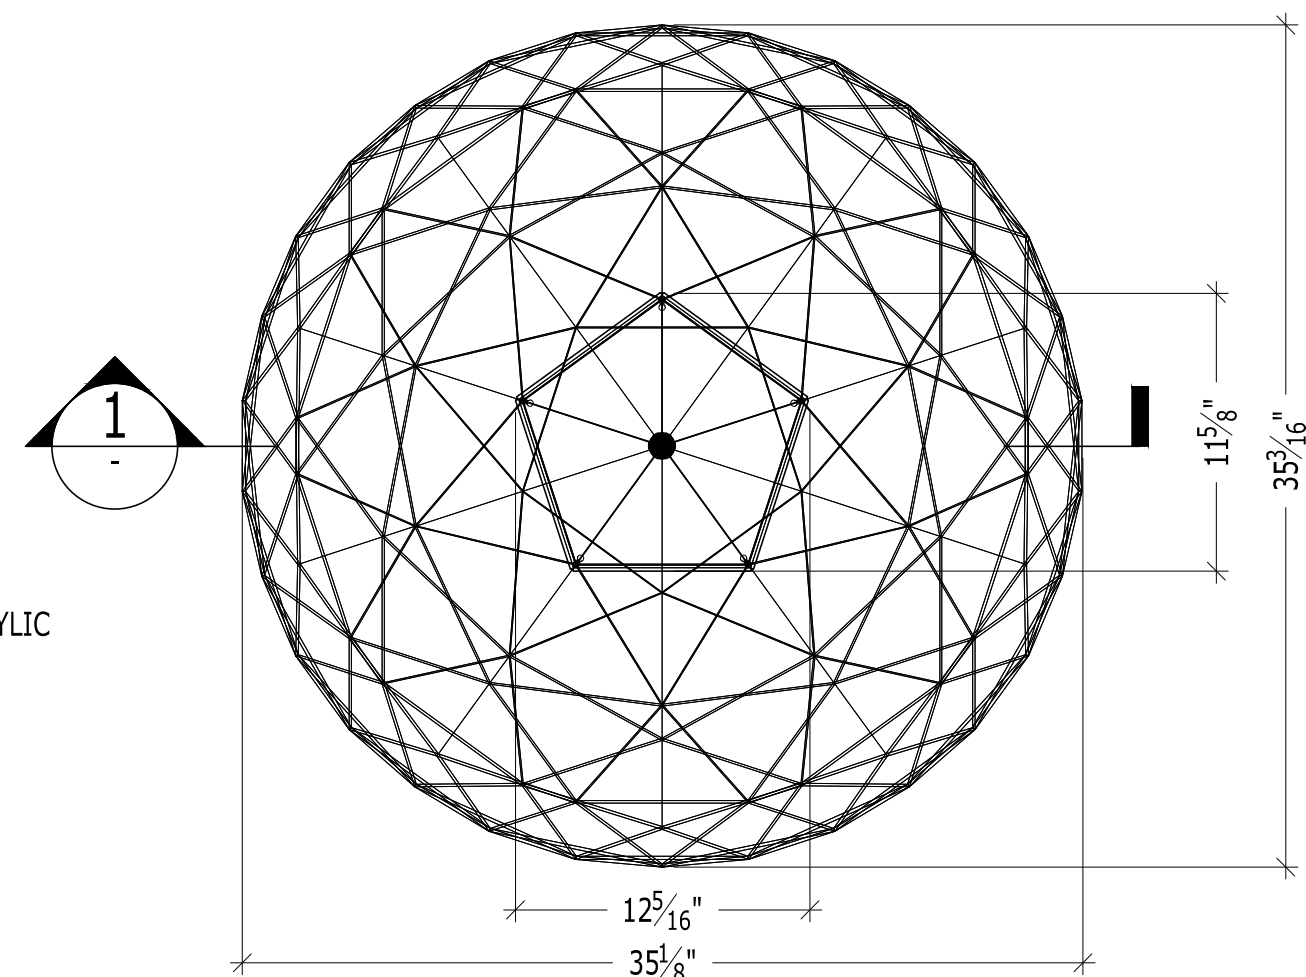

TOP
SCALE: 1-1/2" = 1'-0"

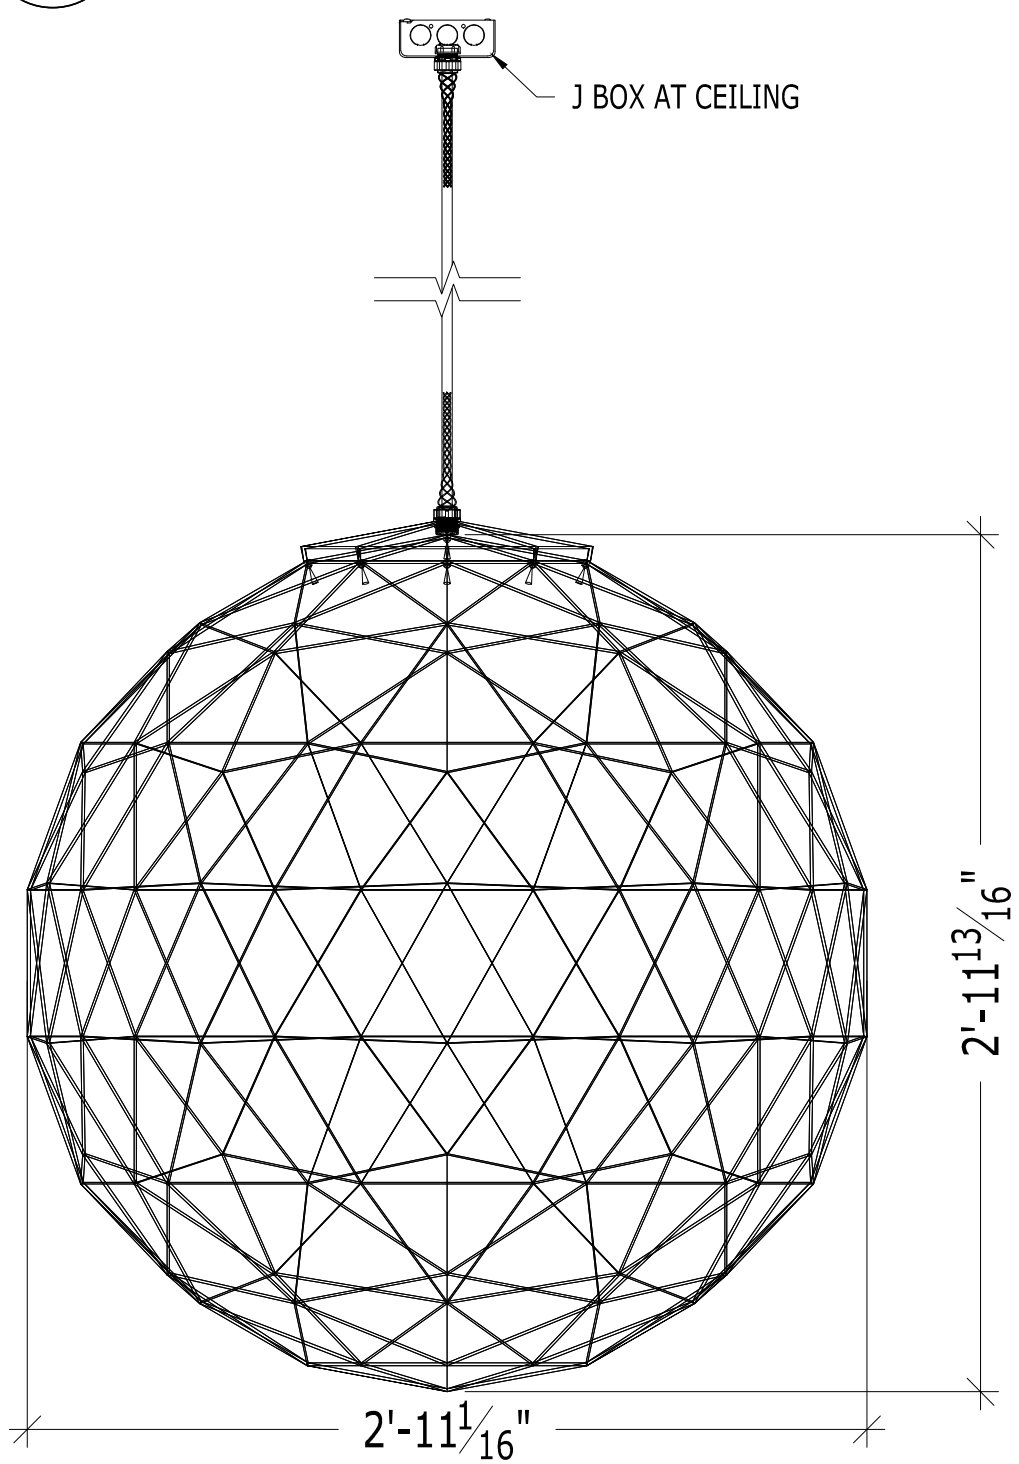

A ELEVATION -
SCALE: 1-1/2" = 1'-0"

FOR REVIEW



C ELEVATION - COMPANION GRAPHIC
SCALE: HALF SCALE

JACK ANDERSON
FABRICATION DESIGN

3326 CAZADOR STREET
LOS ANGELES CA 90065
623-419-4802
jack4congrss@protonmail.com

LOS ANGELES SOLAR SYSTEM PROJECT

NEPTUNE

2800 E. Observatory Rd
Los Angeles, CA 90027

DRAWN BY
JACK


DRAWING DATE
2-5-2026

REVISION DATE
--/--/----


TITLE
FAB DETAILS

SCALE
AS NOTED


SHEET
NE801

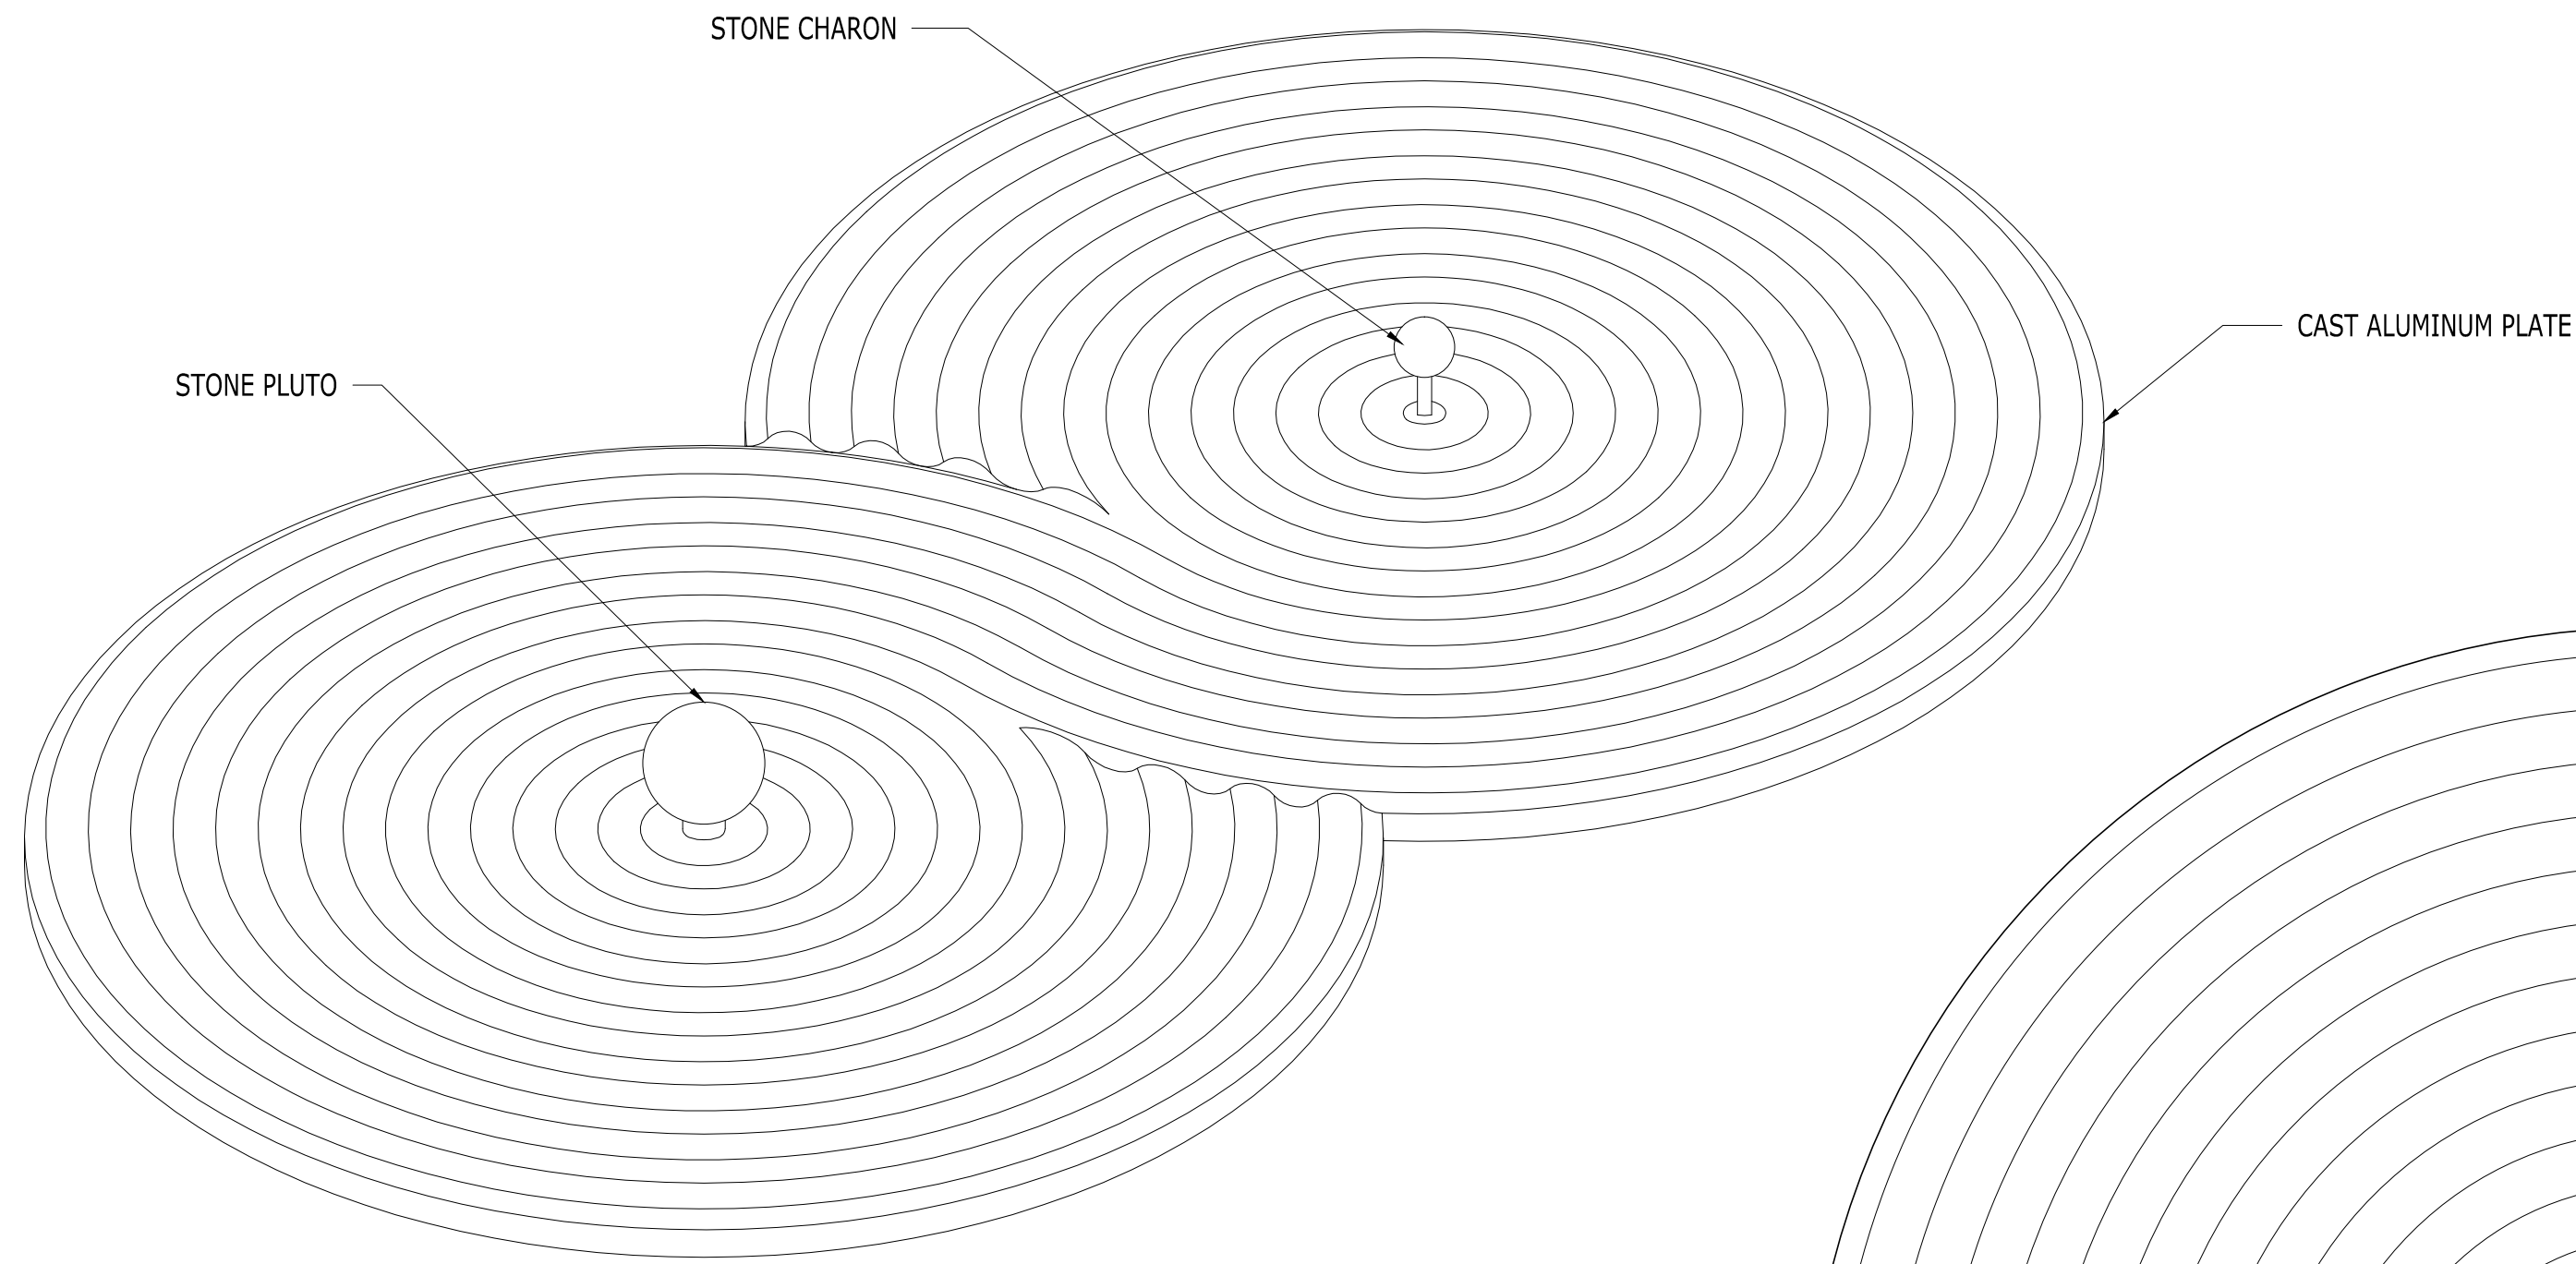


ISO VIEW
NTS

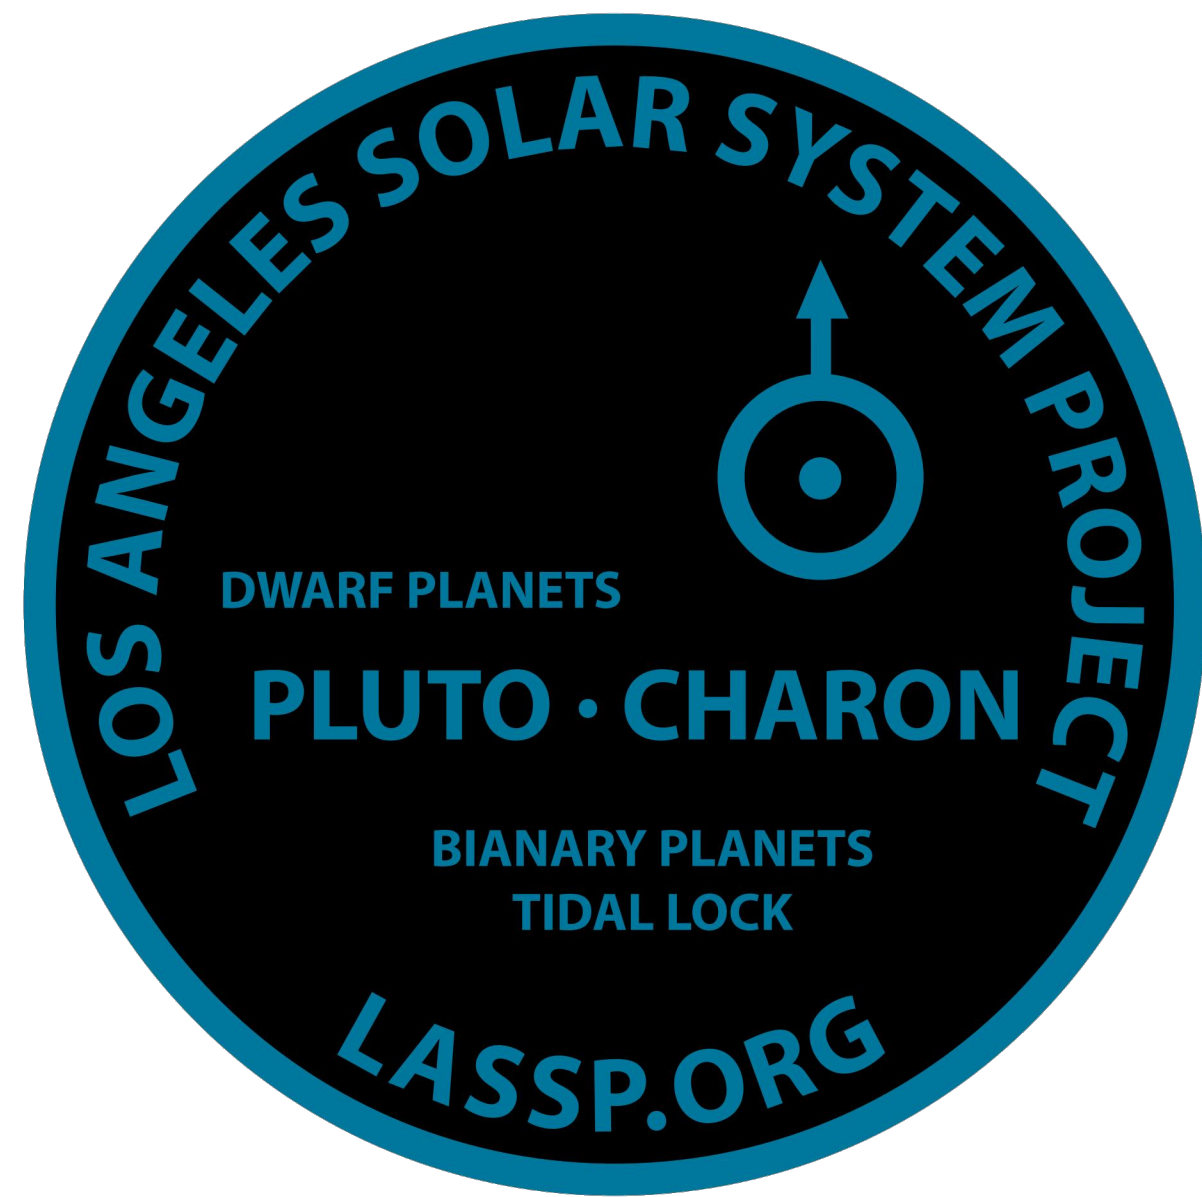

B ELEVATION - COMPANION GRAPHIC
SCALE: HALF SCALE

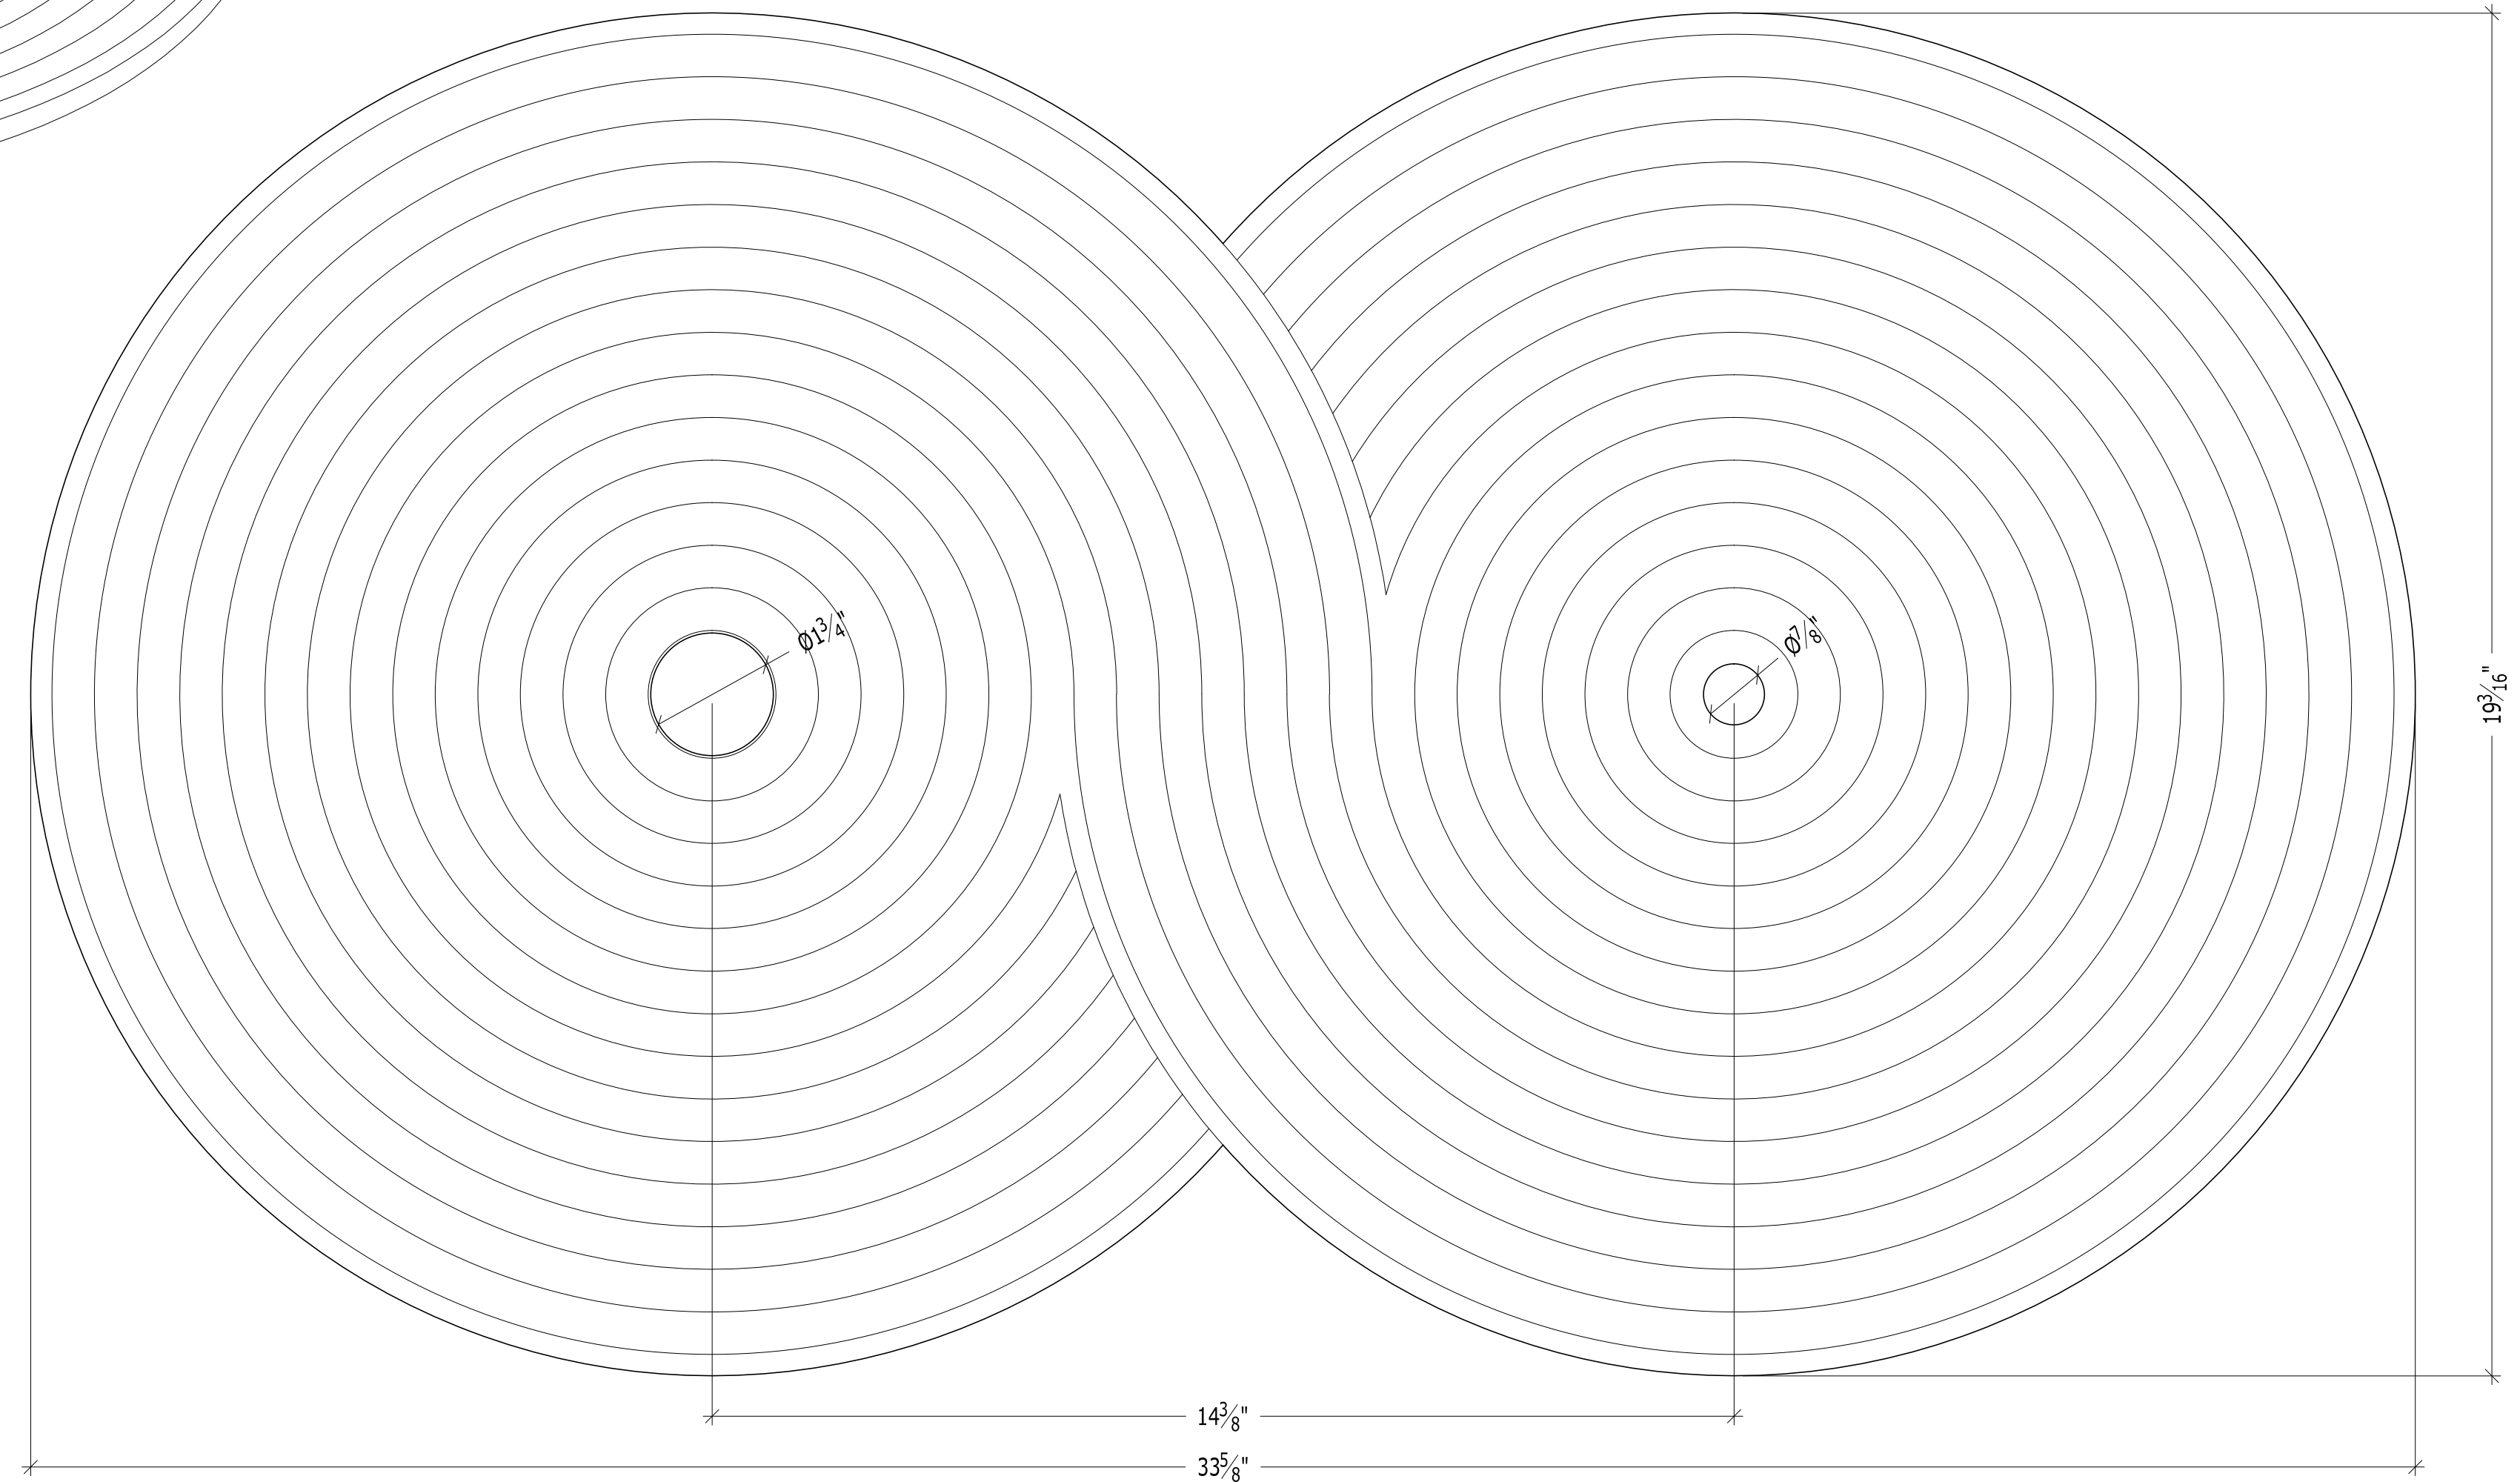

PLAN -
SCALE: HALF SCALE

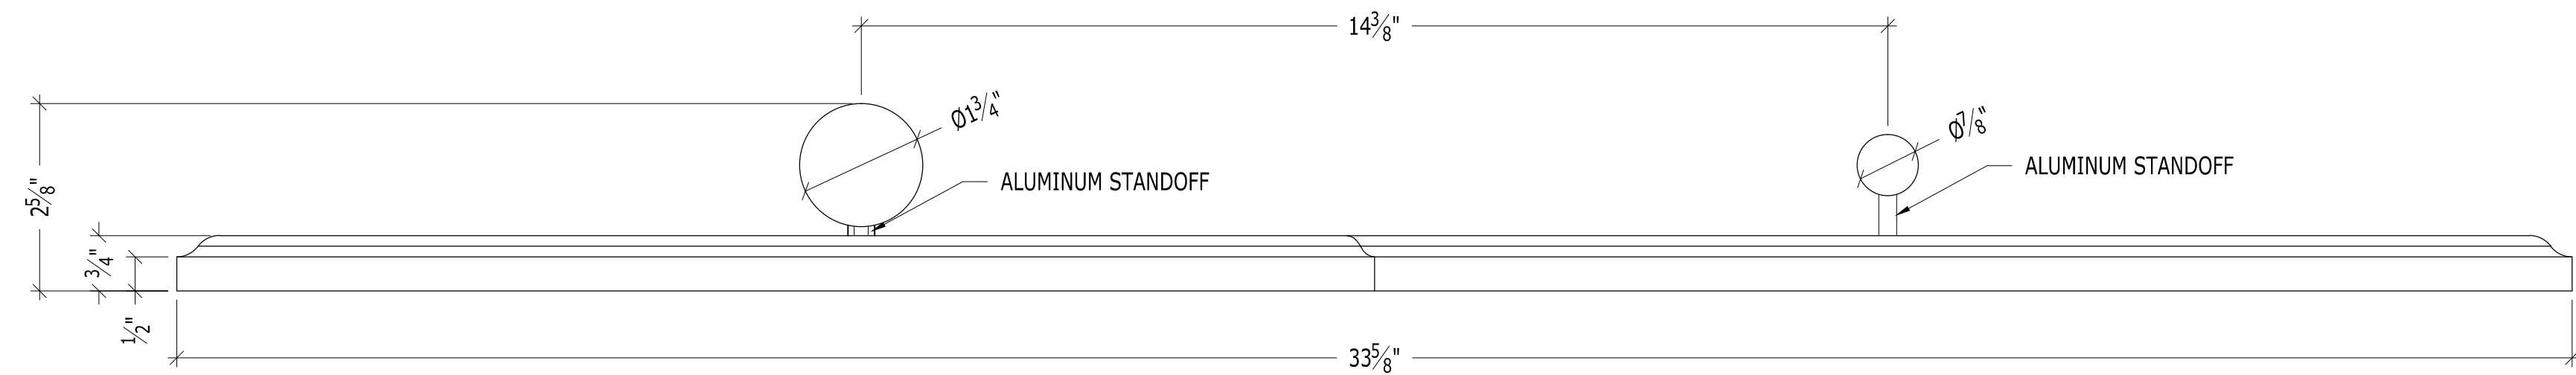


A ELEVATION -
SCALE: HALF SCALE

FOR REVIEW

JACK ANDERSON
FABRICATION DESIGN
3326 CAZADOR STREET
LOS ANGELES CA 90065
623-419-4802
jack4congrss@protonmail.com

LOS ANGELES SOLAR SYSTEM PROJECT
PLUTO CHARON
2800 E. Observatory Rd
Los Angeles, CA 90027


DRAWN BY
JACK
DRAWING DATE
2-5-2026
REVISION DATE
--/--/----
TITLE
FAB DETAILS
SCALE
AS NOTED
SHEET
PC901

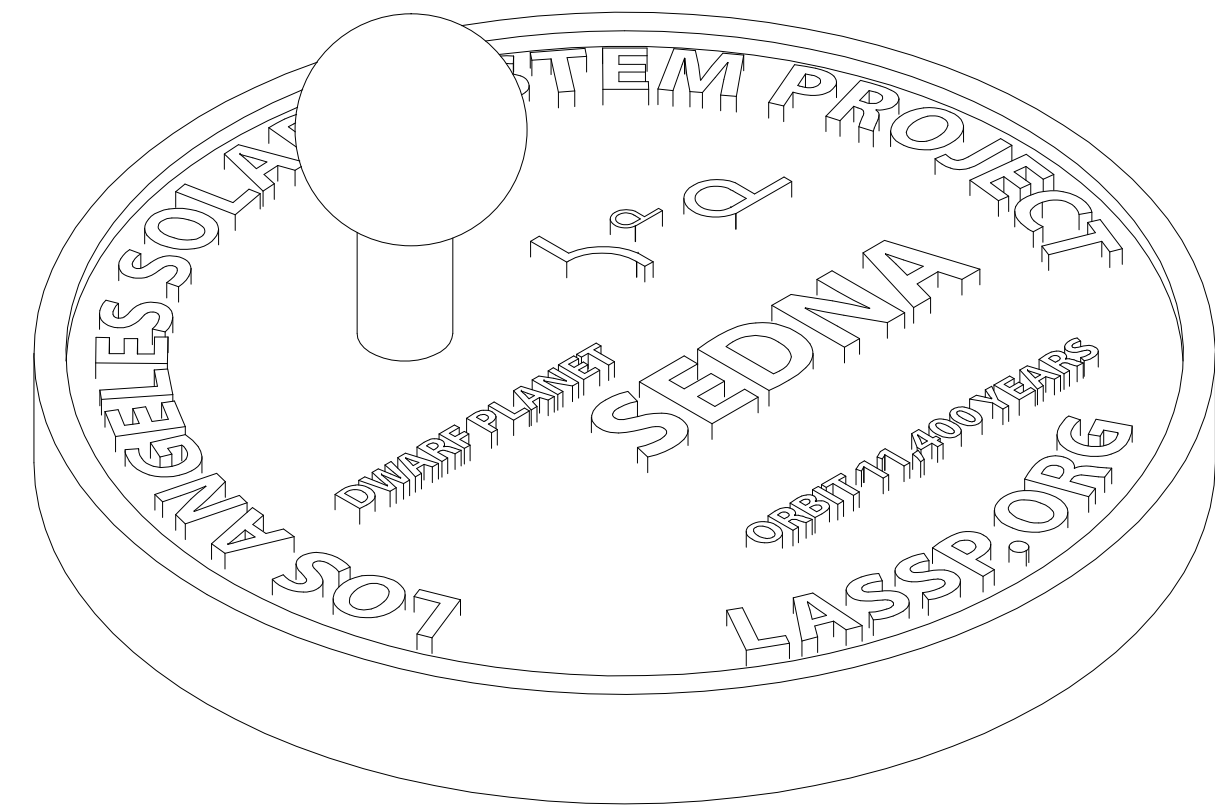


ISO VIEW
NTS




2" #10 PHSMS
SECURE TO STUD

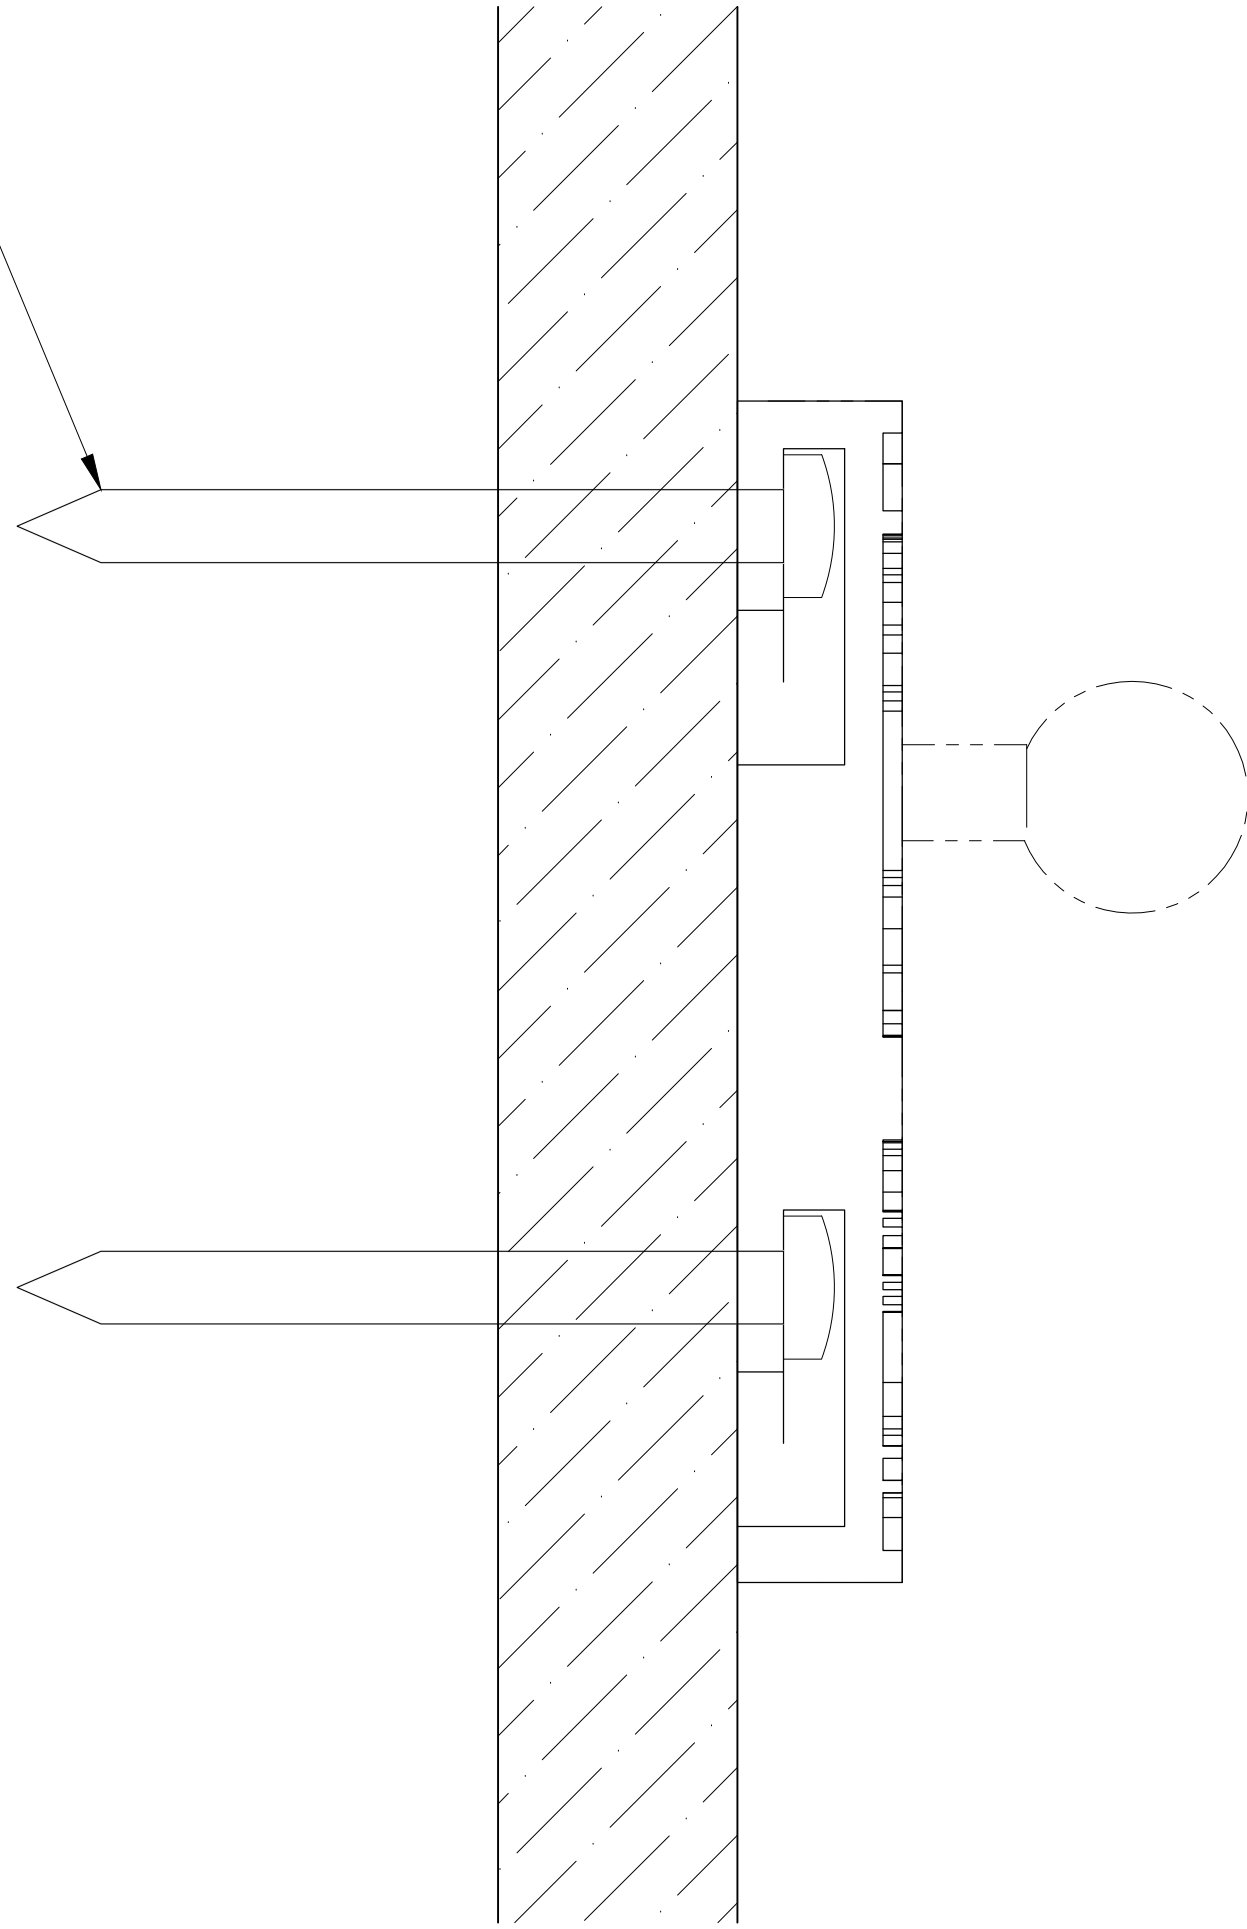

1 SECTION -
SCALE: FULL SCALE

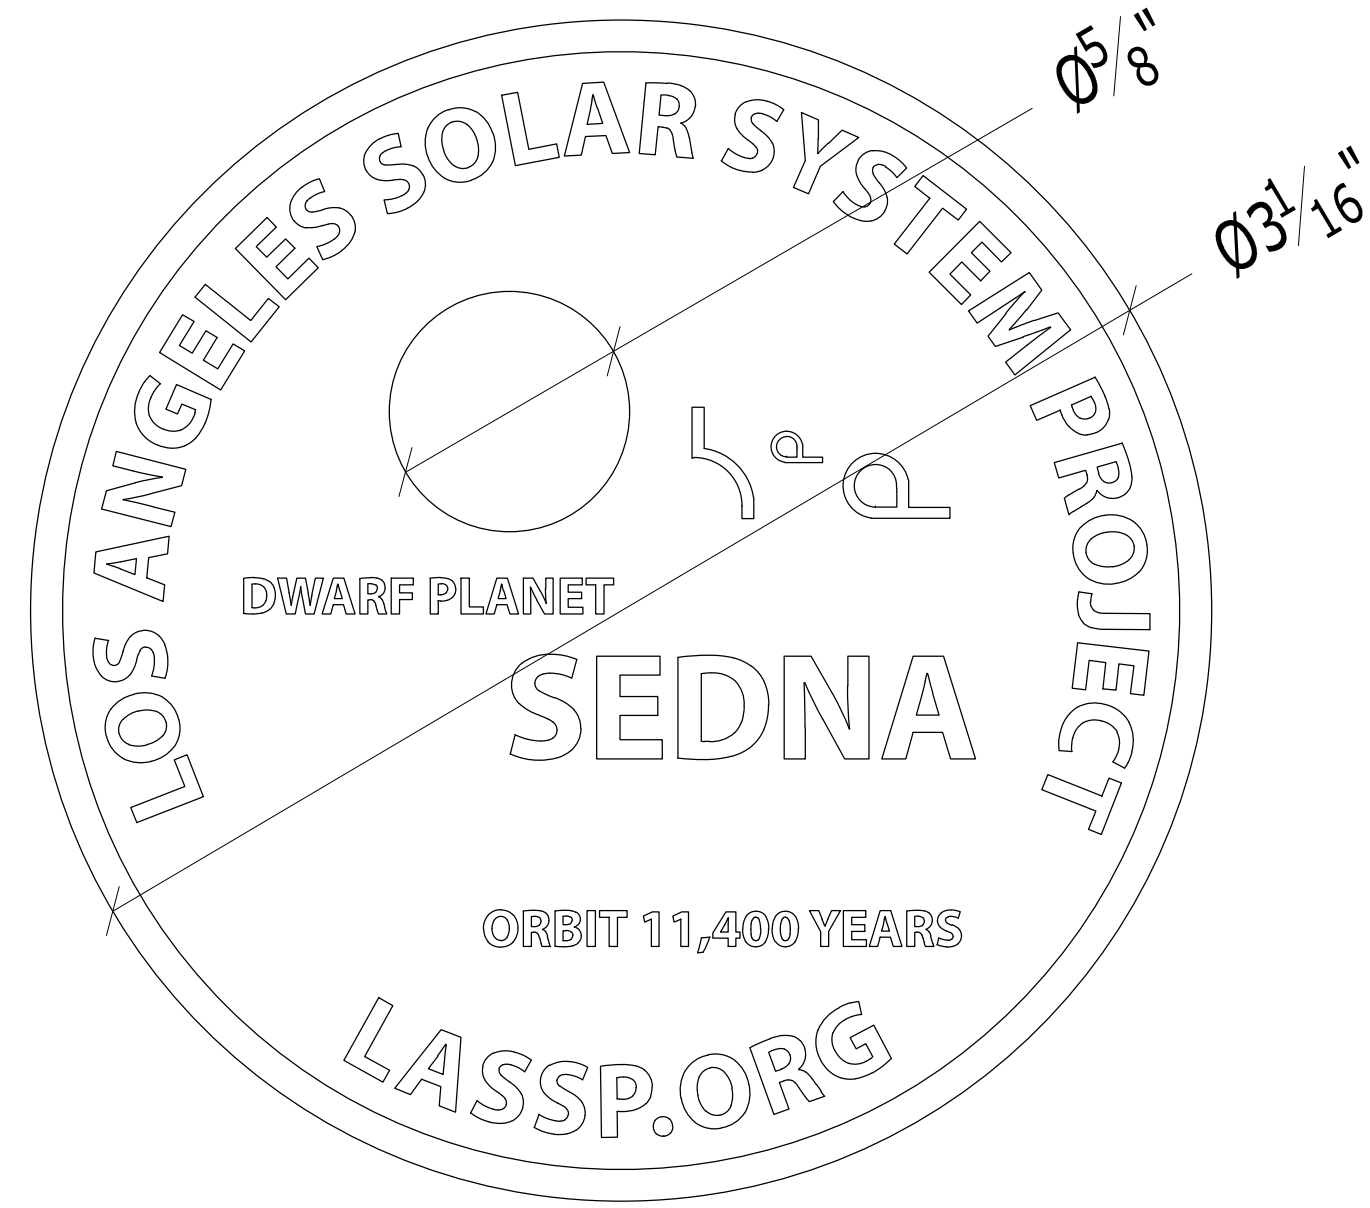

PLAN -
SCALE: FULL SCALE

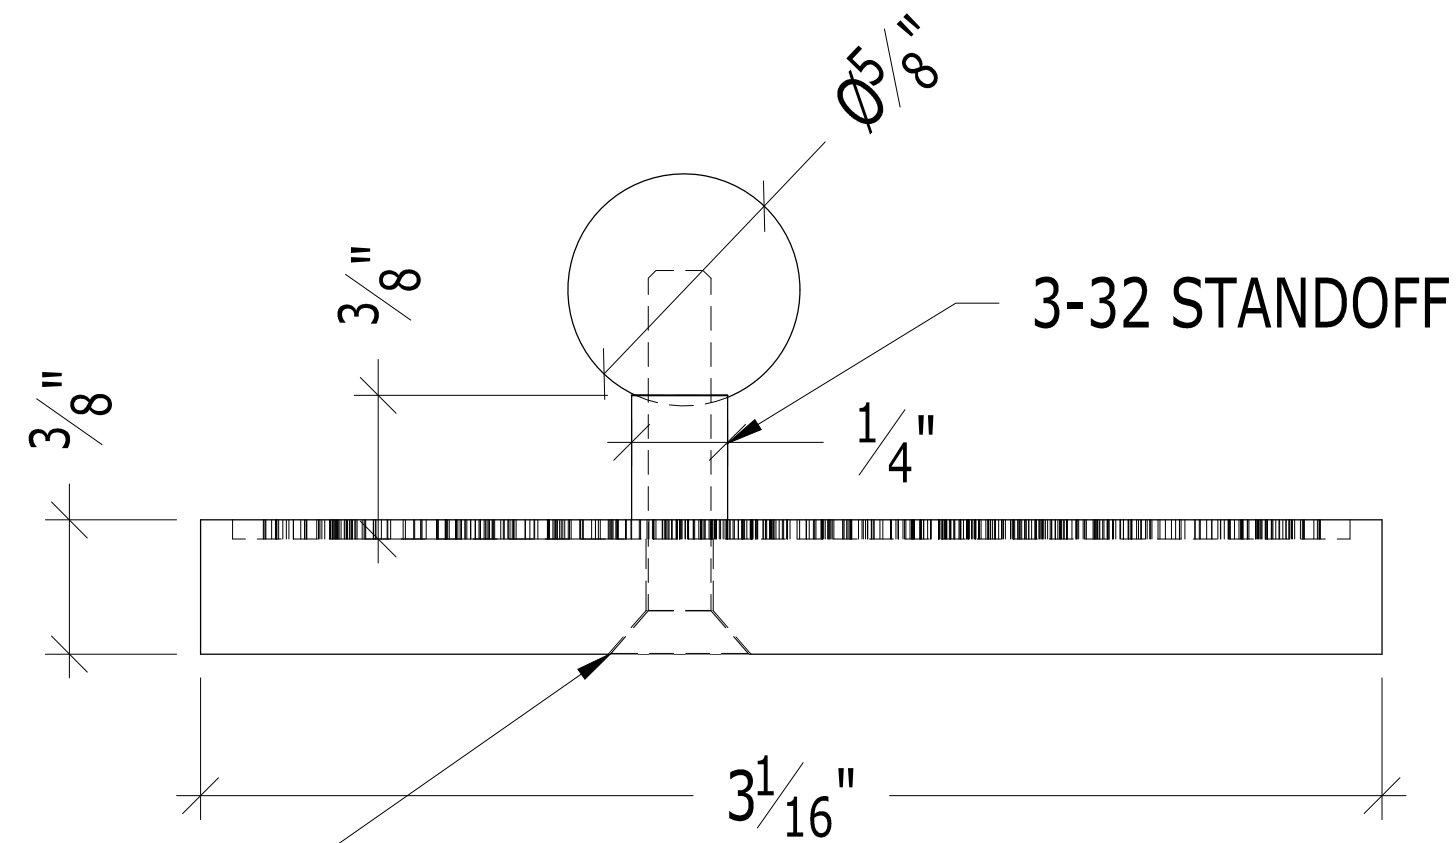

8-32 x 1" F.HD. MACH. SCREW

A ELEVATION -
SCALE: FULL SCALE

FOR REVIEW


JACK ANDERSON
FABRICATION DESIGN
3326 CAZADOR STREET
LOS ANGELES CA 90065
623-419-4802
jack4congrss@protonmail.com

LOS ANGELES SOLAR SYSTEM PROJECT


2800 E. Observatory Rd
Los Angeles, CA 90027

WALL MOUNT DWARF PLANET / ASTEROID


DRAWN BY	JACK
DRAWING DATE	2-5-2026
REVISION DATE	--/--/----
TITLE	ELEVATION, SECTIONS
SCALE	AS NOTED
SHEET	SE101

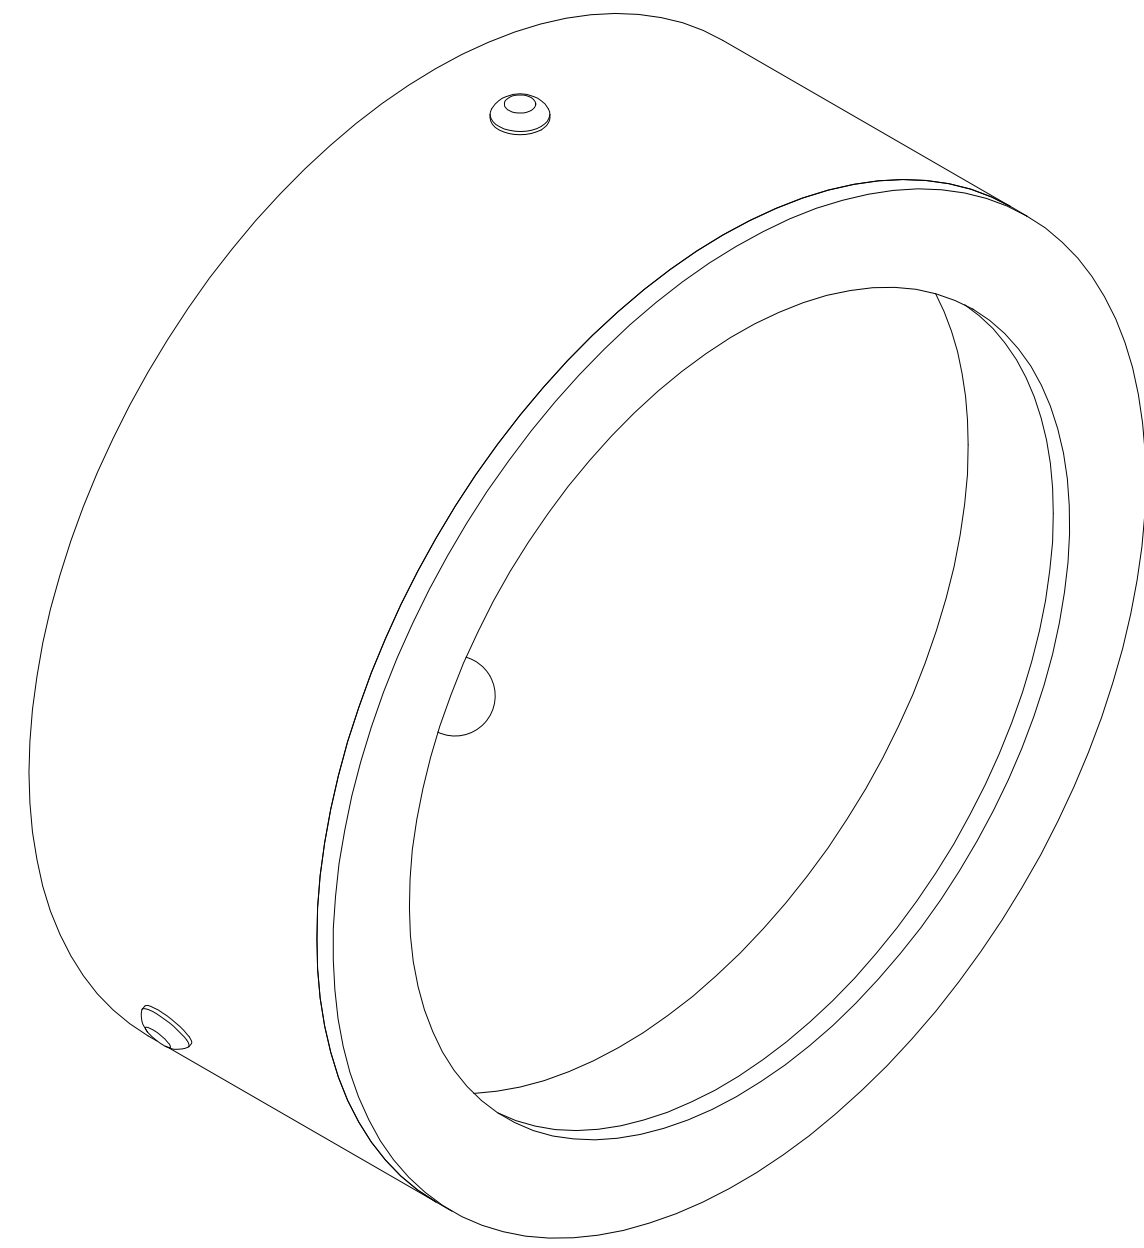


ISO VIEW
NTS

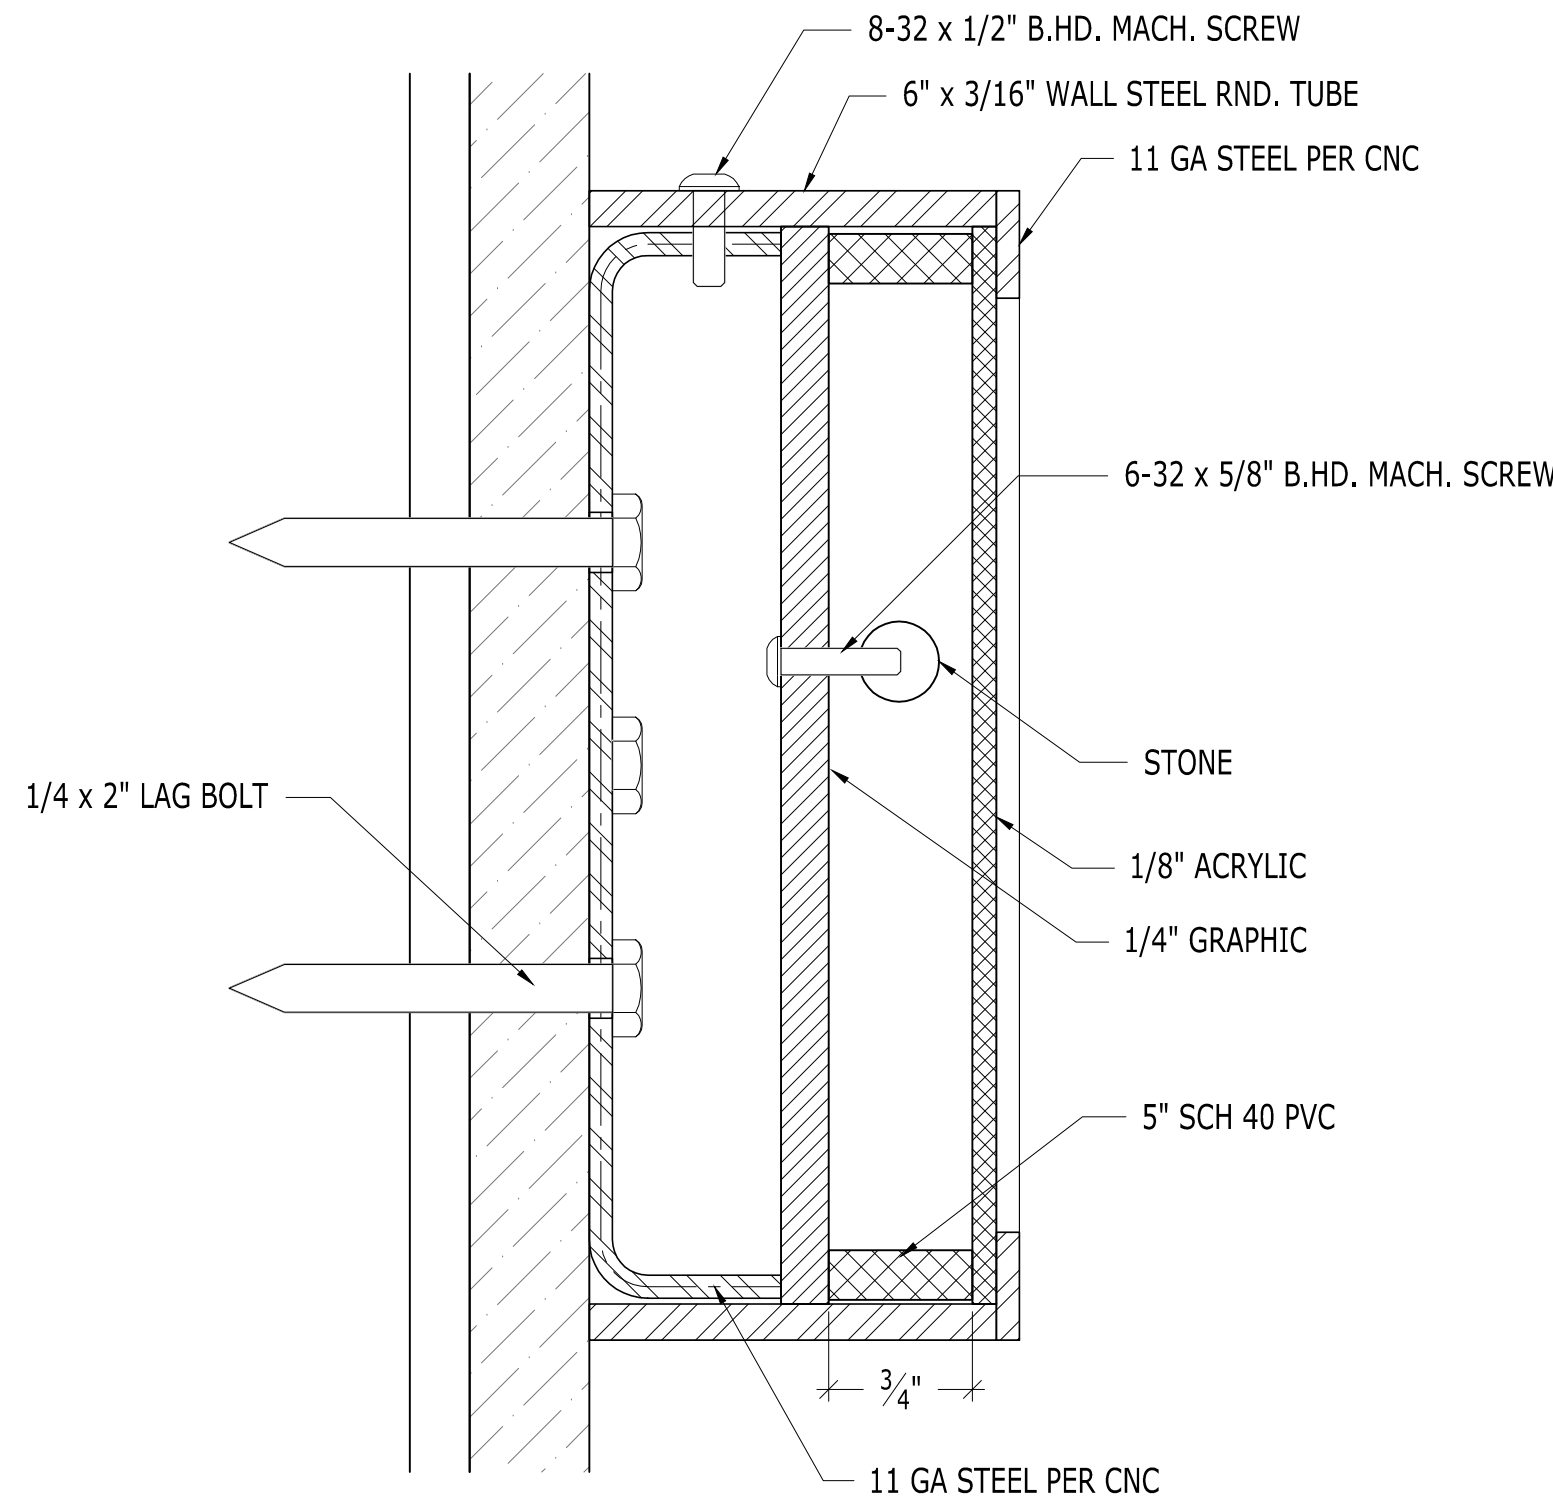


1 SECTION -
SCALE: FULL SCALE

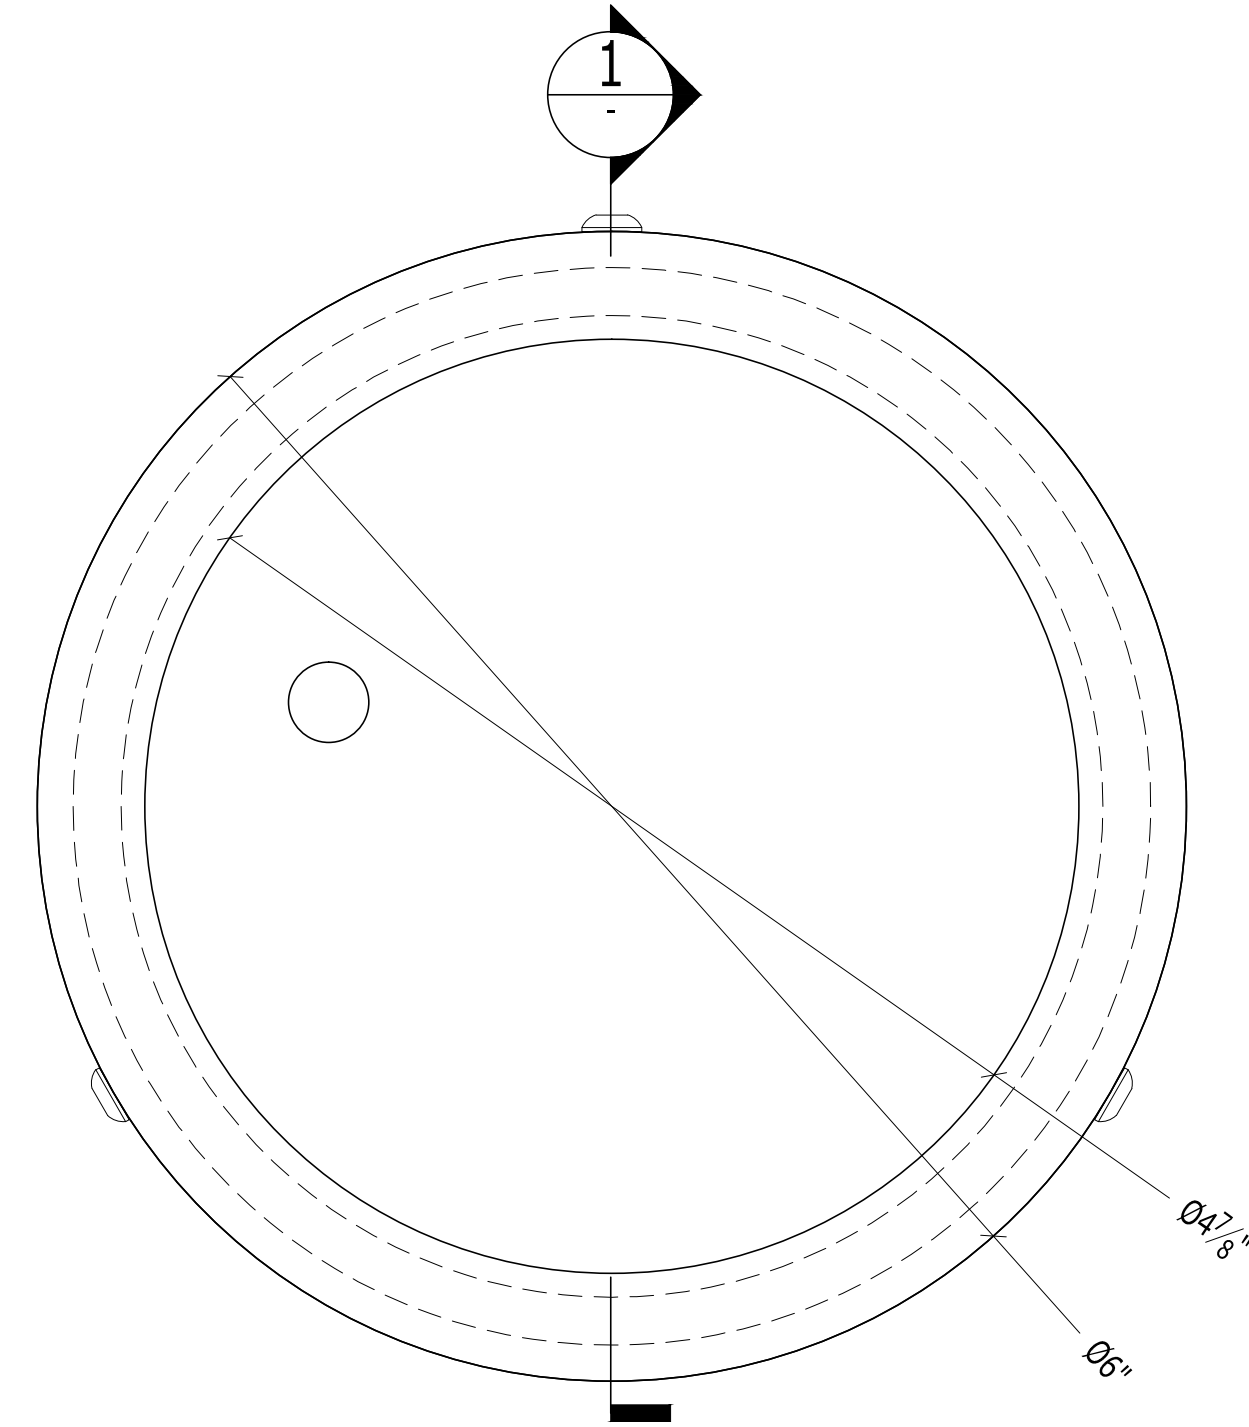

A ELEVATION -
SCALE: FULL SCALE

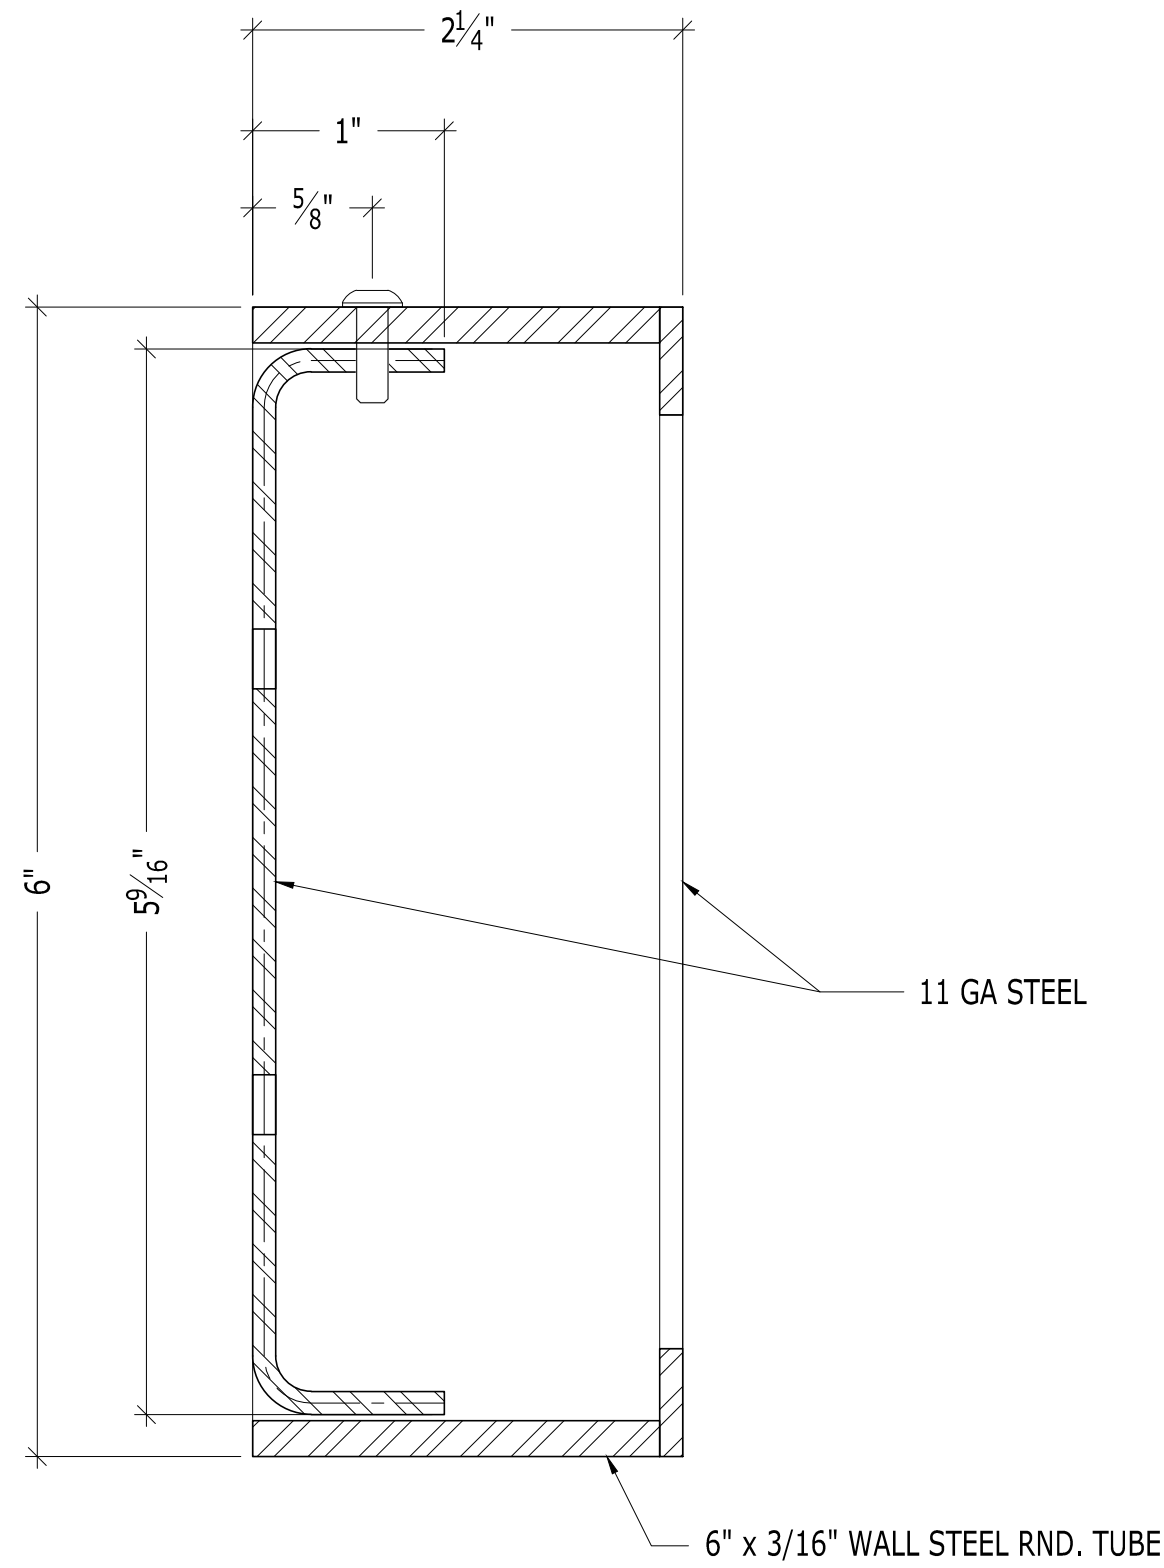

2 SECTION - STEEL
SCALE: FULL SCALE

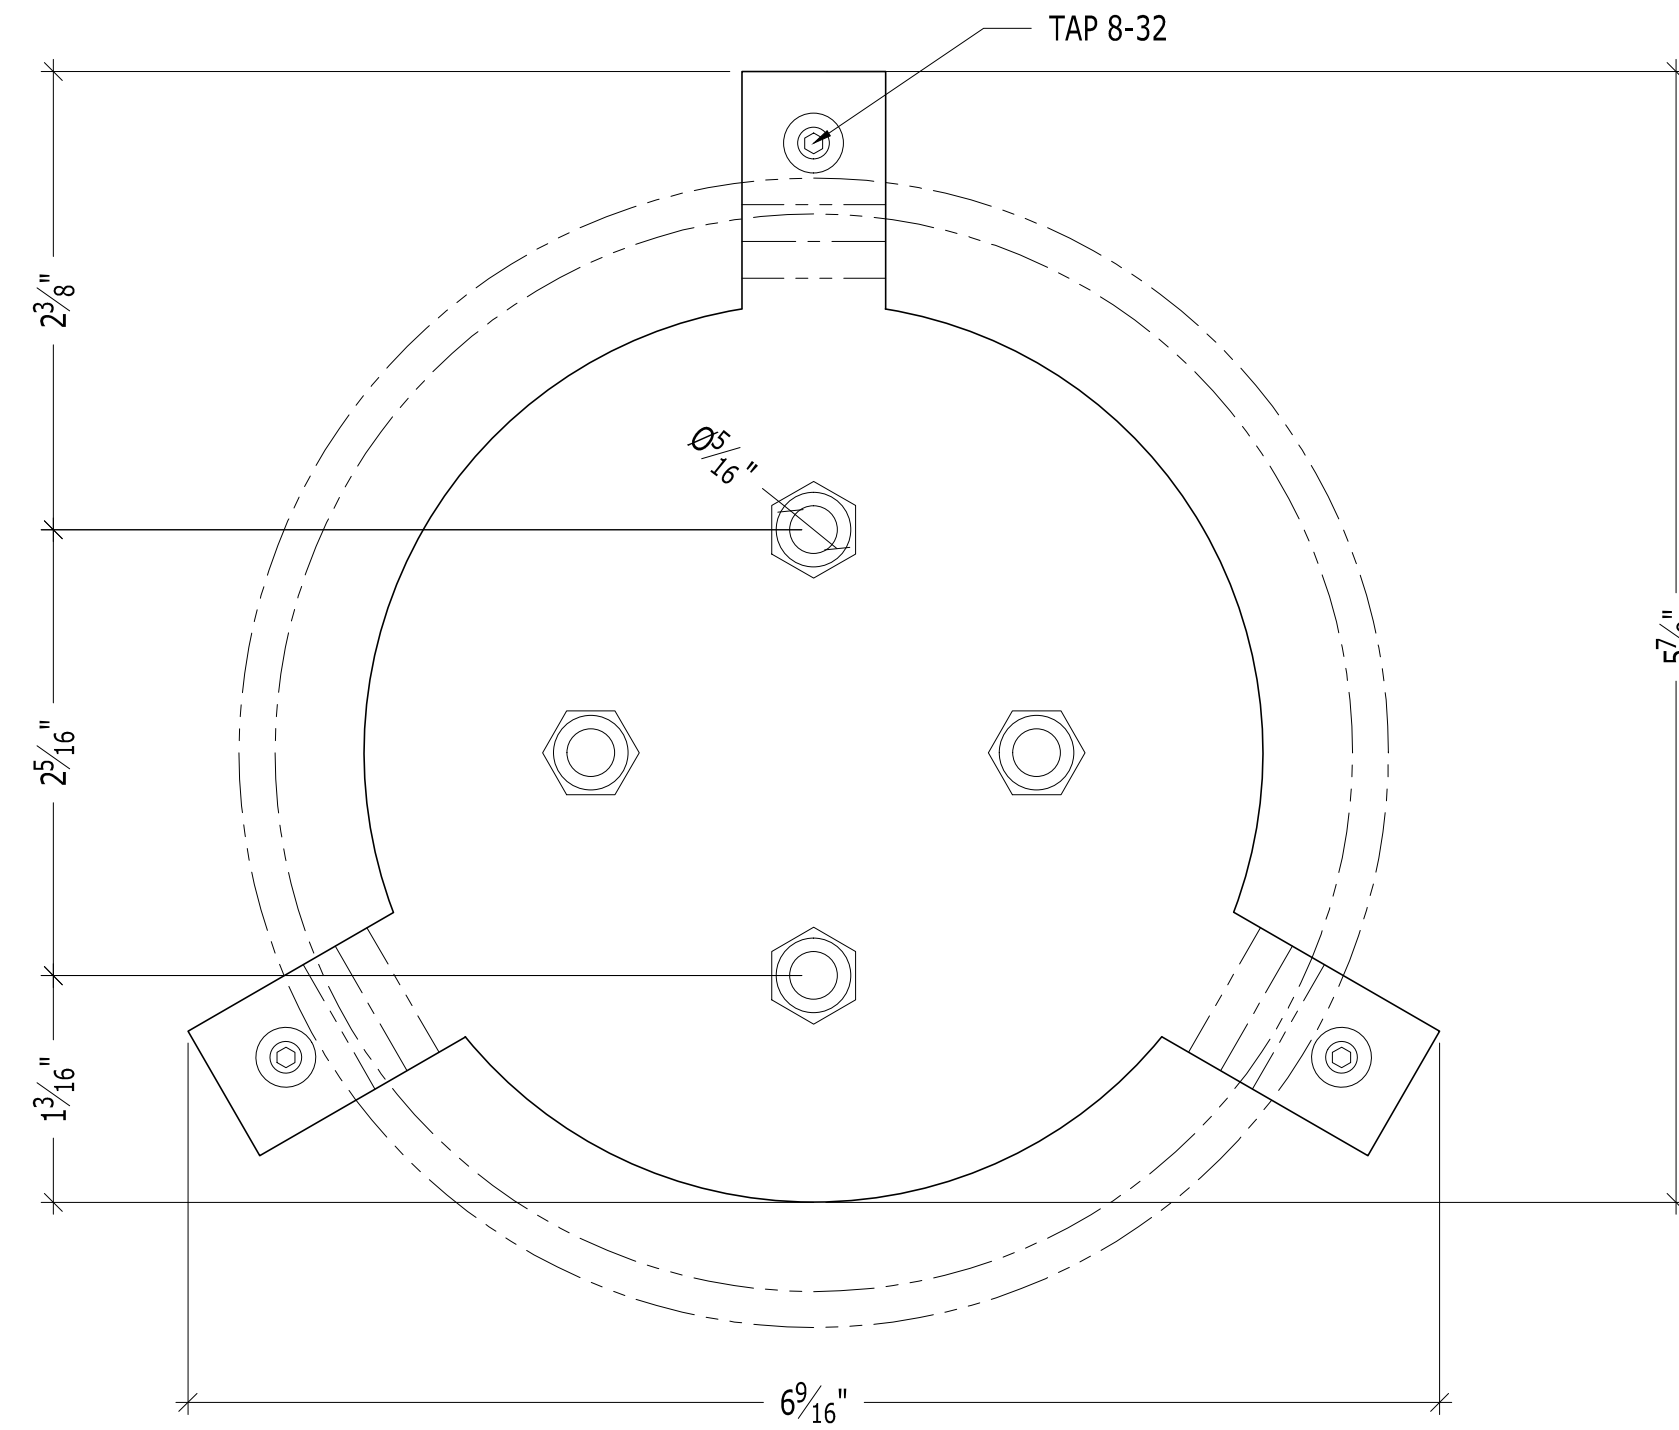

3 DETAIL - BACK PLATE PER CNC
SCALE: FULL SCALE

FOR REVIEW

JACK ANDERSON
FABRICATION DESIGN
3326 CAZADOR STREET
LOS ANGELES CA 90065
623-419-4802
jack4congrss@protonmail.com

LOS ANGELES SOLAR SYSTEM PROJECT
WALL MOUNT DWARF PLANET / ASTEROID
2800 E. Observatory Rd
Los Angeles, CA 90027

DRAWN BY	JACK
DRAWING DATE	2-5-2026
REVISION DATE	--/------
TITLE	ELEVATION, SECTIONS
SCALE	AS NOTED
SHEET	AS900